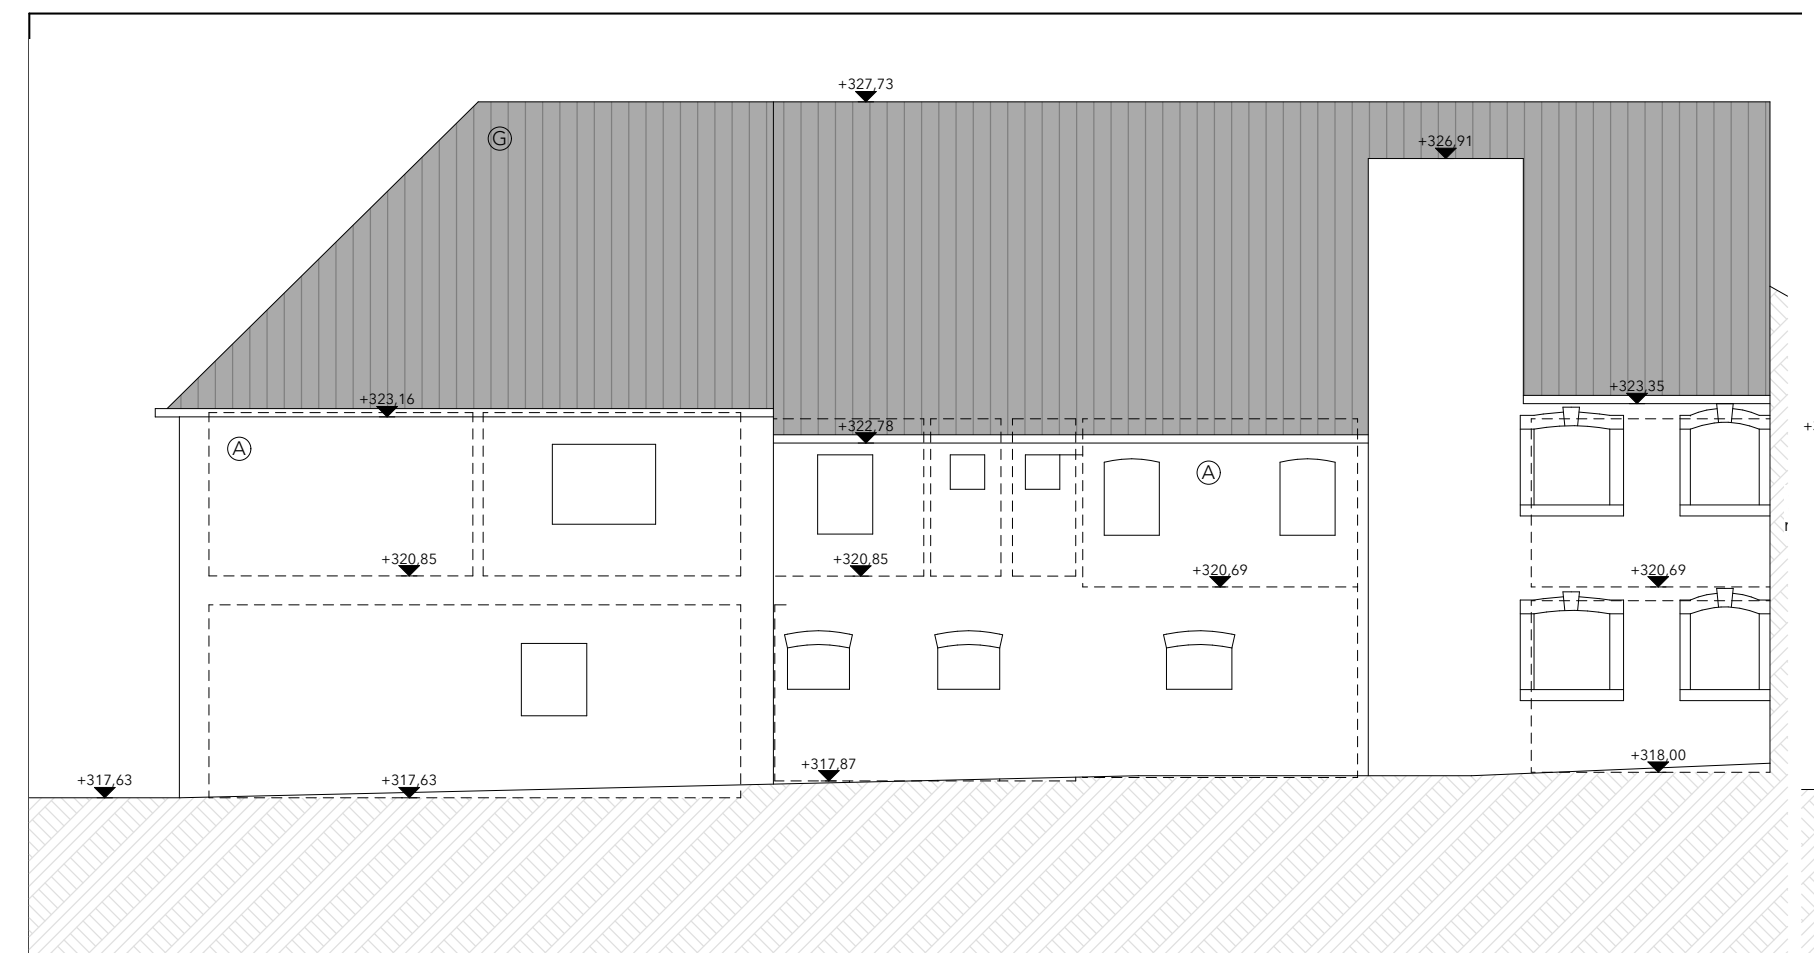

Vue en élévation - NE
situation existante
éch. 1/100e

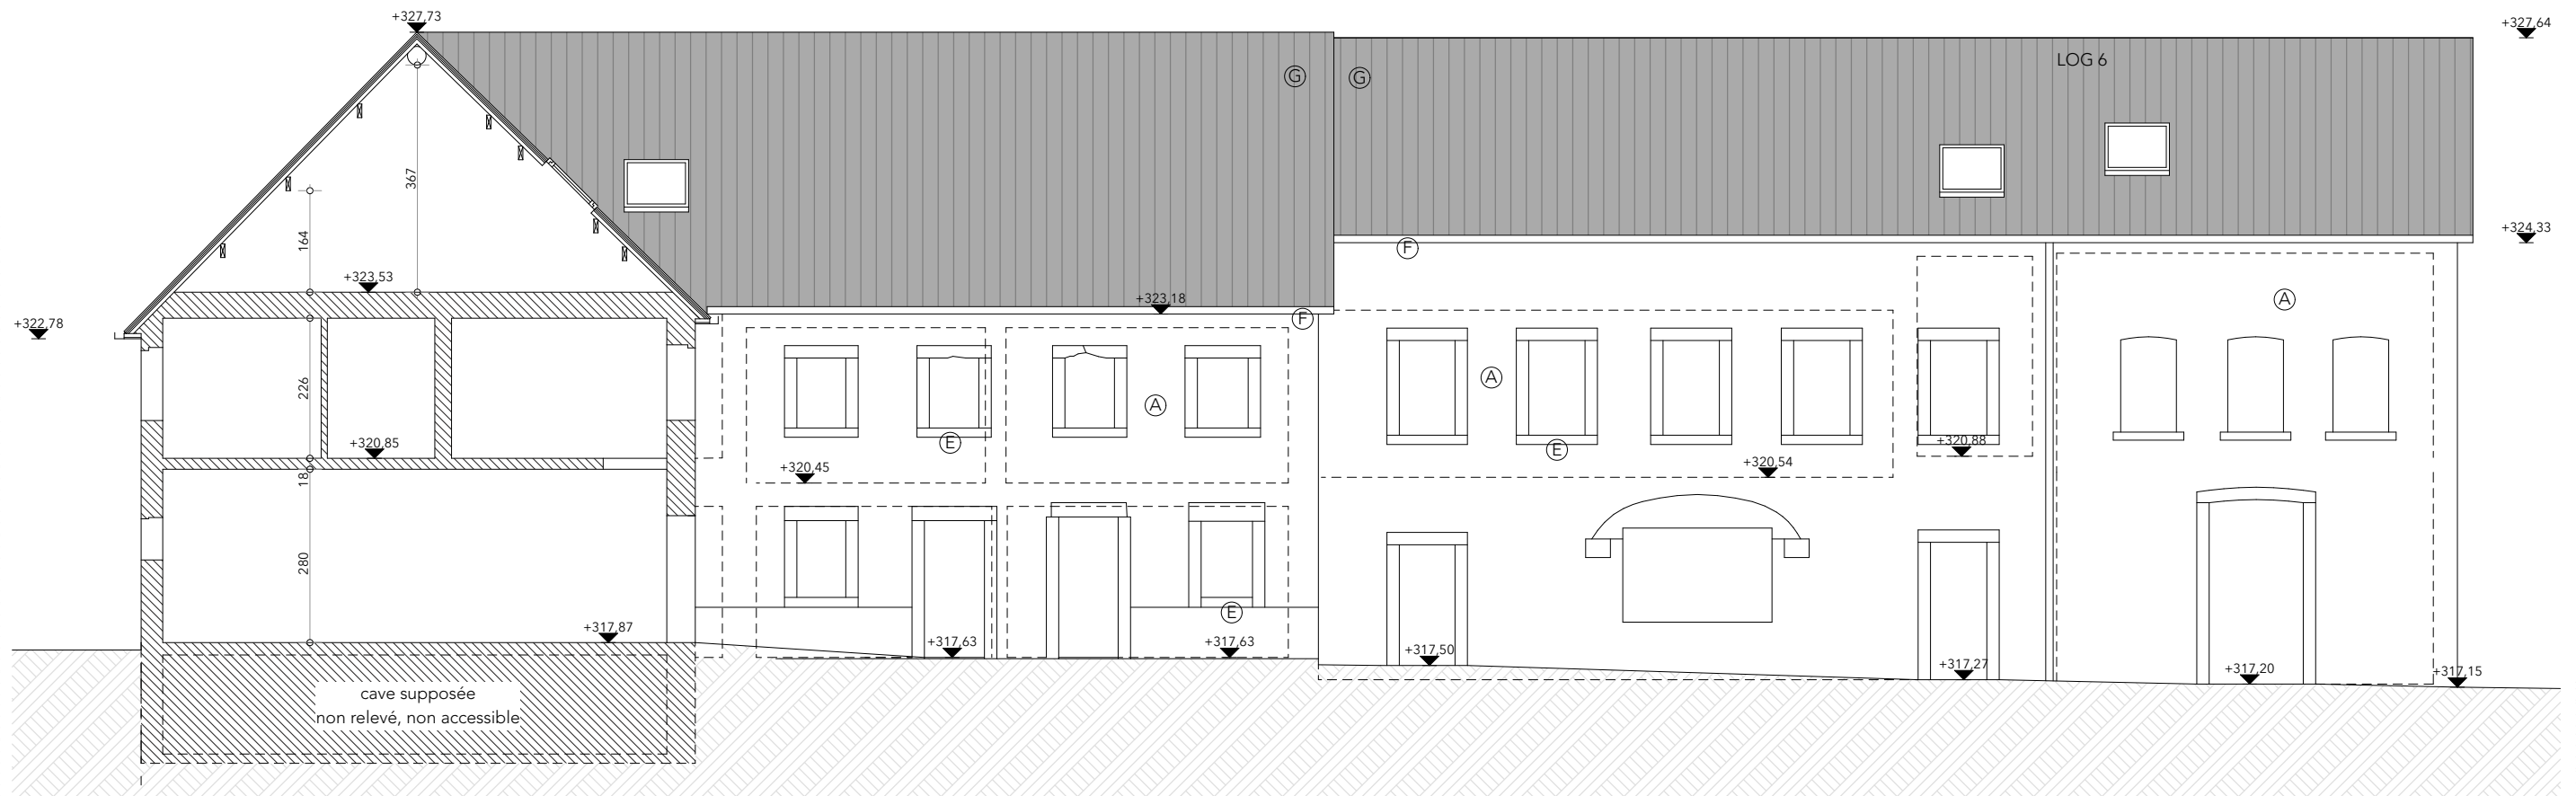

Vue en coupe AA
situation existante
éch. 1/100e

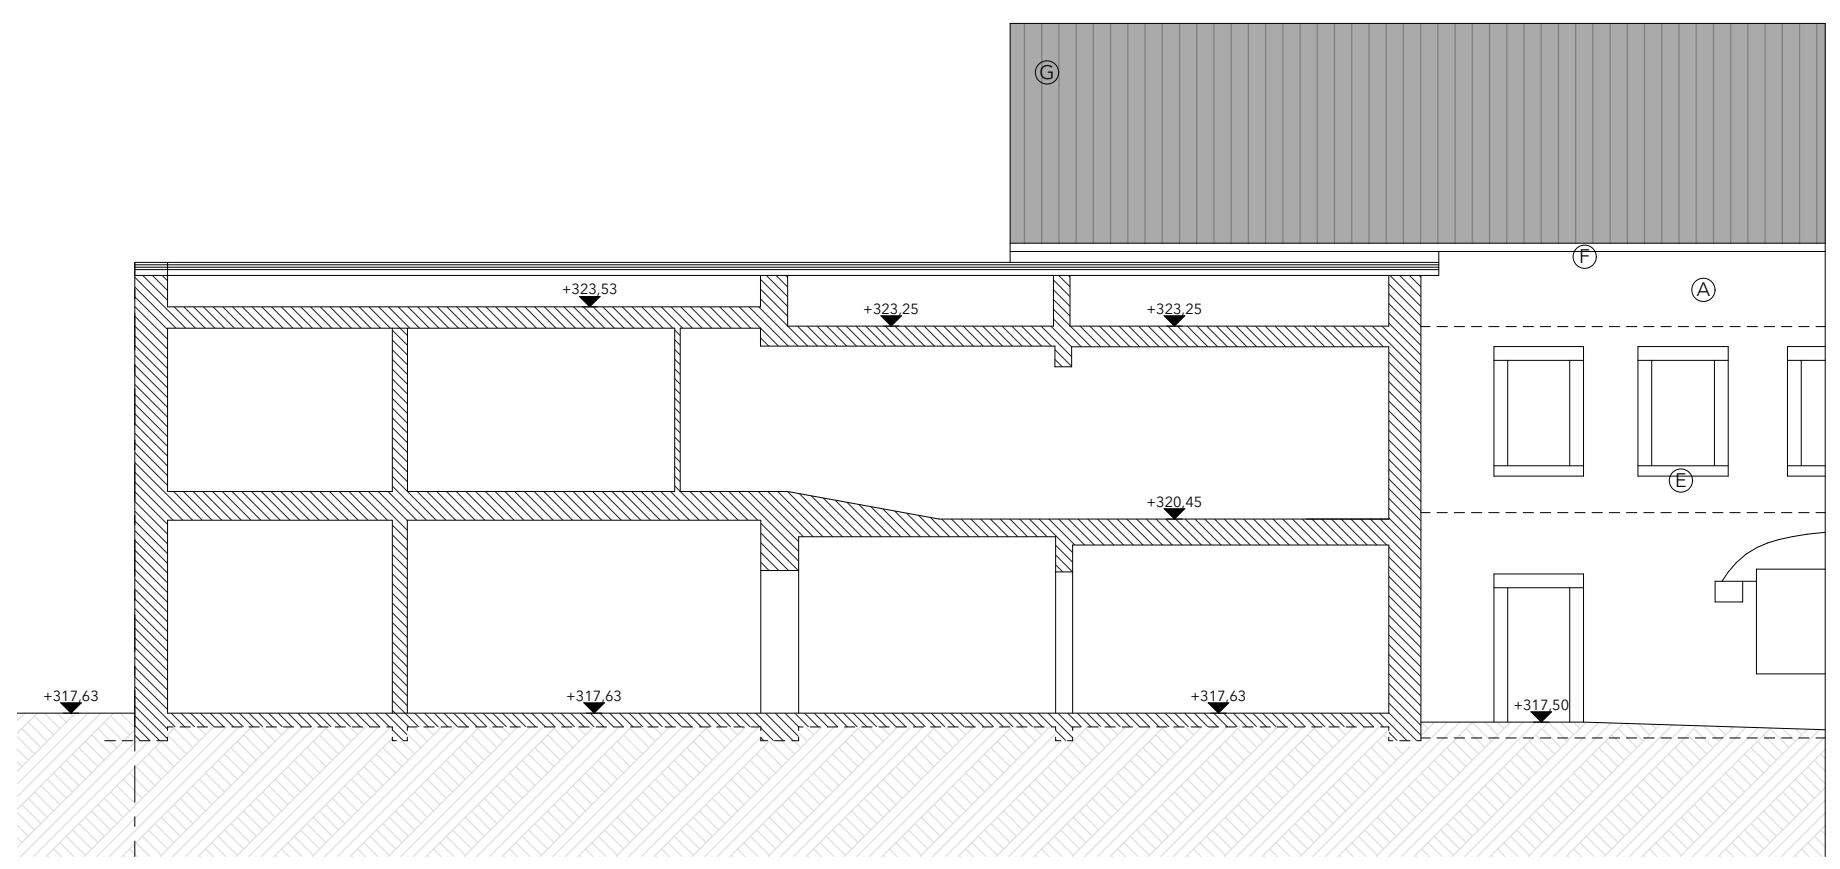

Vue en coupe BB
situation existante
éch. 1/100e

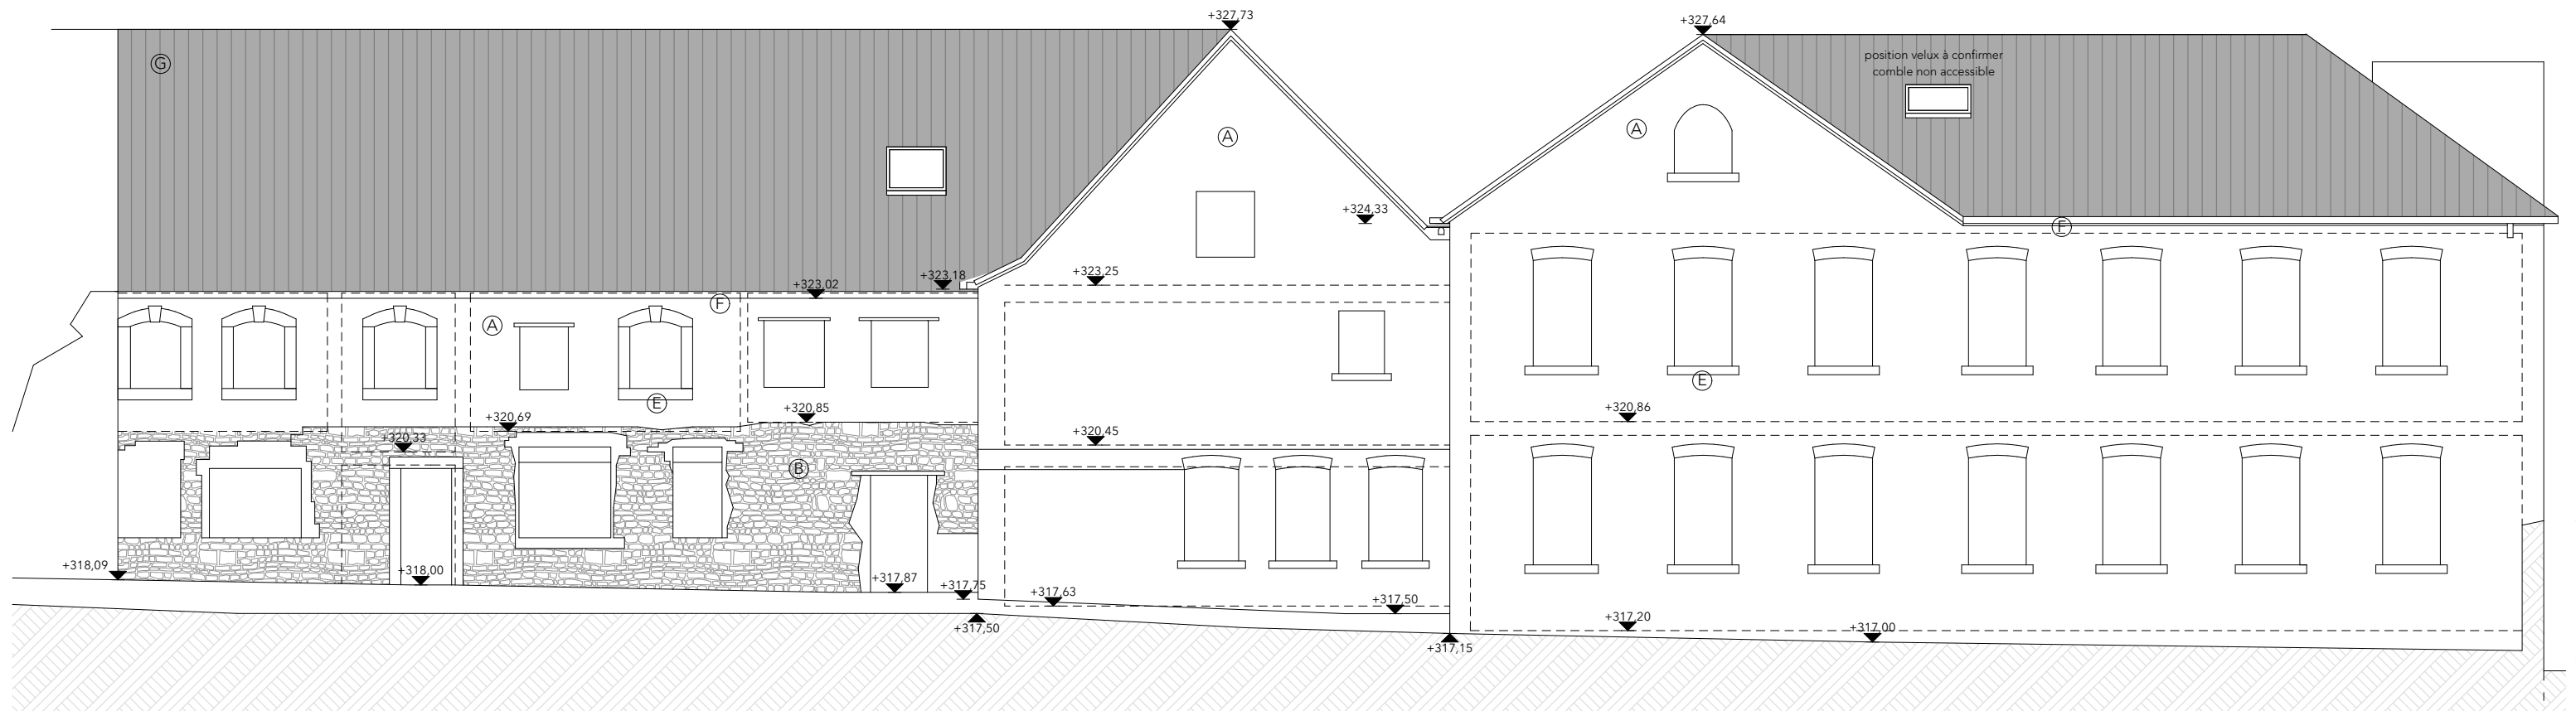

Vue en élévation - SE
situation existante
éch. 1/100e

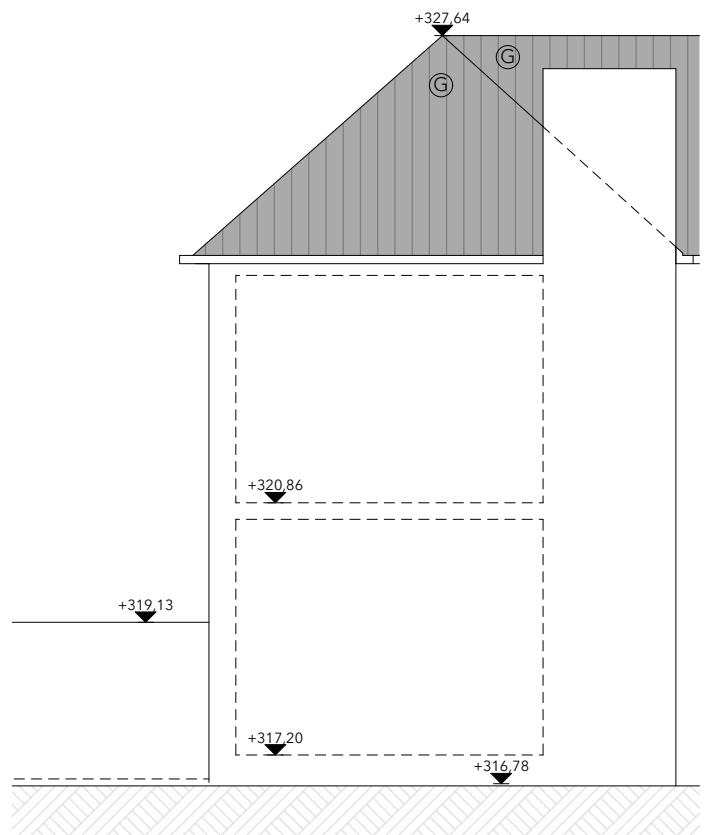

Vue en élévation - NE
situation existante
éch. 1/100e

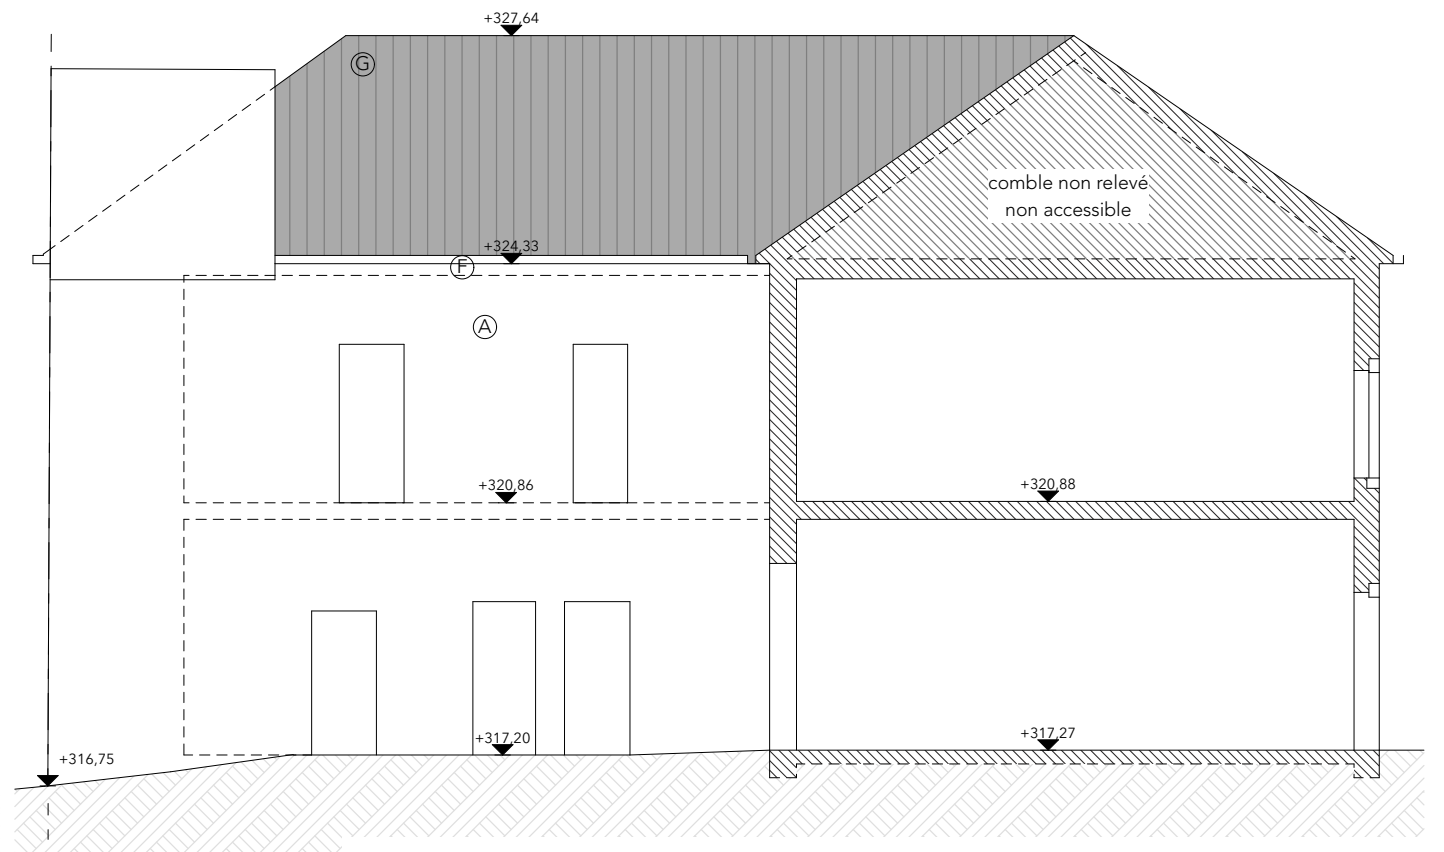

Vue en coupe - CC
situation existante
éch. 1/100e

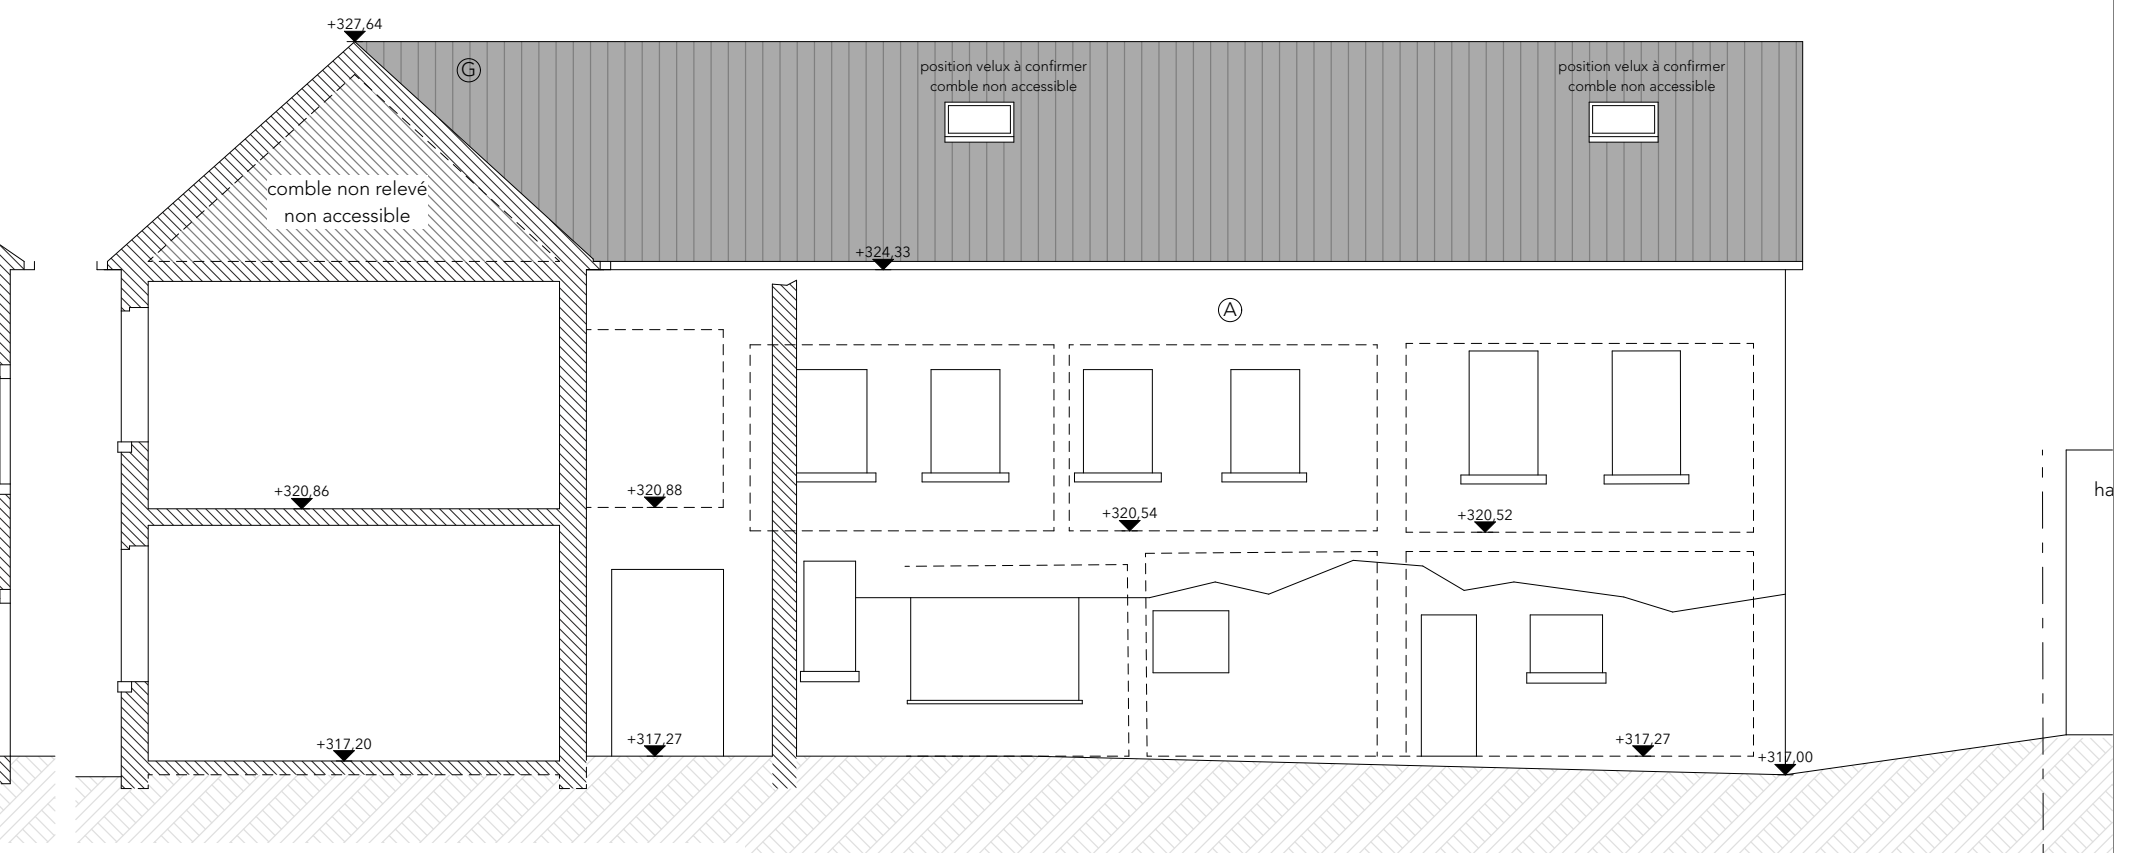

Vue en coupe - DD
situation existante
éch. 1/100e

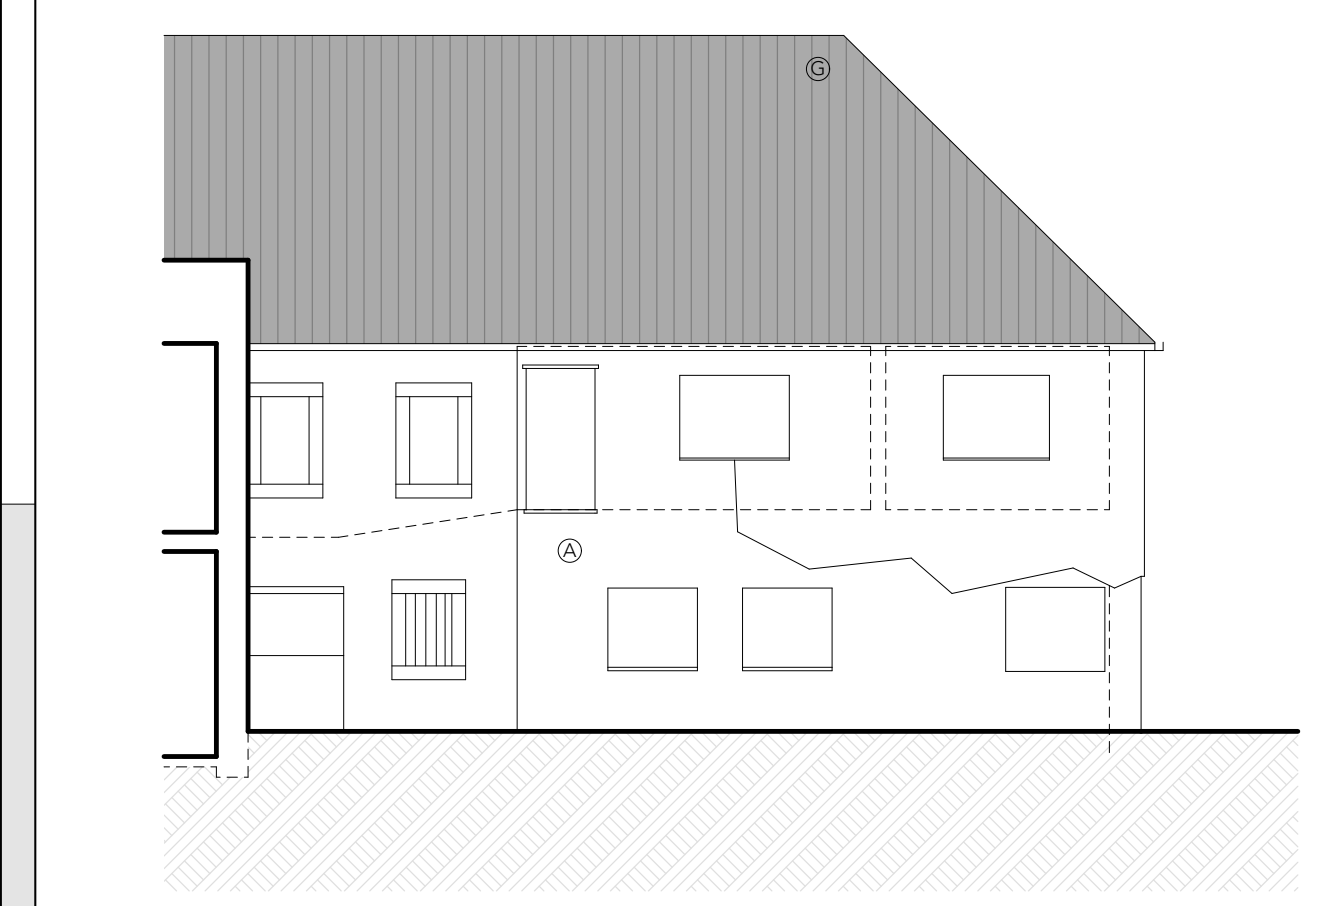

Vue en élévation NE
situation existante
éch. 1/100e

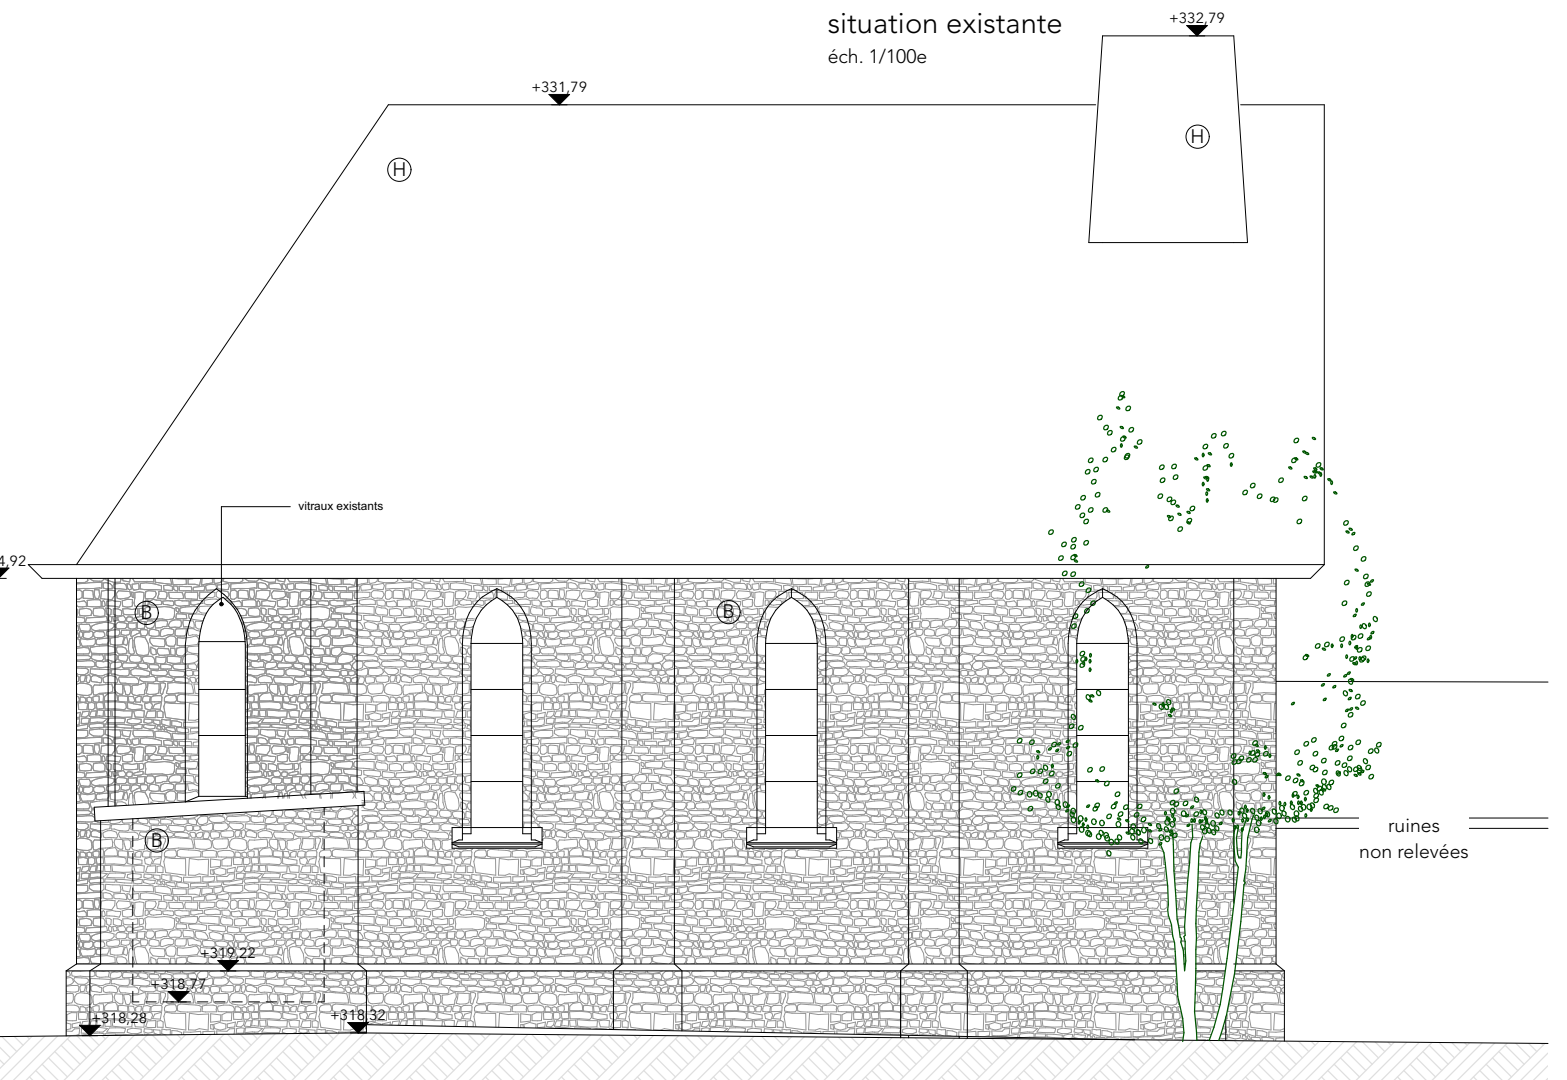

Vue en élévation - NO
situation existante
éch. 1/100e

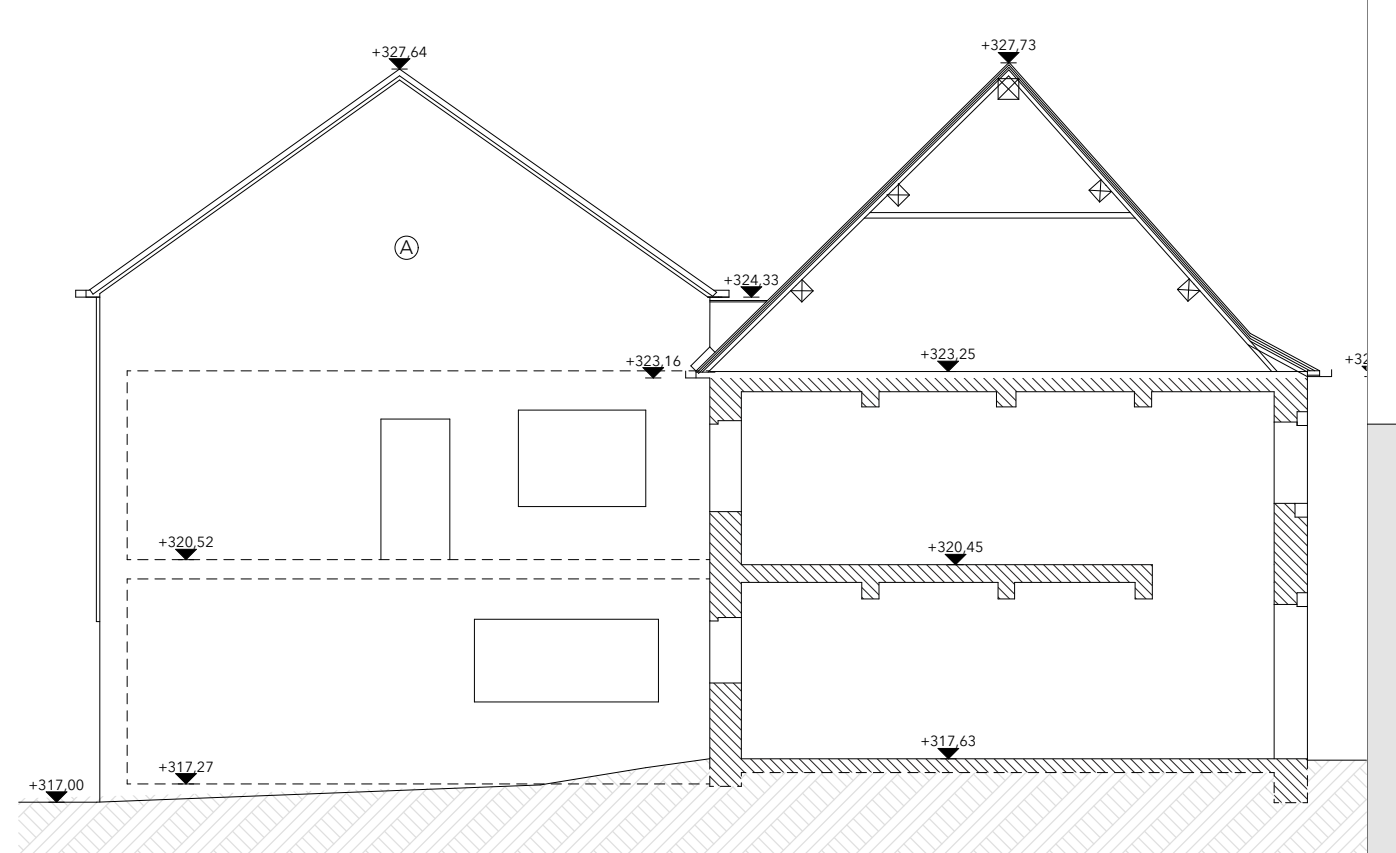

Vue en coupe - EE
situation existante
éch. 1/100e

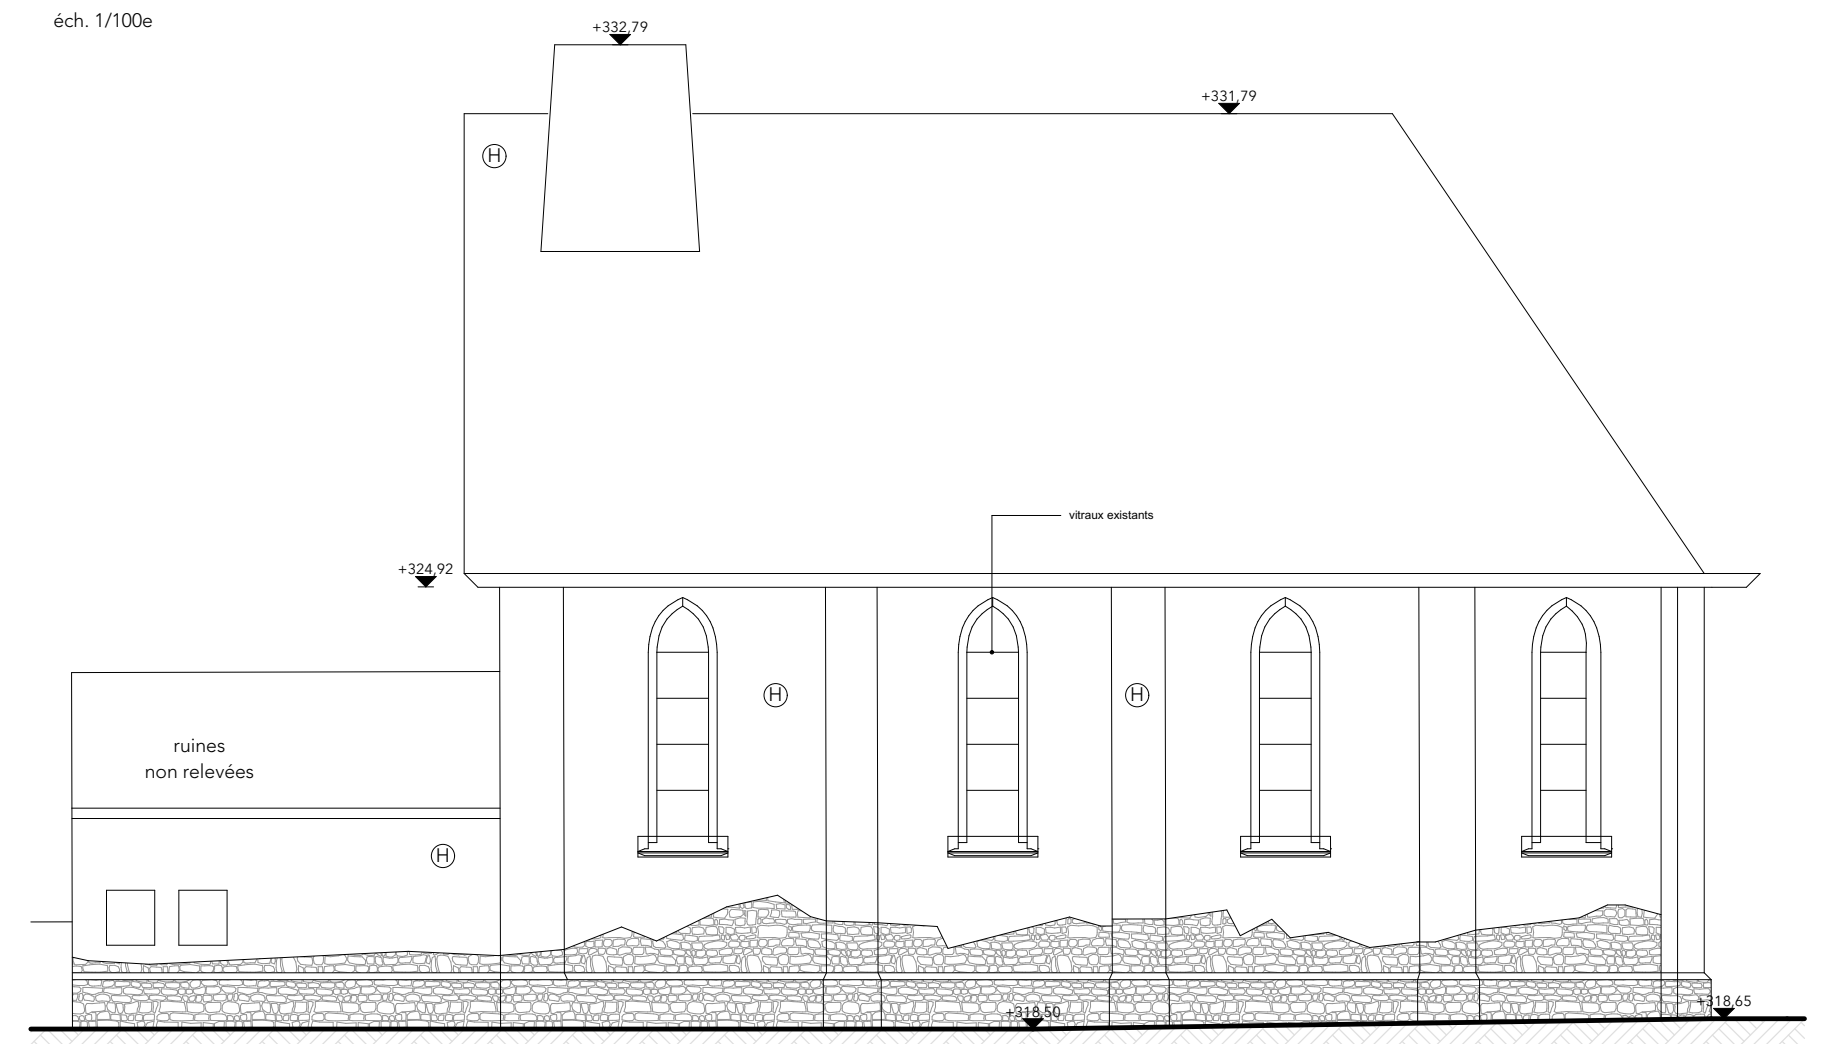

Vue en élévation - SO
situation existante
éch. 1/100e

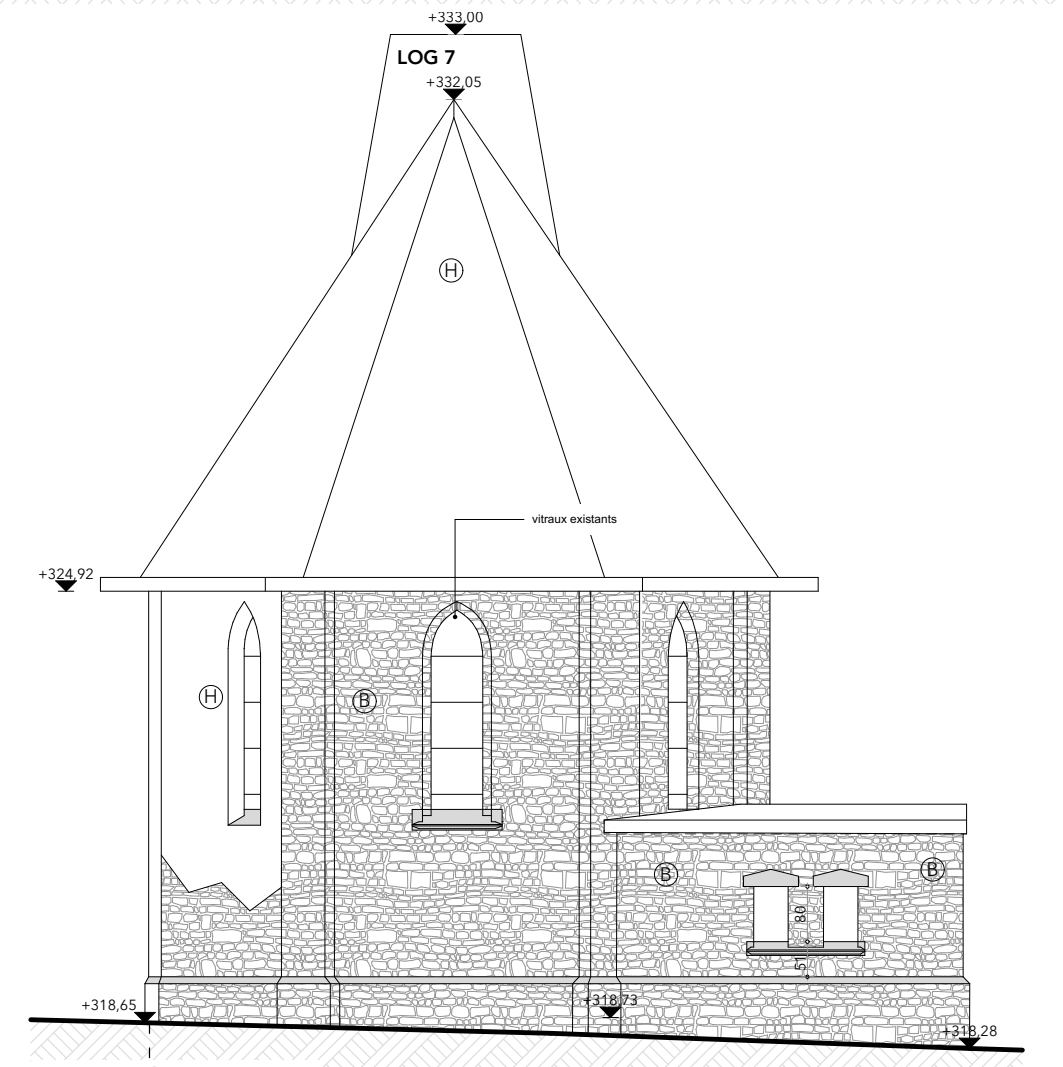

Vue en élévation - SE
situation existante
éch. 1/100e

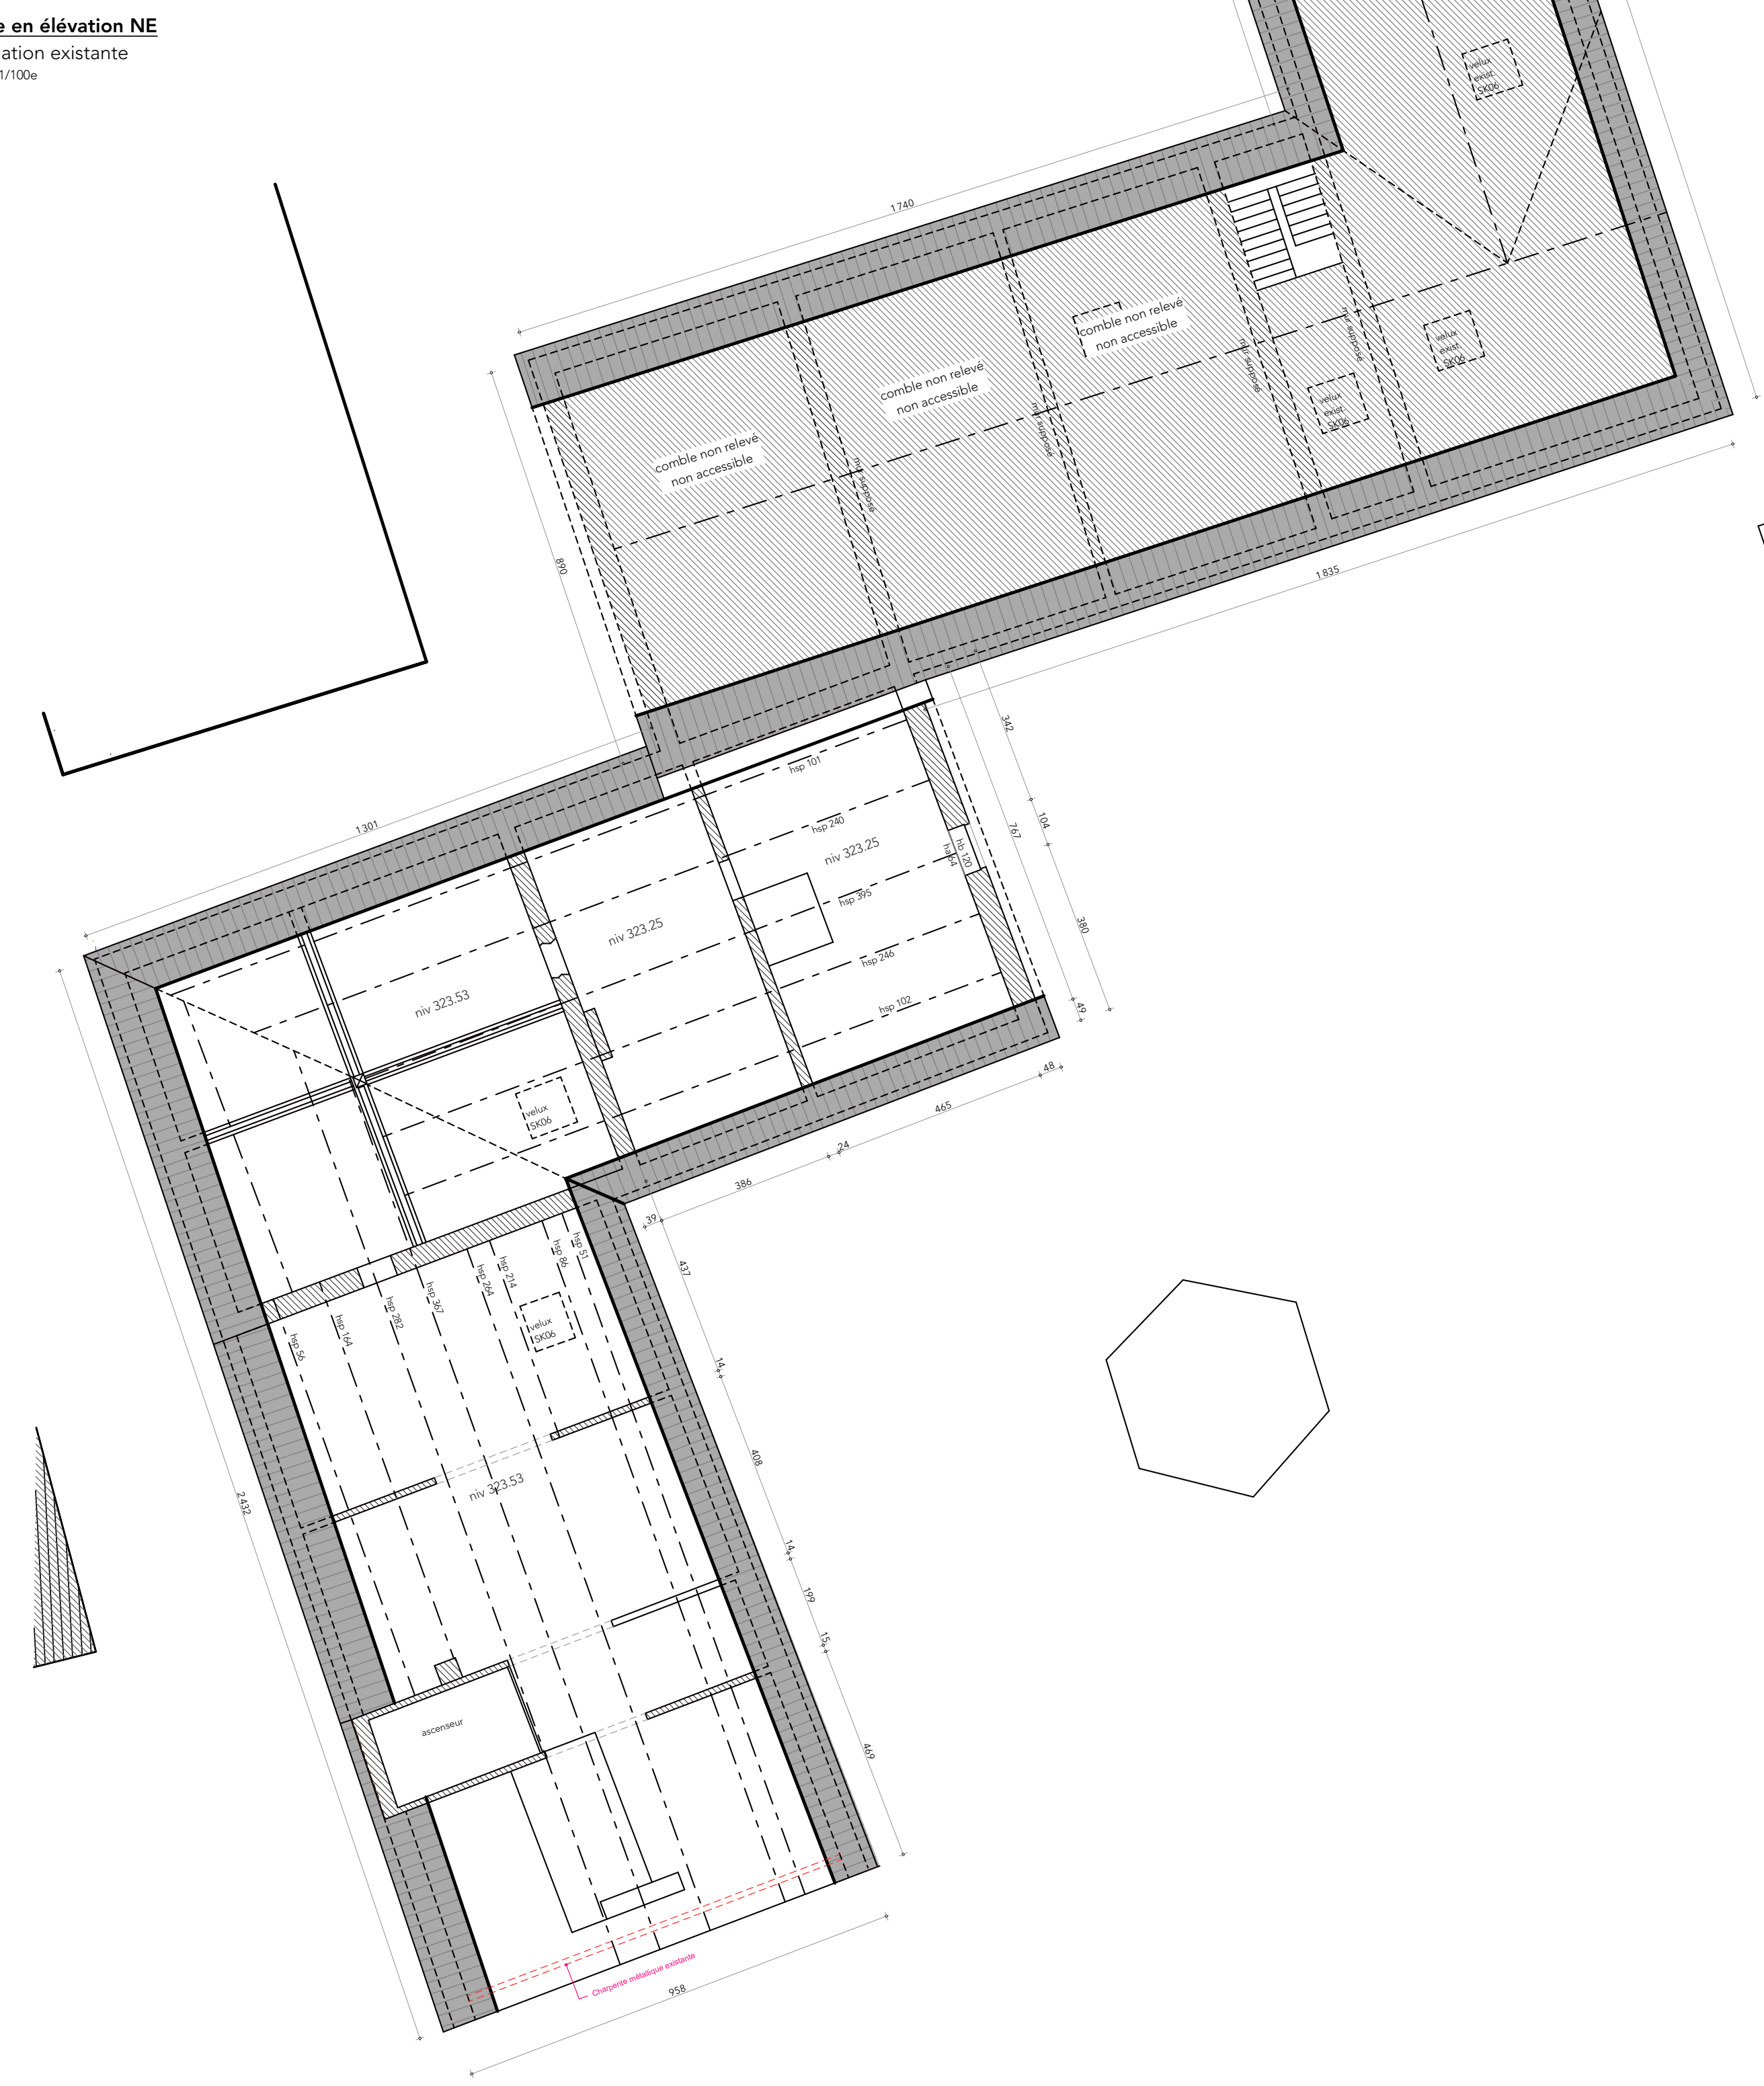

Vue en plan du 2ème étage
situation existante
éch. 1/100e

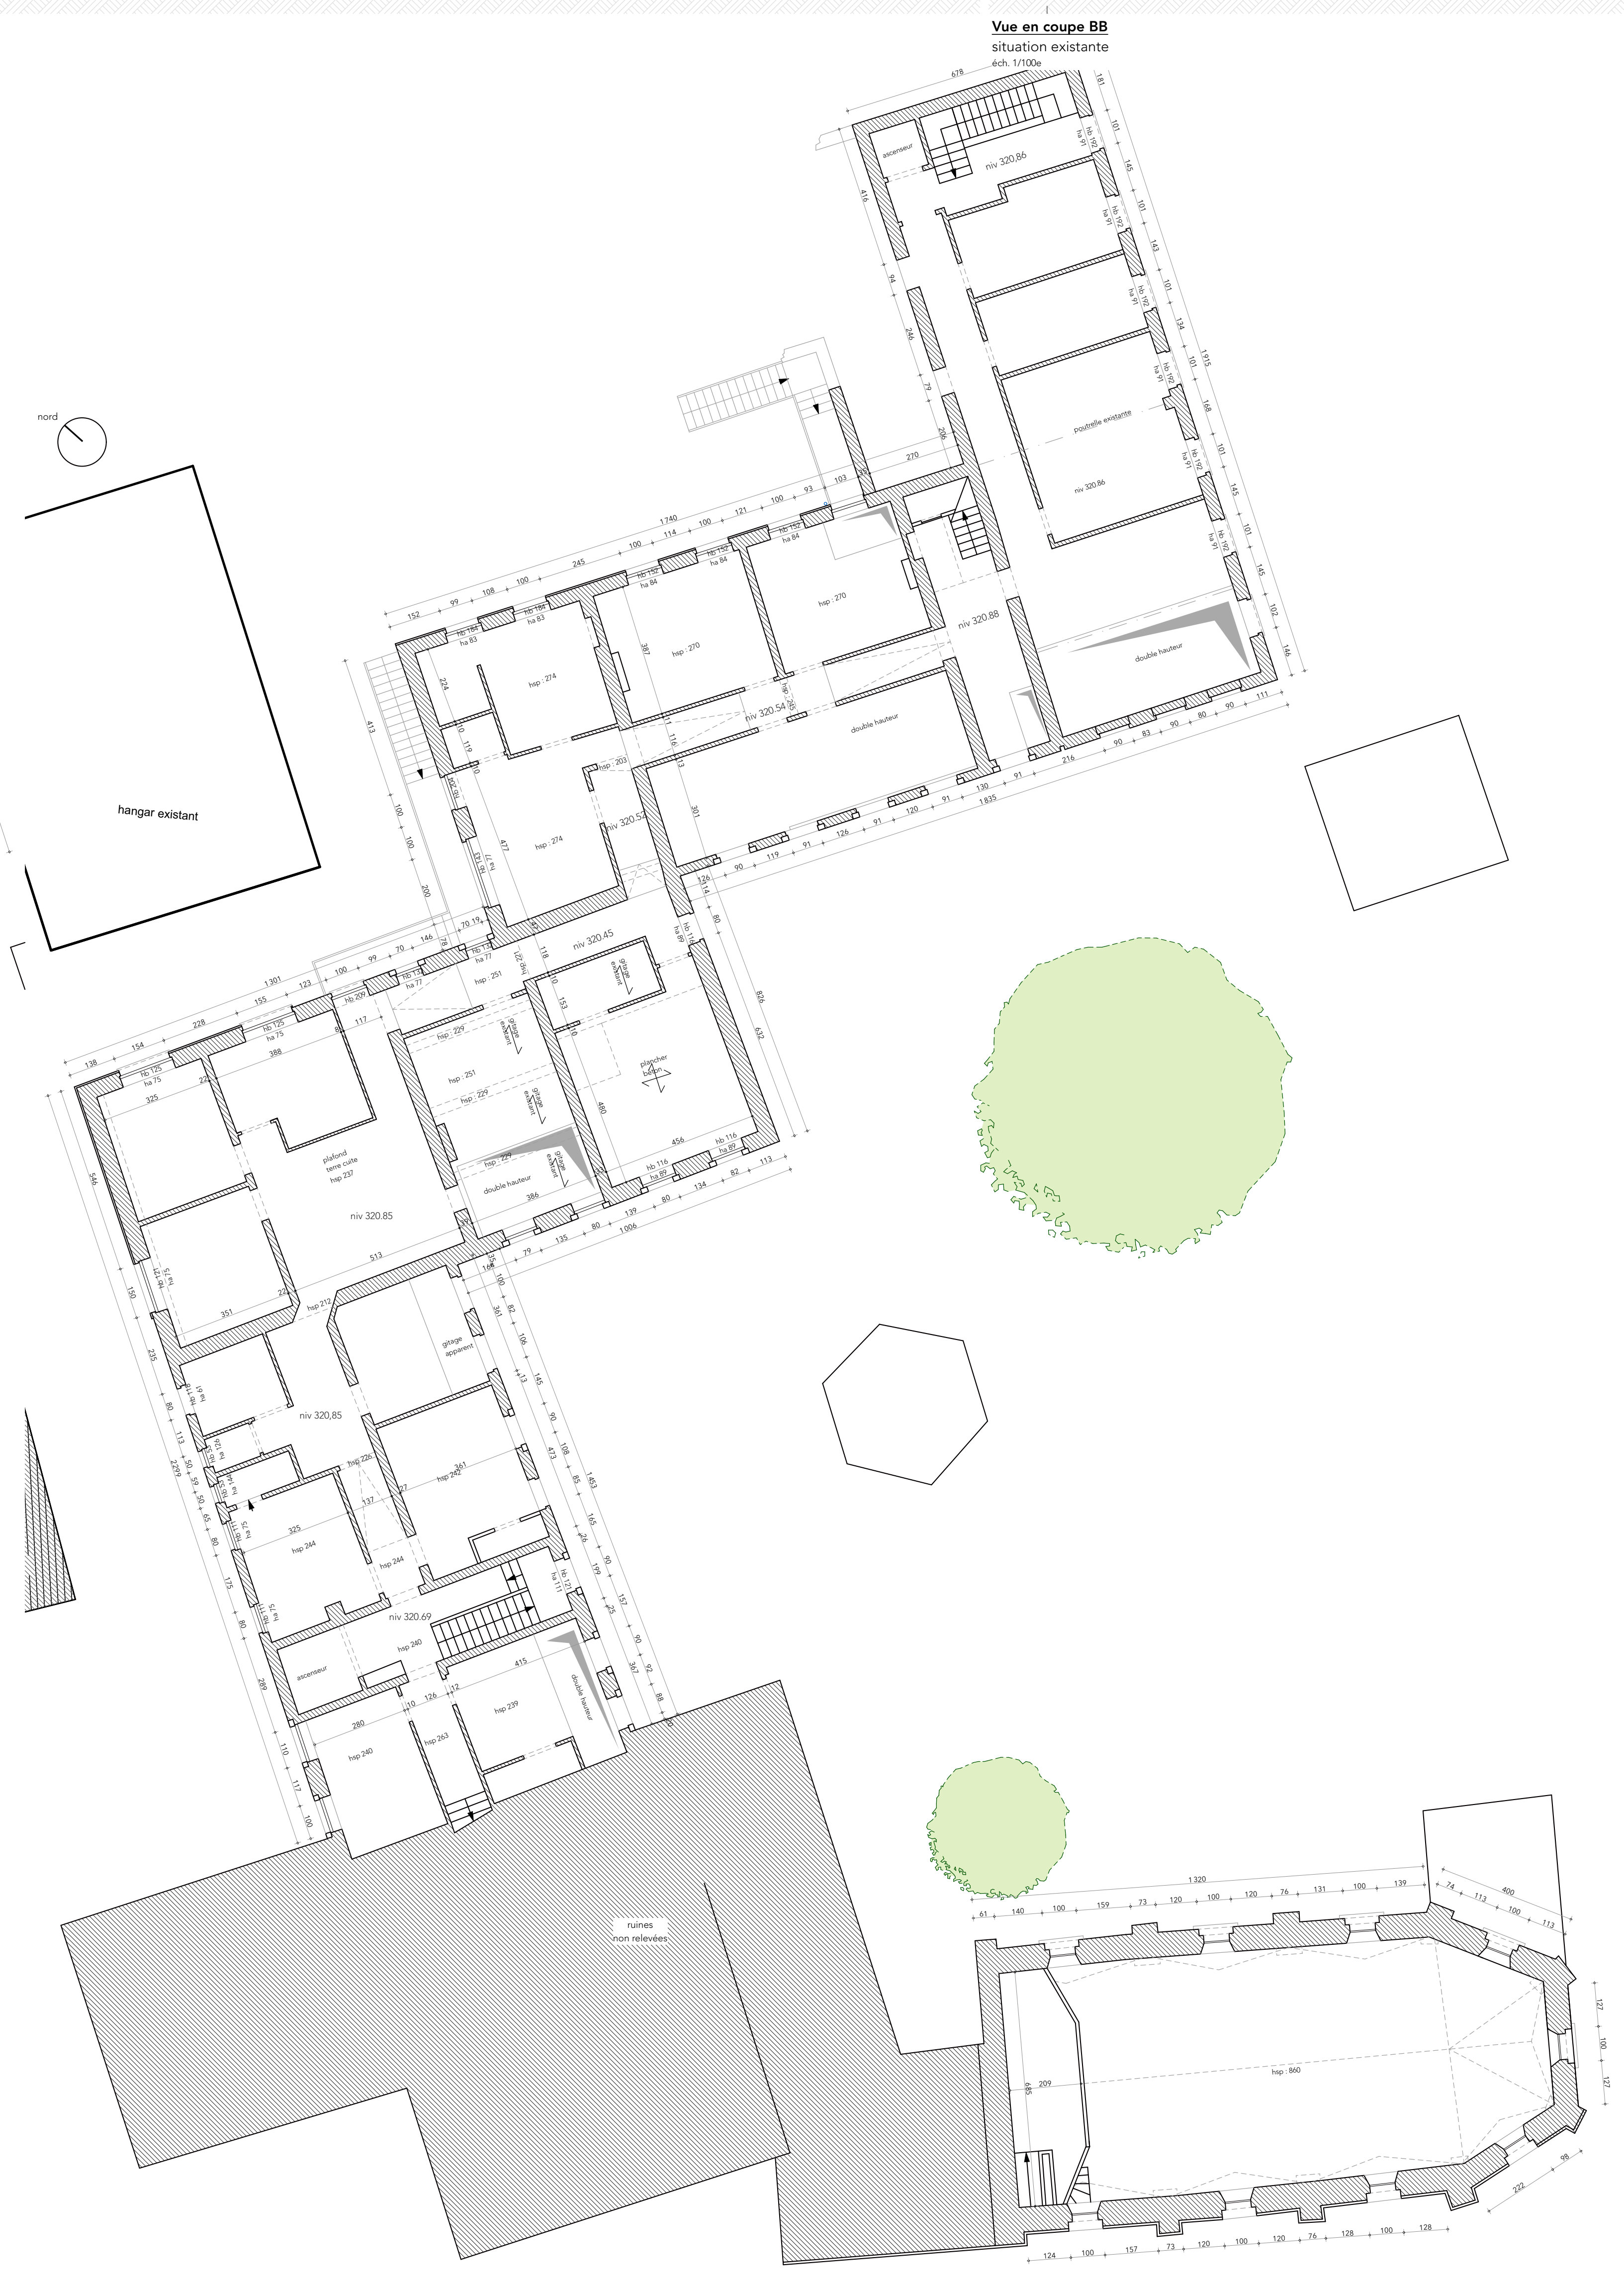

Vue en plan du 1er étage
situation existante
éch. 1/100e

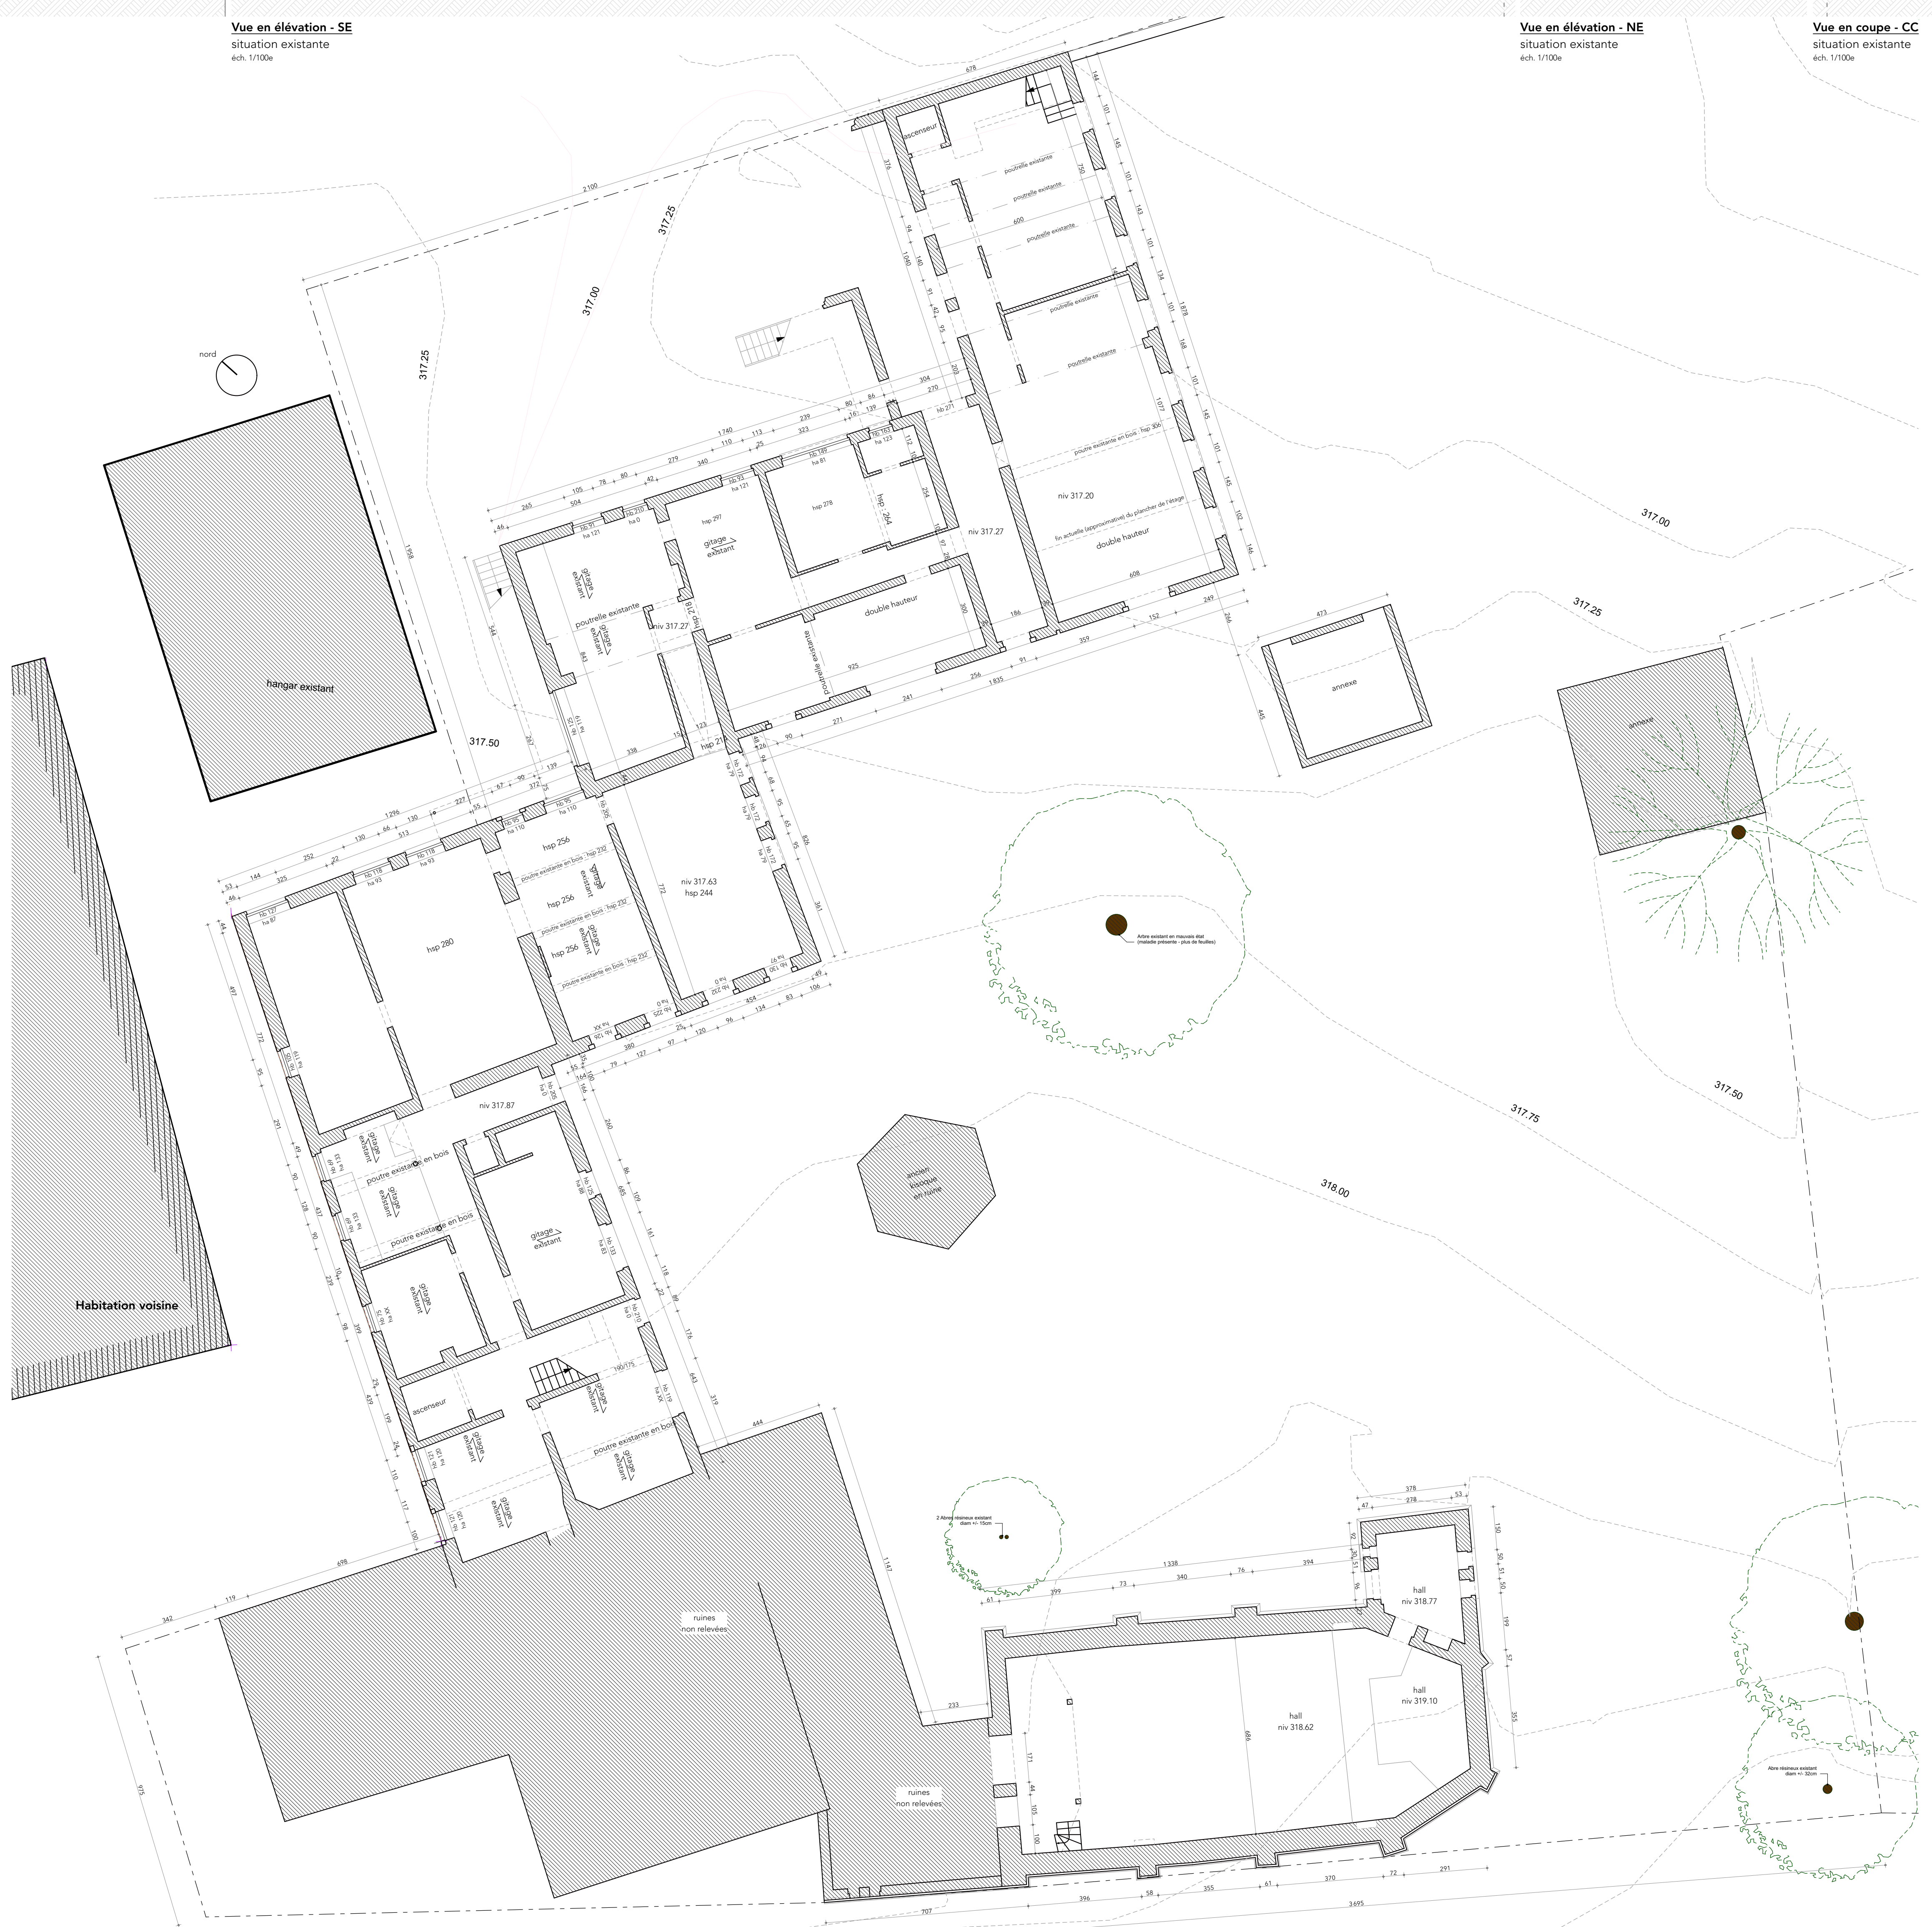

Vue en plan du rez-de-chaussée
situation existante
éch. 1/100e

Légende des matériaux - EXISTANTS

Numéro	Type	Matériaux	Teinte
Ⓐ	Parement principal	Maçonnerie en briques de terre cuite	ton rouge-brun (résidu de peinture blanche par endroit)
Ⓑ	Parement	Pierres (moellons)	ton gris-beige
Ⓒ	Bardage	Ardoises	ton gris
Ⓓ	Menuiseries extérieures	Bois	ton naturel
Ⓔ	Seuils	Pierre calcaire	ton gris clair
Ⓕ	Gouttière	Zinc naturel	ton gris clair
Ⓖ	Couverture	Tuiles plates en terre cuite	ton gris anthracite
Ⓗ	Couverture	Ardoises	ton gris

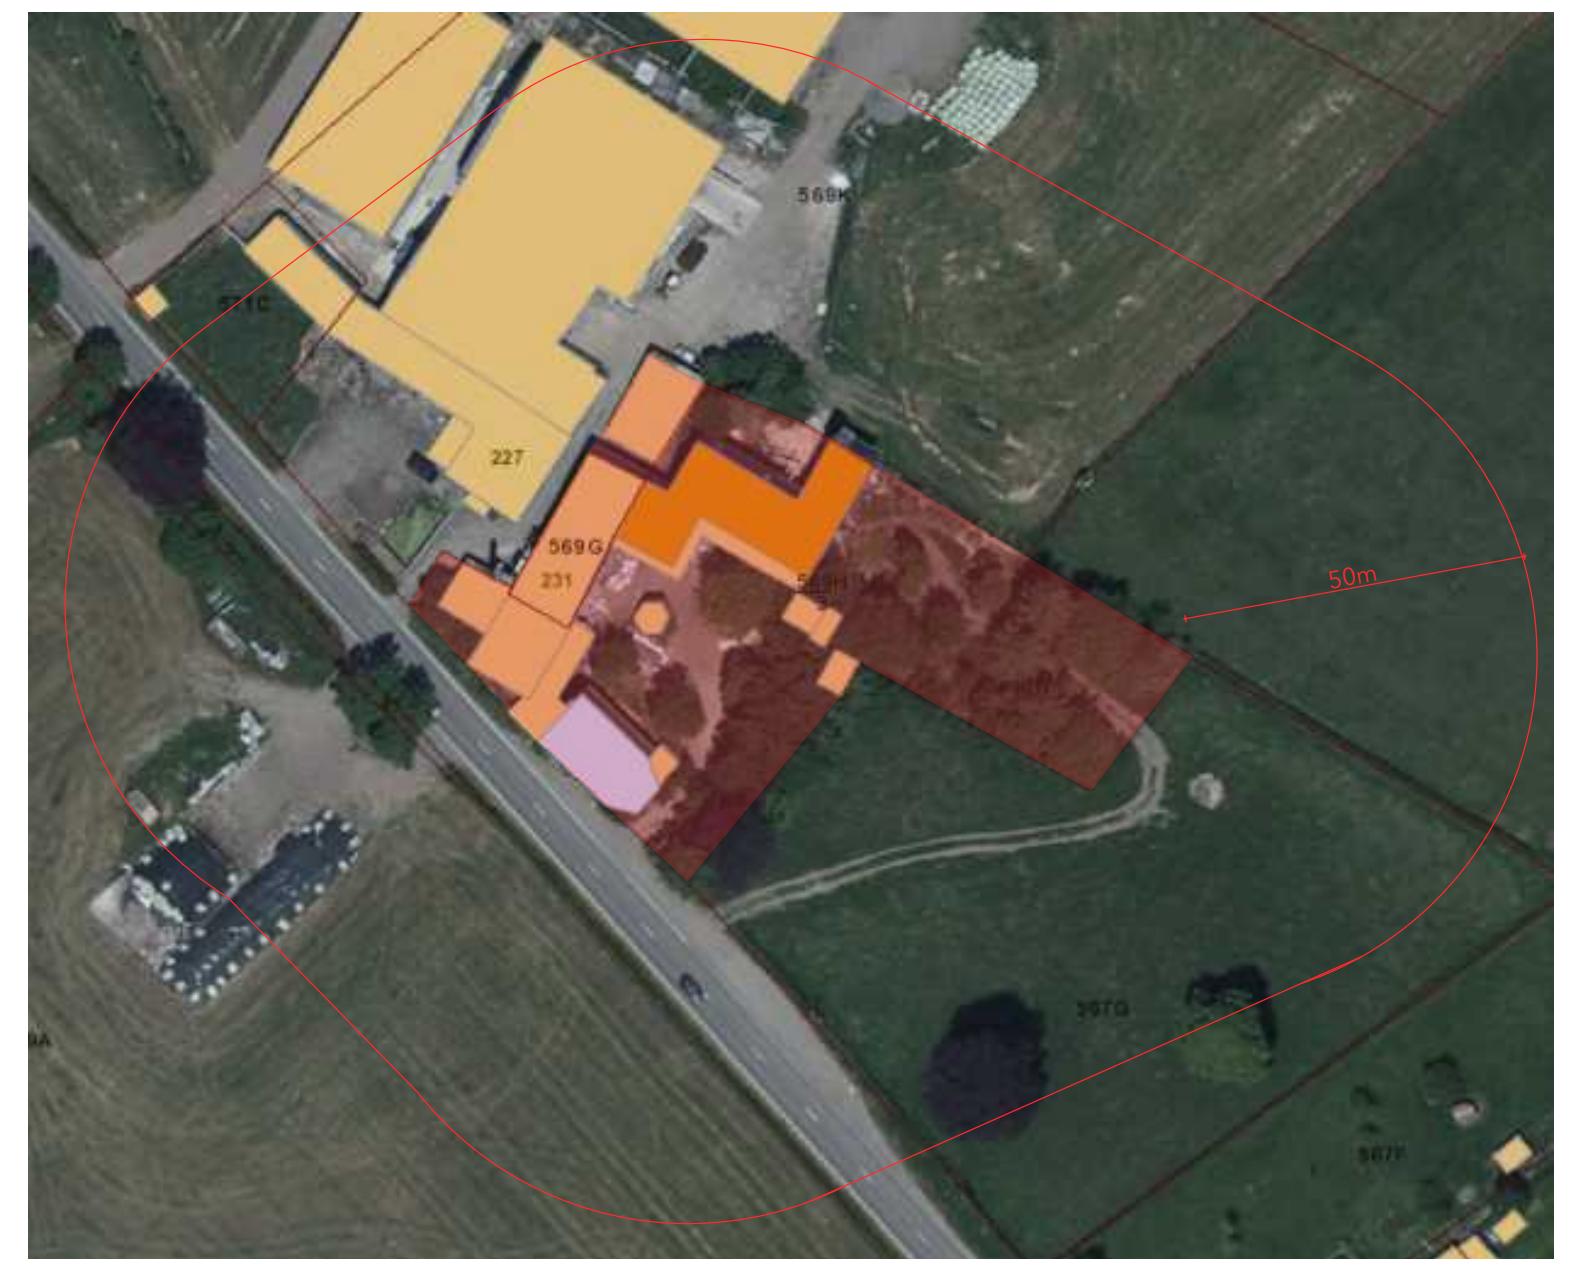

Contexte urbanistique
situation existante

n°227: maison rez+1+ toiture à versants
569 K : hangars agricoles volumes rez+toitures à versants

Projet
Transformation d'une chapelle à l'abandon et de l'ancien couvent de Gensterbloem en 7 logements

Adresse
Rue du Mémorial Américain 231, à 4852 Plombières
Cadastre : Plombières 4DIV / Section B / 569H3, 569G, 567G et une partie de la 569K

Administration
Urbanisme de Plombières

Maître de l'ouvrage
(représentée par

Auteur de projet
YA Architecture SRL

Evolution du dossier

Phase	Version	Date	Explicatif	Réalisé par
		19/06/2023	1ère réunion de Patrimoine (sans la présence de l'auteur de projet) sur site	
AP		12/02/2024	Présentation de l'AP3 au Patrimoine et au SPW, au SPW à Liège	Y - A
PU	**A**	**14/03/2025**	**Tracé de la demande de permis d'urbanisme**	**YM**

Légende des matériaux utilisés dans les plans et coupes

▨	Maçonnerie existante	🟥	Bloc de béton	▨	Isolant	▨	Parement en brique
▨	Terrain	▨	Empierrement	🟥	Béton armé	🟥	Chape et finition sol

Contenu de la feuille	N° de Dossier	Maître de l'ouvrage
situation existante	**2336**	**M2B**

Feuille n°	Version	Phase	Date	Echelle	Réalisé par
1/3	**A**	**PU**	**14/03/25**	**voir plans**	**YM**

YA Architecture SRL

Ce document est la propriété de YA Architecture SRL. Toute reproduction ou communication à des tiers en est interdite sans son autorisation préalable