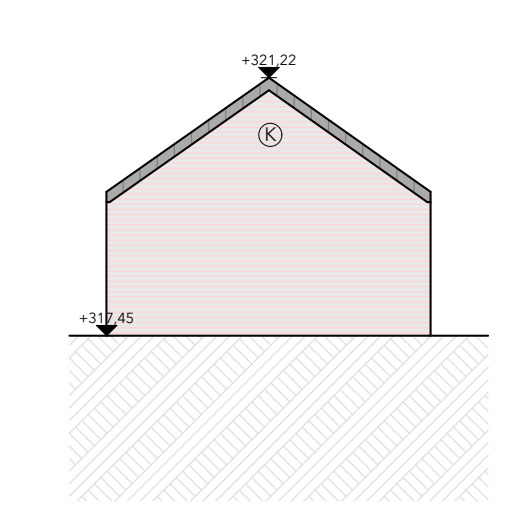

Vue en élévation - façade arrière
situation projetée - annexe rénovée LOG 6
éch. 1/100e

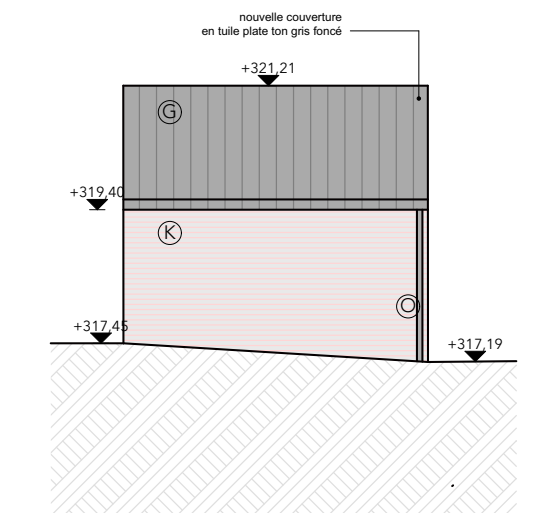

Vue en élévation - façade latérale gauche
situation projetée - annexe rénovée LOG 6
éch. 1/100e

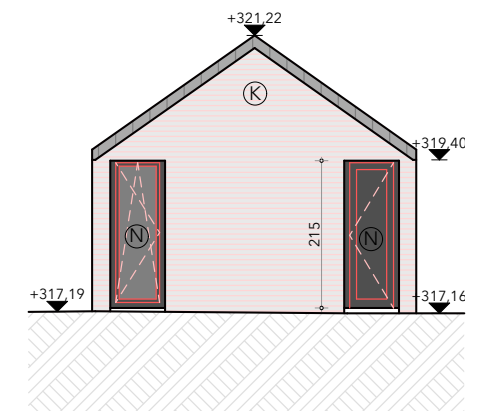

Vue en élévation - façade avant
situation projetée - annexe rénovée LOG 6
éch. 1/100e

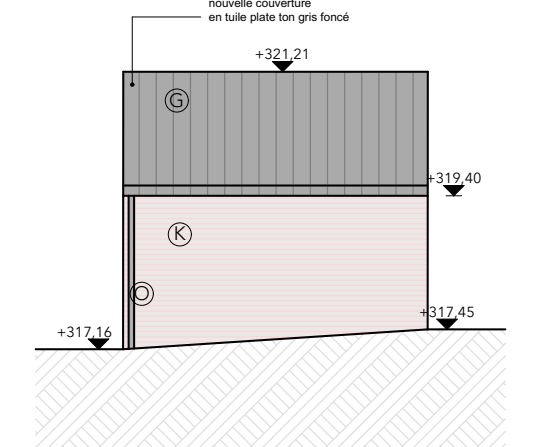

Vue en élévation - façade latérale droite
situation projetée - annexe rénovée LOG 6
éch. 1/100e

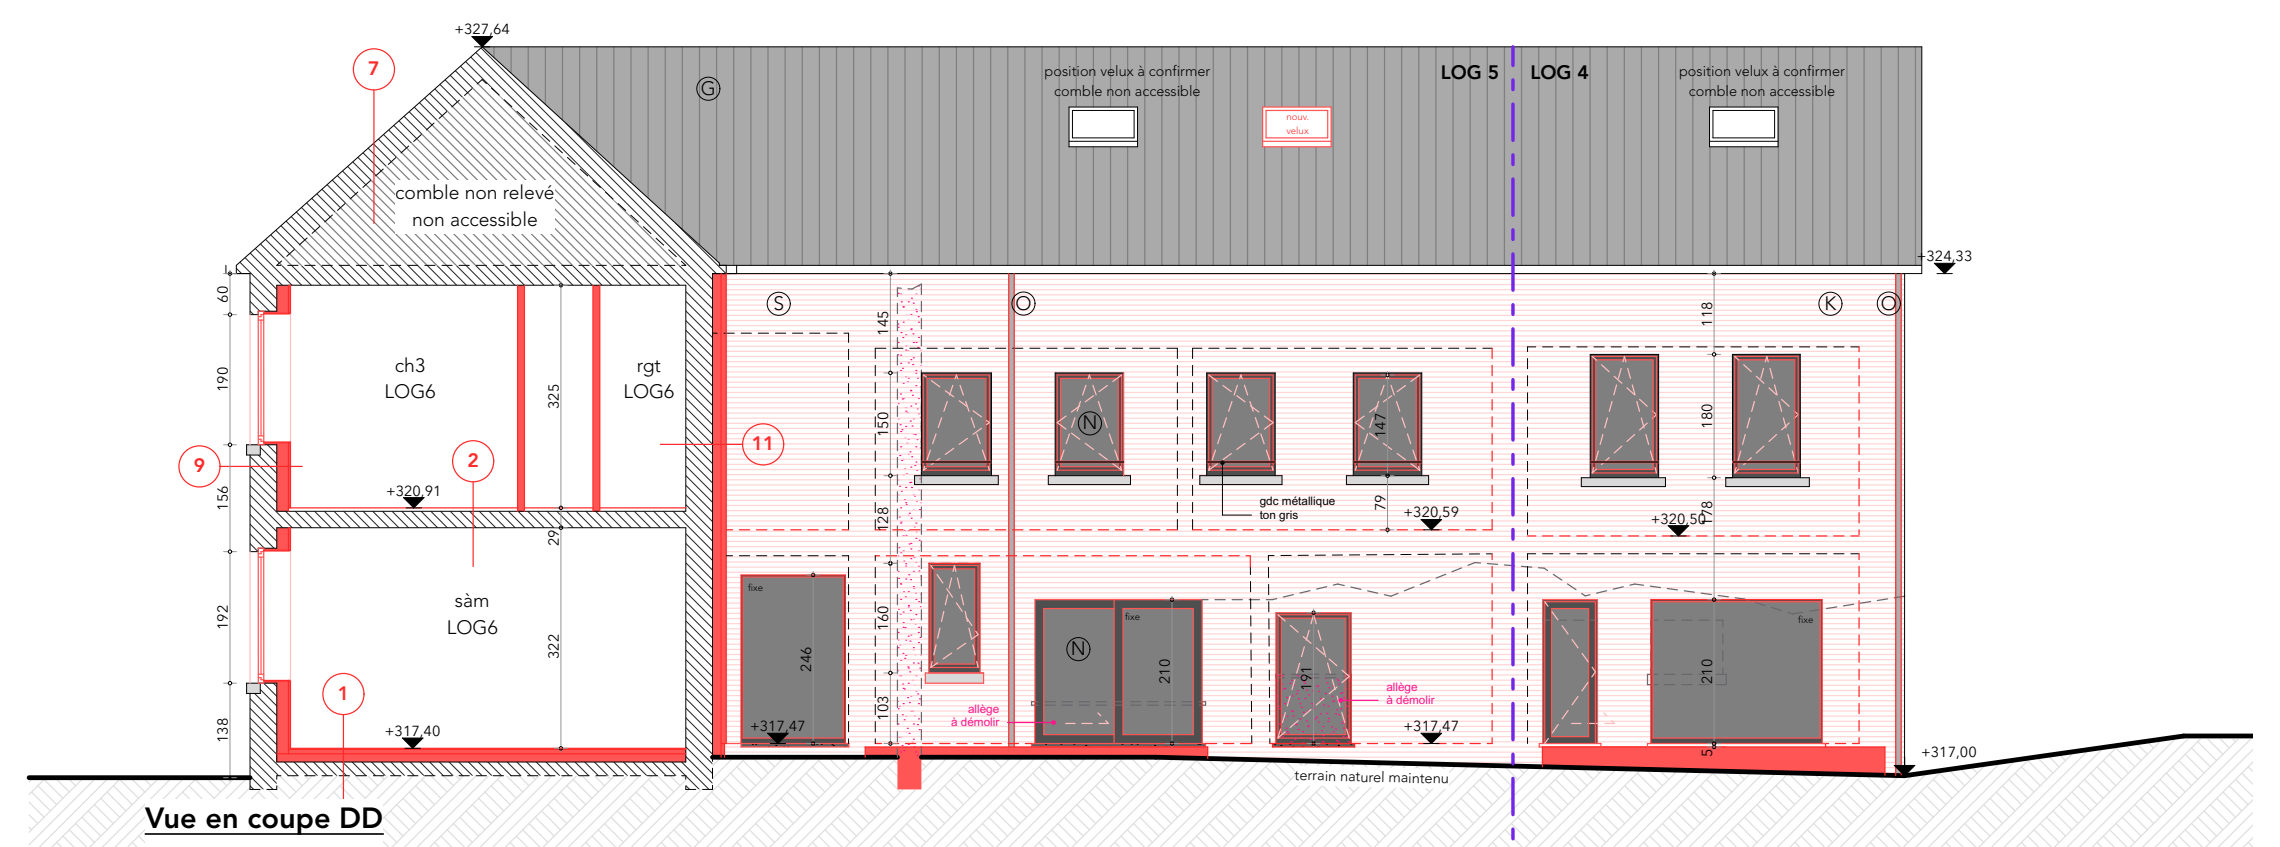

Vue en coupe DD
situation projetée
éch. 1/100e

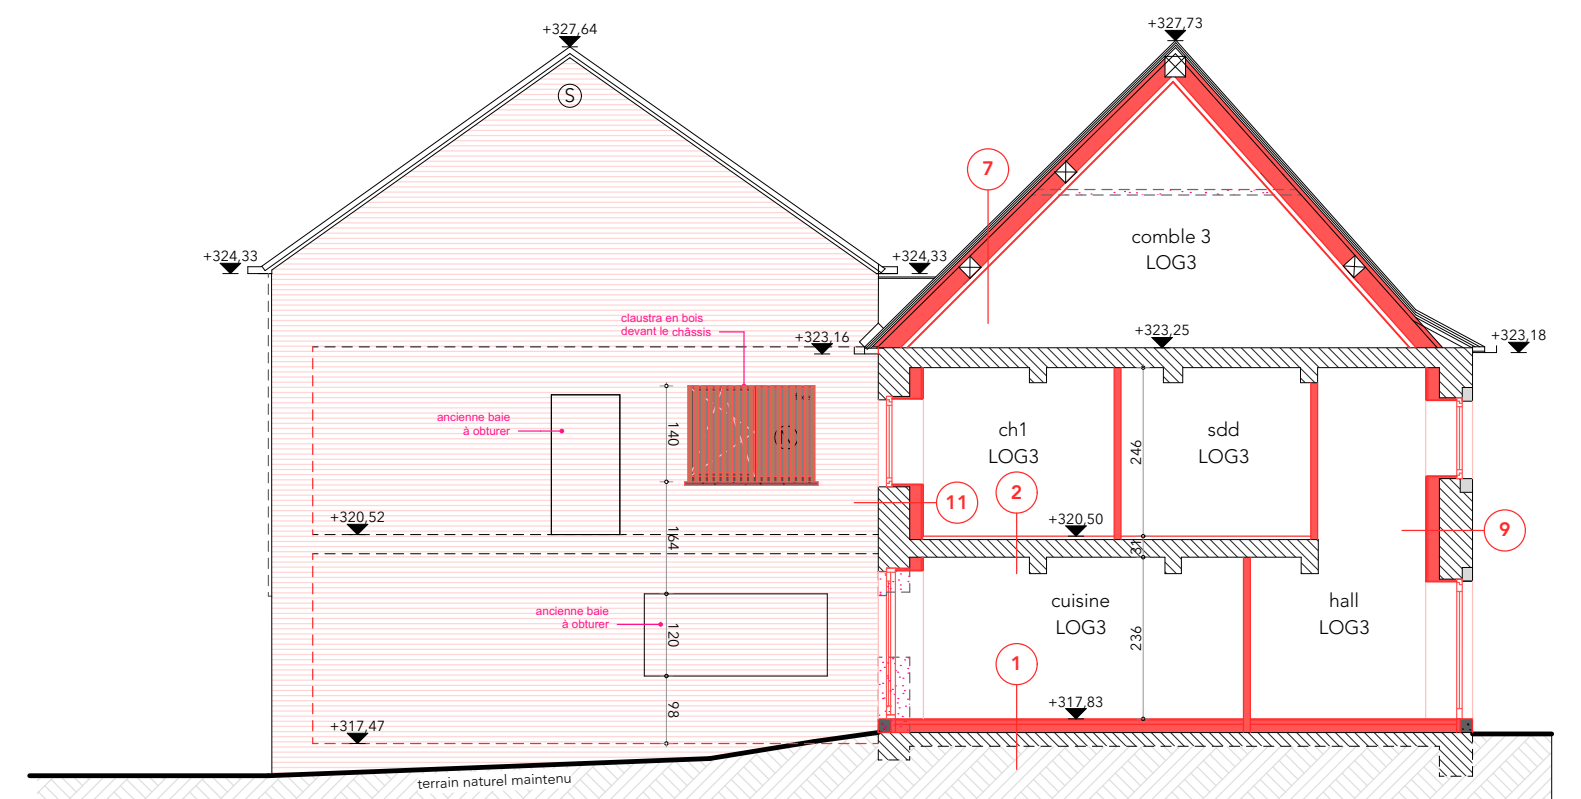

Vue en coupe EE
situation projetée
éch. 1/100e

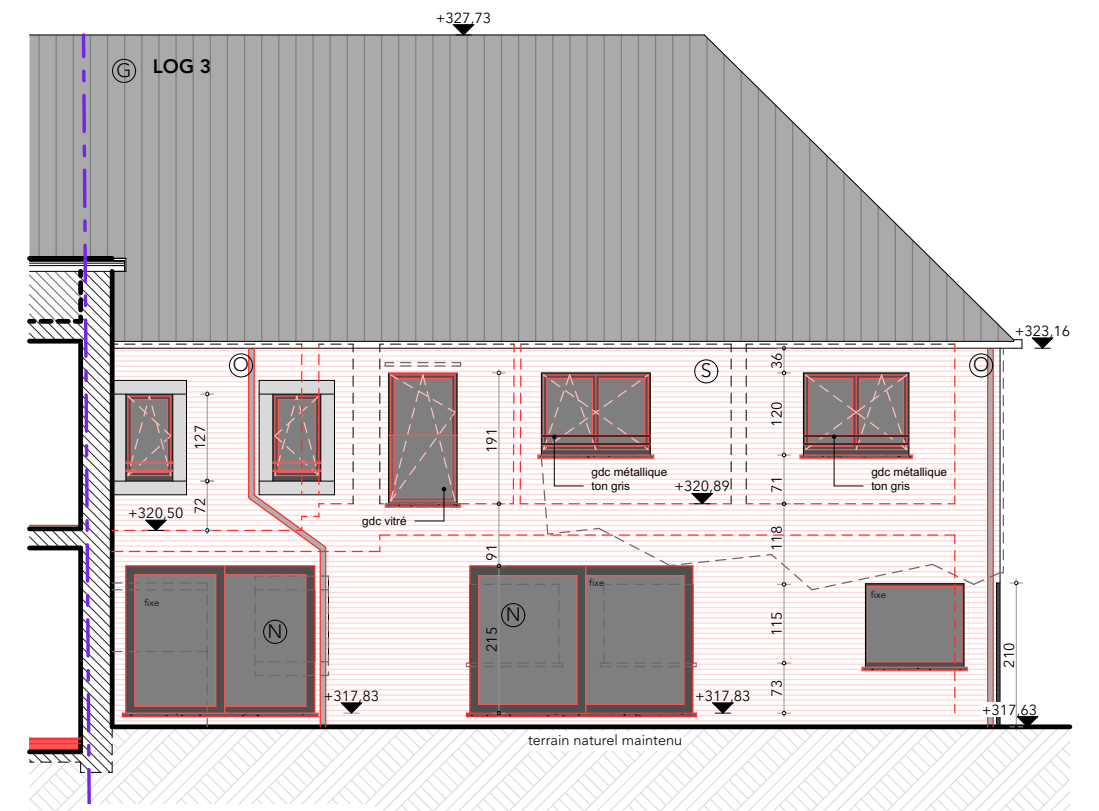

Vue en élévation - NE
situation projetée
éch. 1/100e

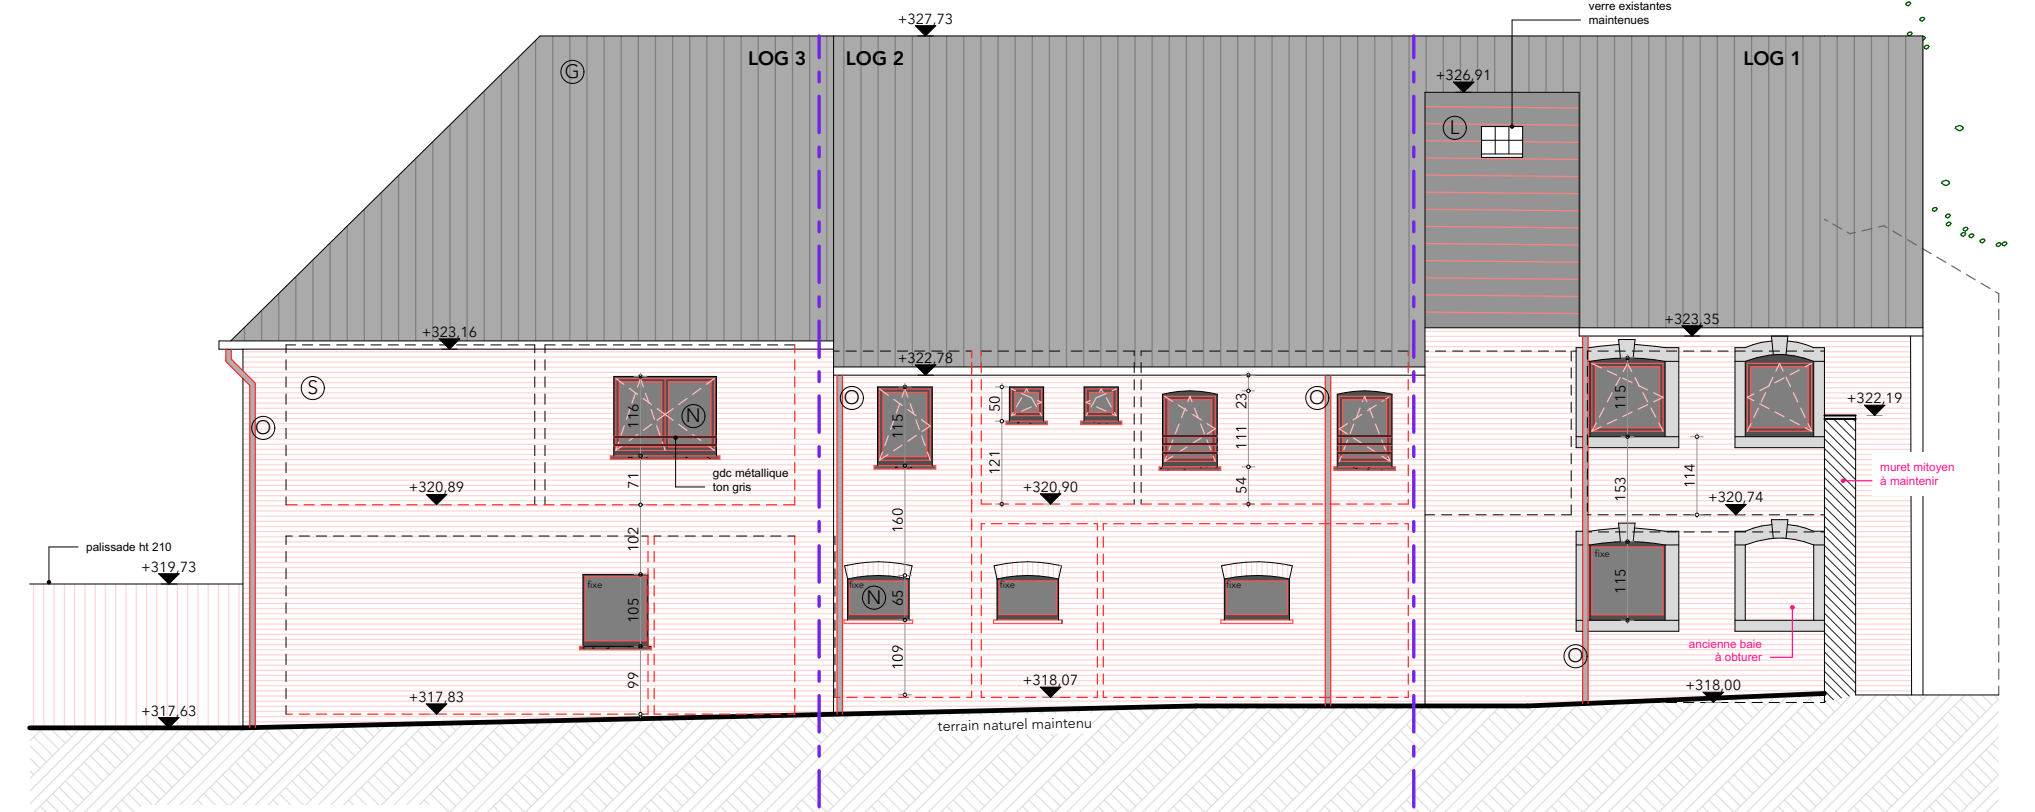

Vue en élévation - NO
situation projetée
éch. 1/100e

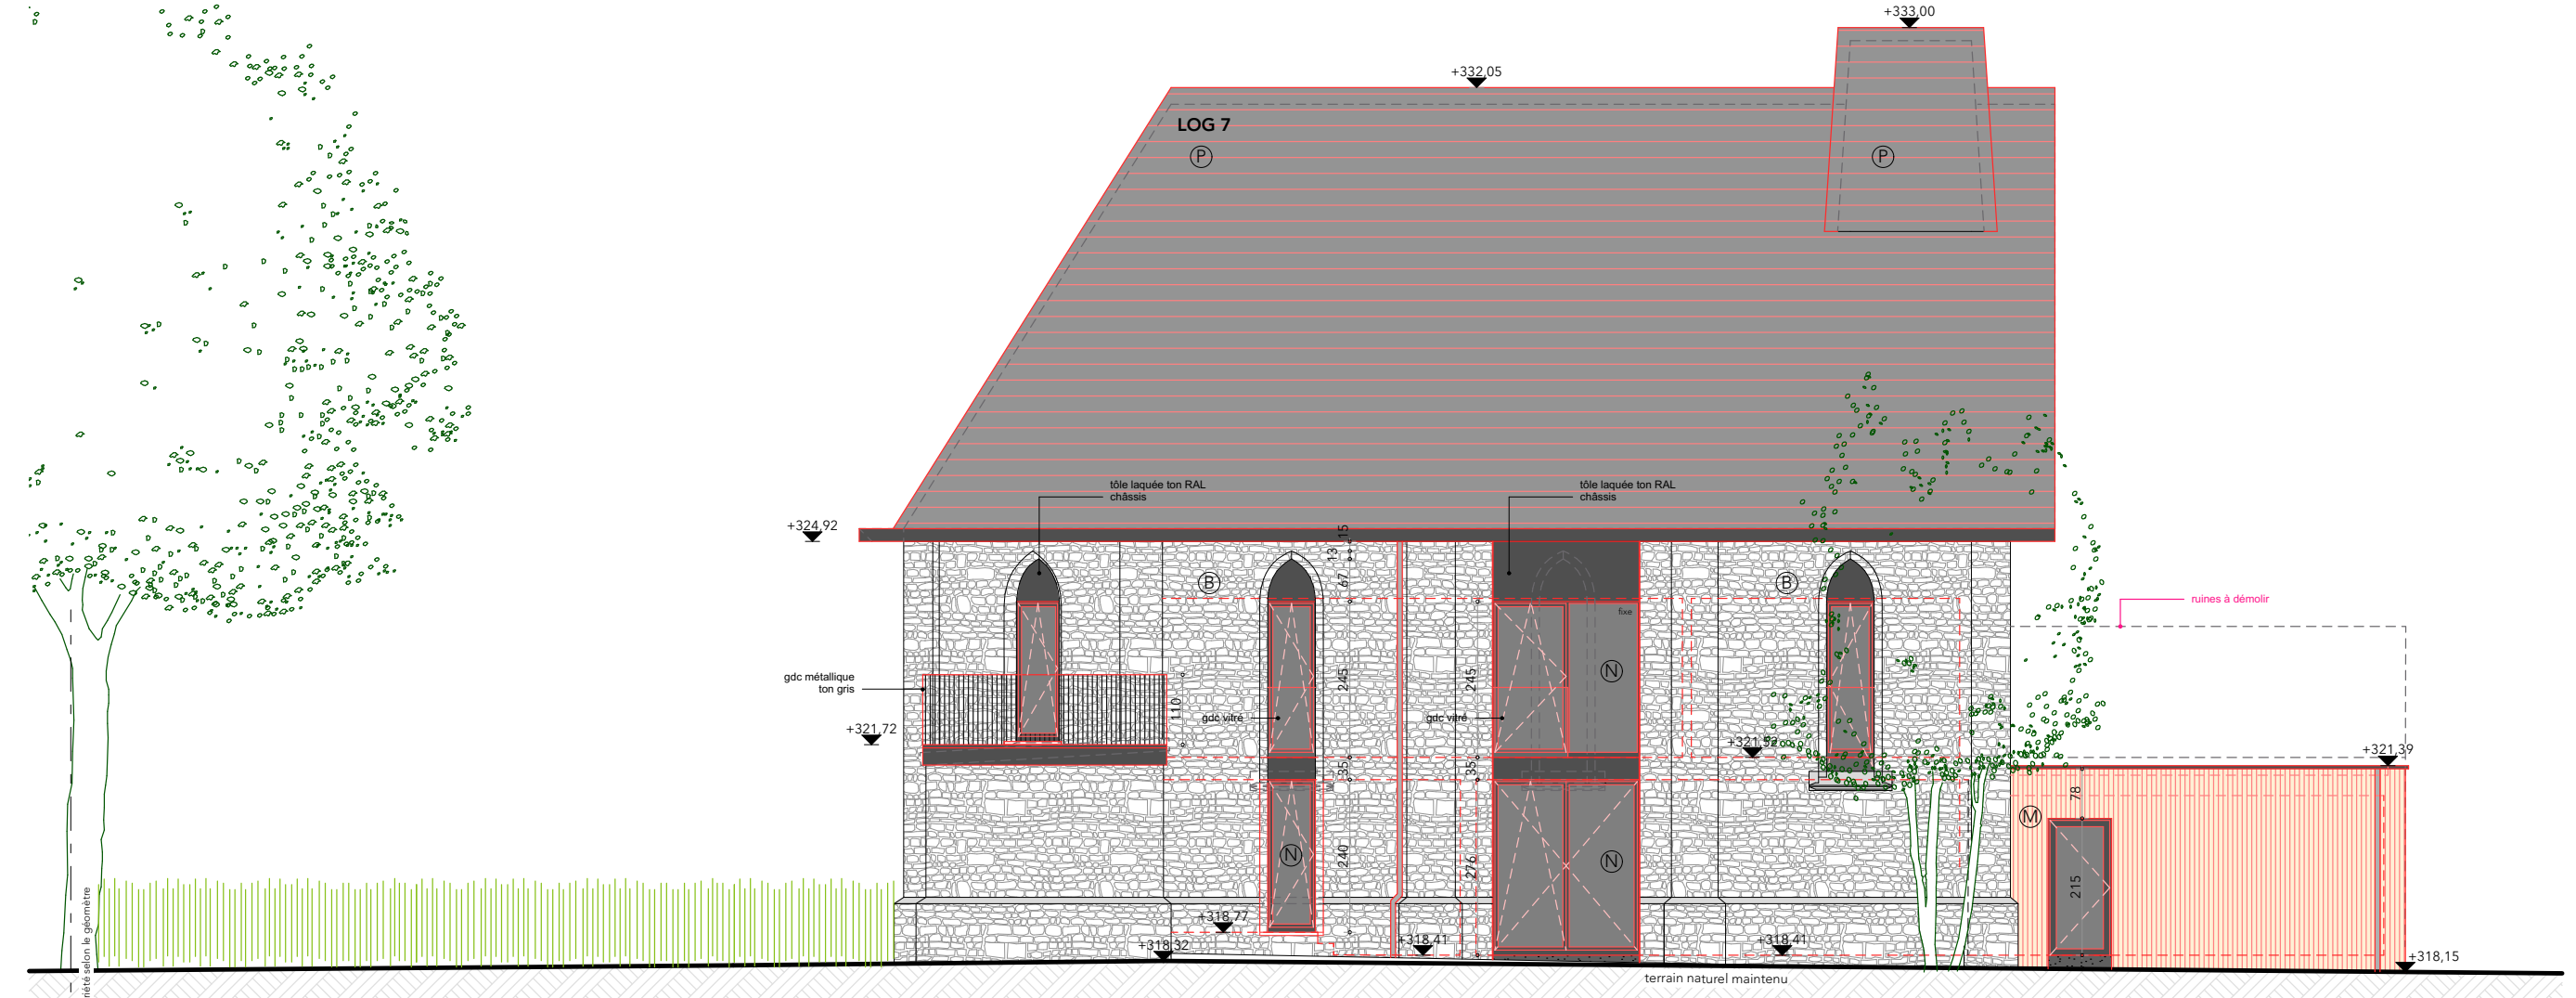

Vue en élévation - NE
situation projetée
éch. 1/100e

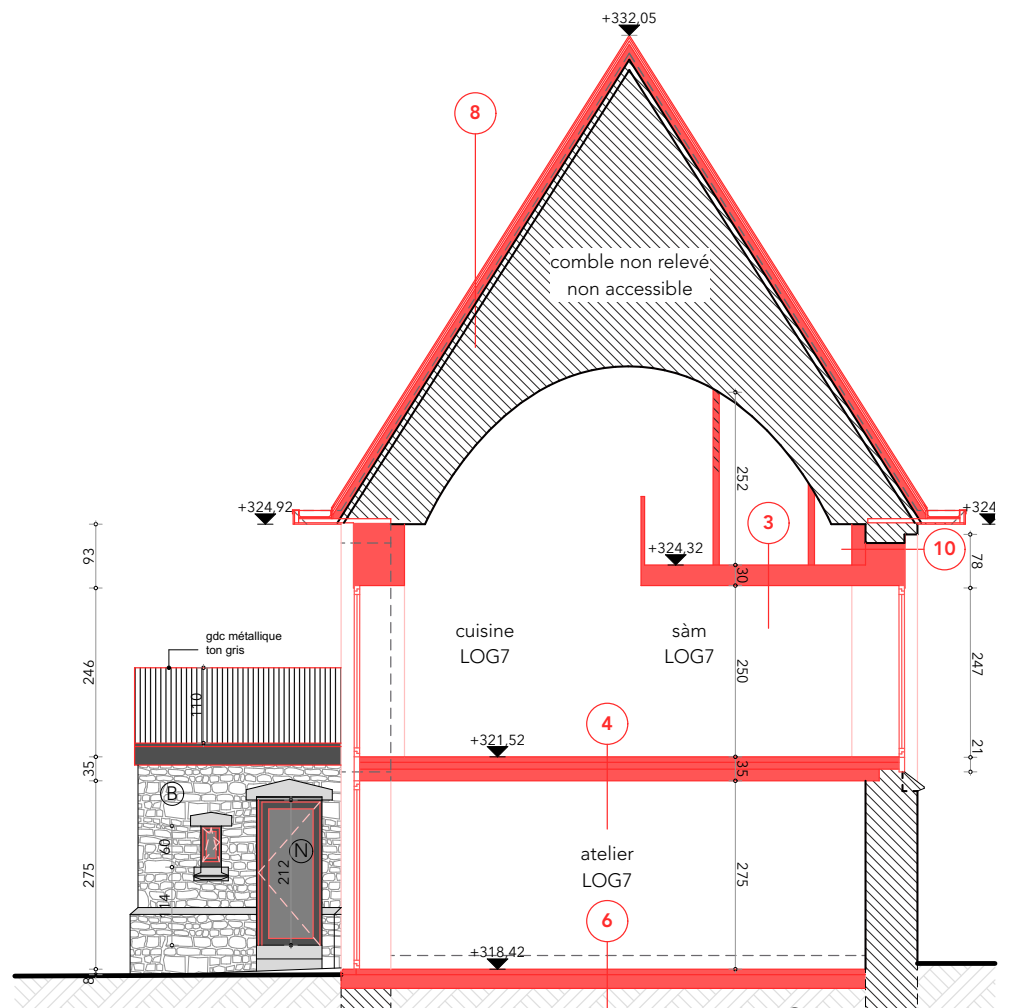

Vue en coupe FF
situation projetée
éch. 1/100e

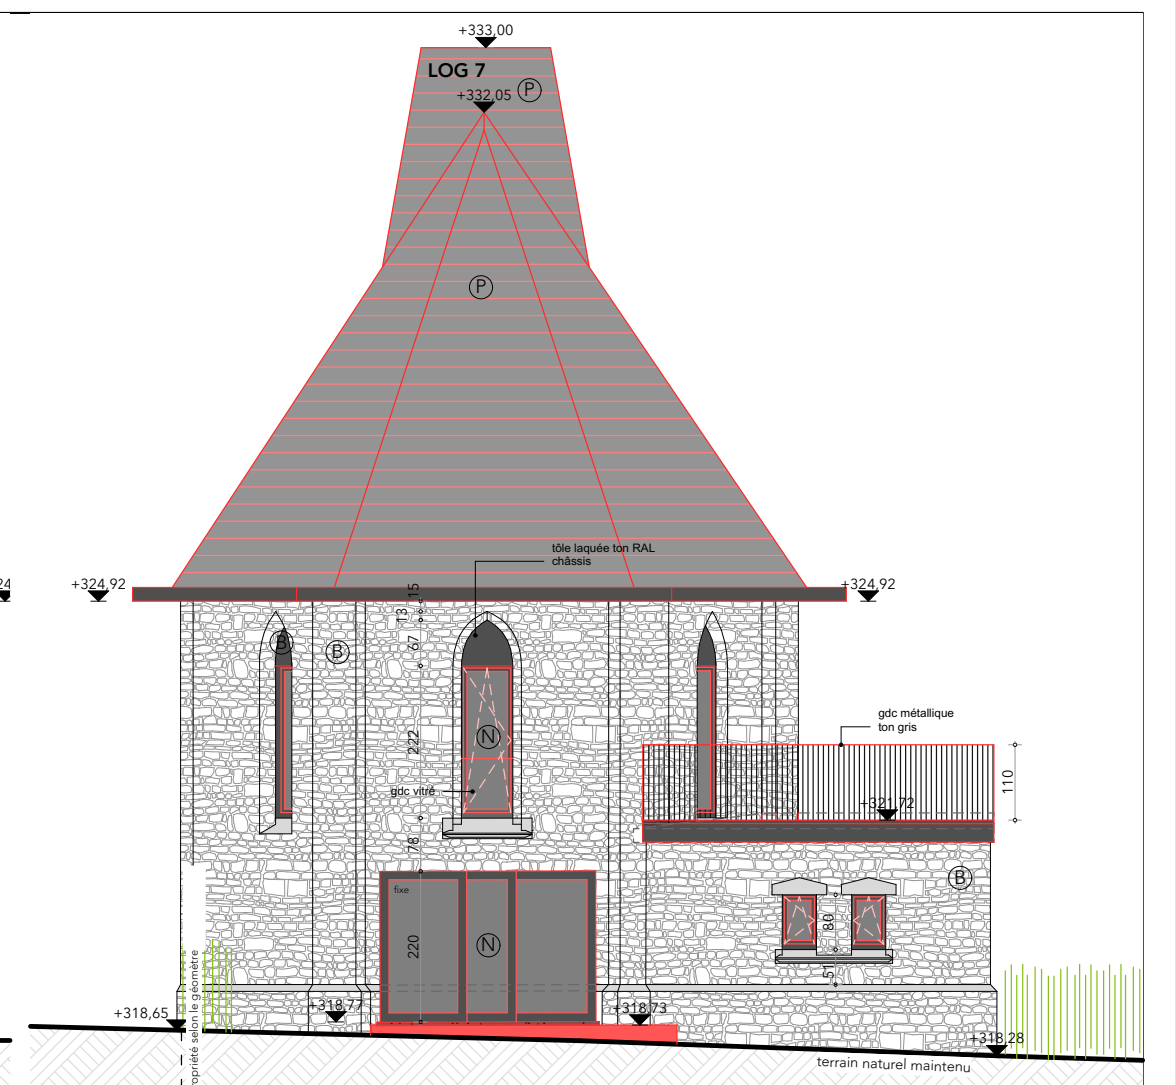

Vue en élévation - SE
situation projetée
éch. 1/100e

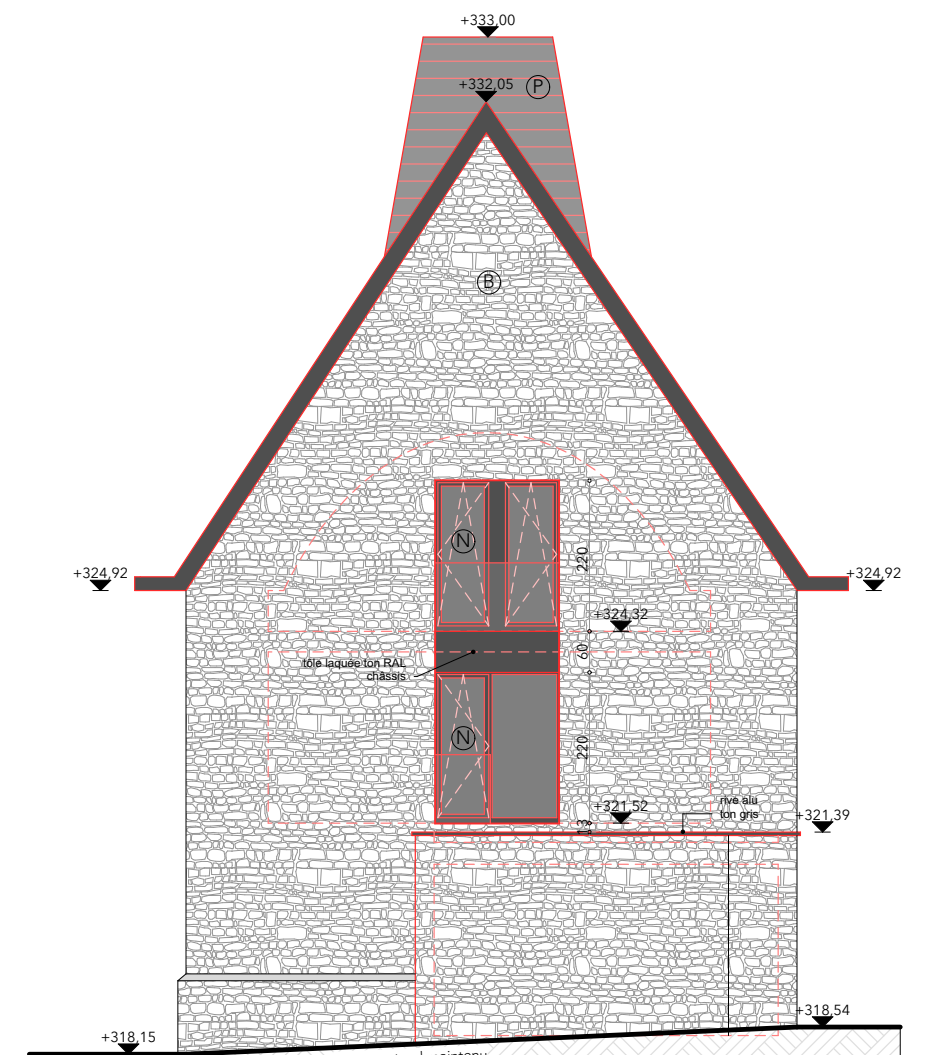

Vue en élévation - NO
situation projeté
éch. 1/100e

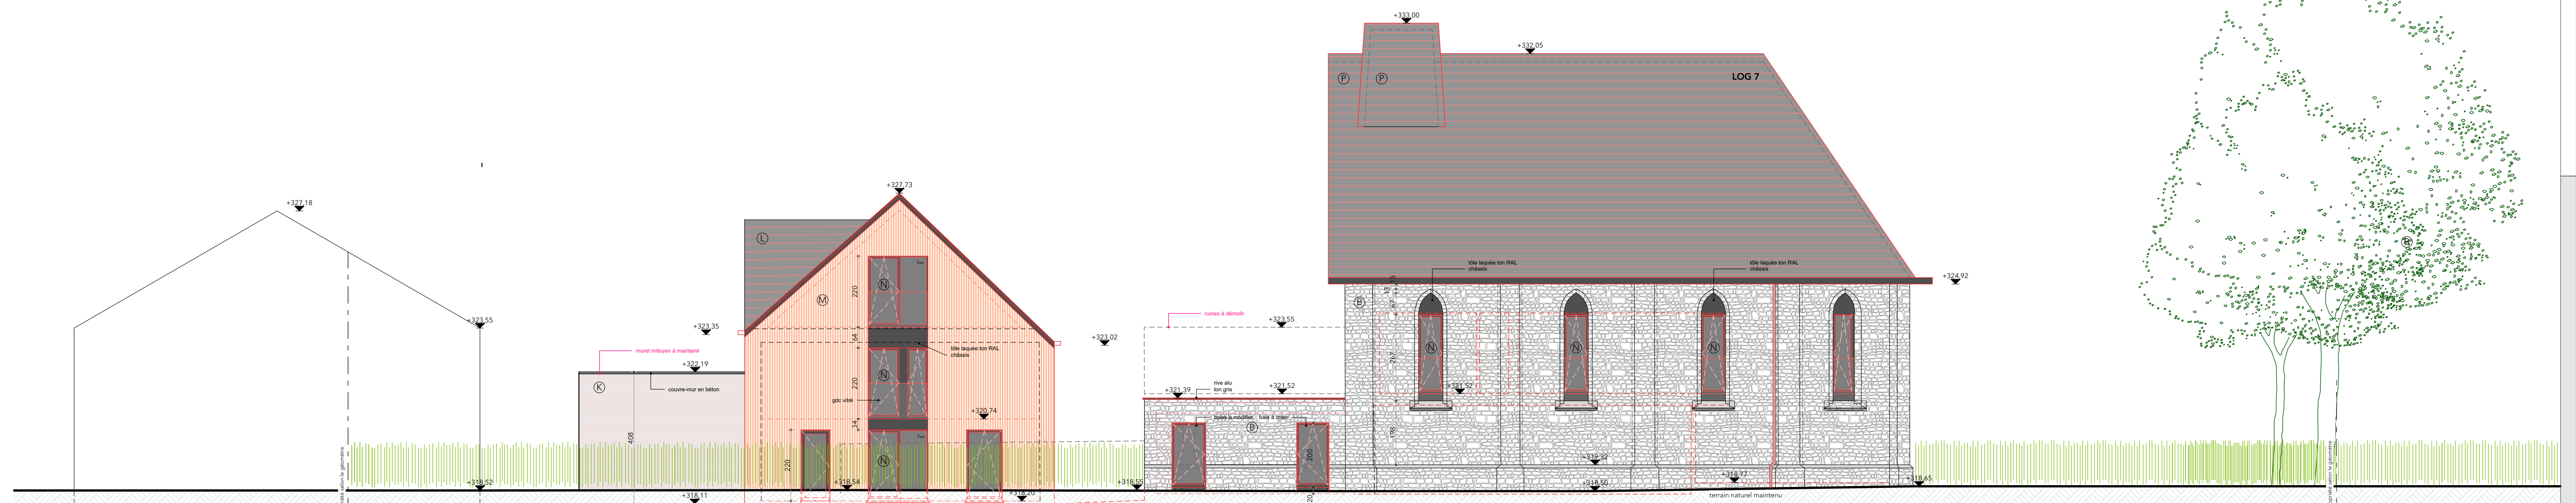

Vue en élévation - SO
situation projetée
éch. 1/100e

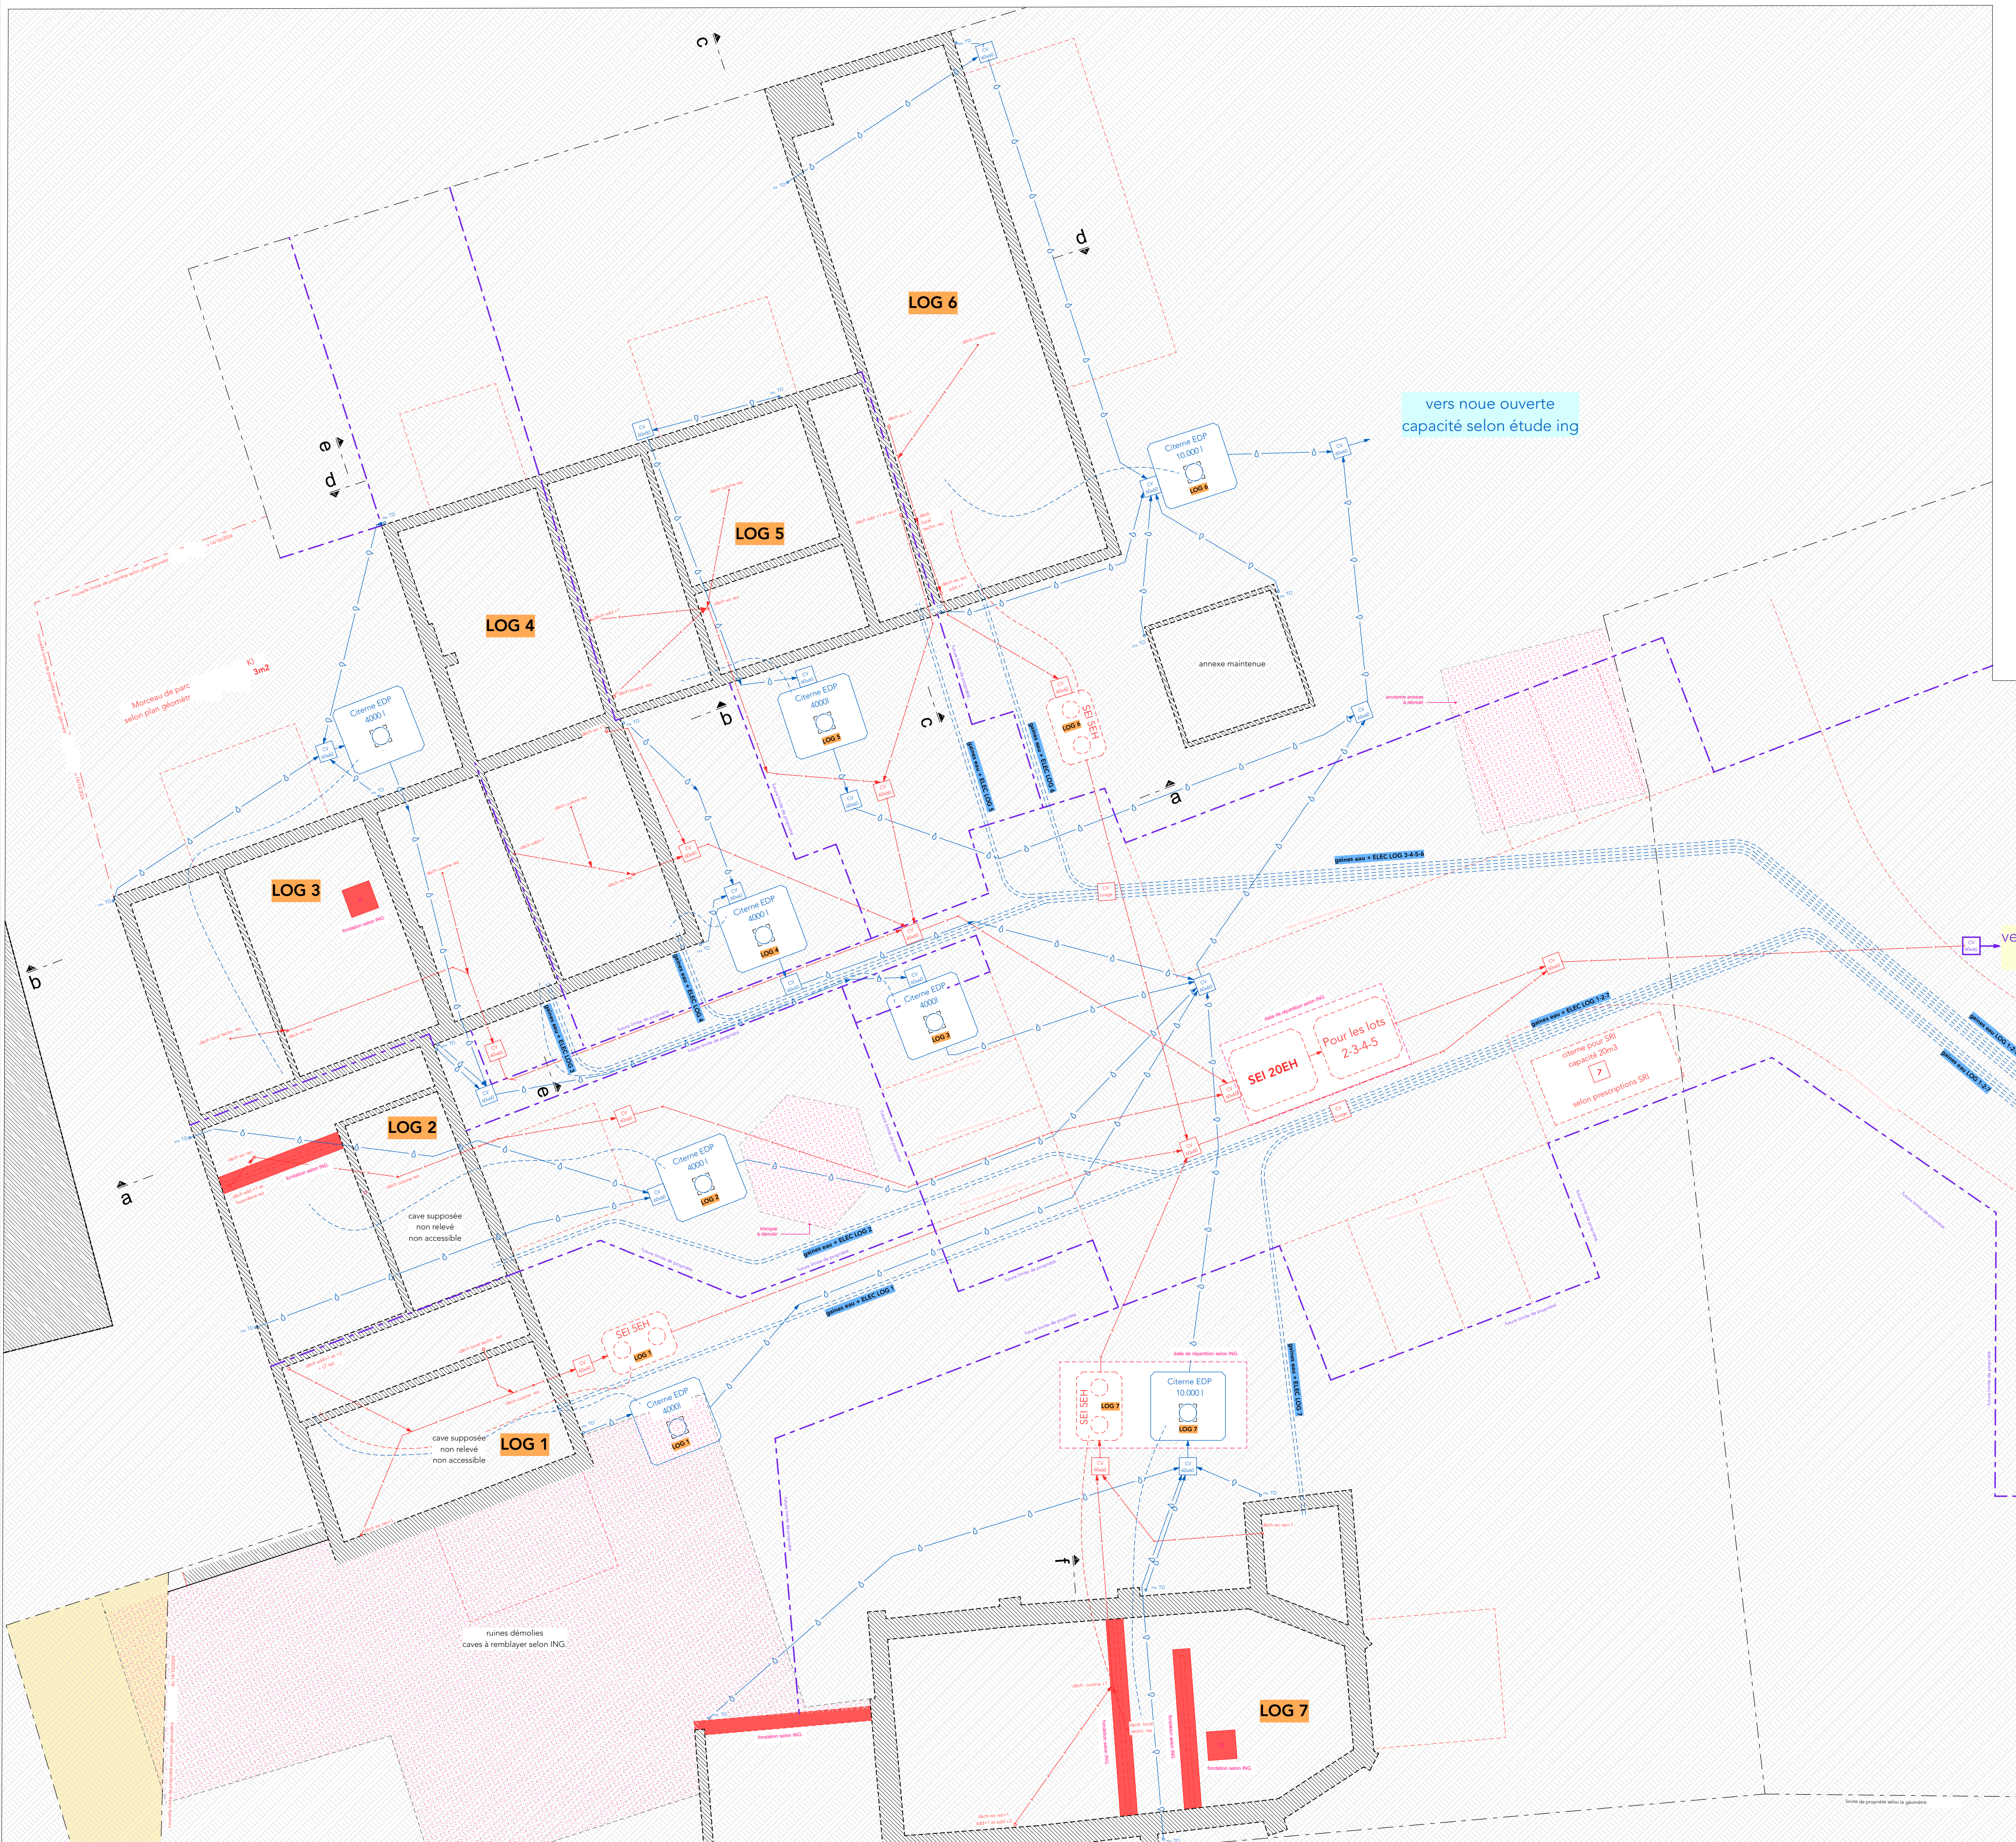
LOG 6
LOG 5
LOG 4
LOG 3
LOG 2
LOG 1
LOG 7
vers noue ouverte capacité selon étude ing
vers massif drainant selon ING.
prairie existante appartenant également au MO
SEI 20EH
annexe maintenue
nouvelle limite de propriété selon plan géomètre

Vue en plan de l'égouttage
situation projetée
éch. 1/100e

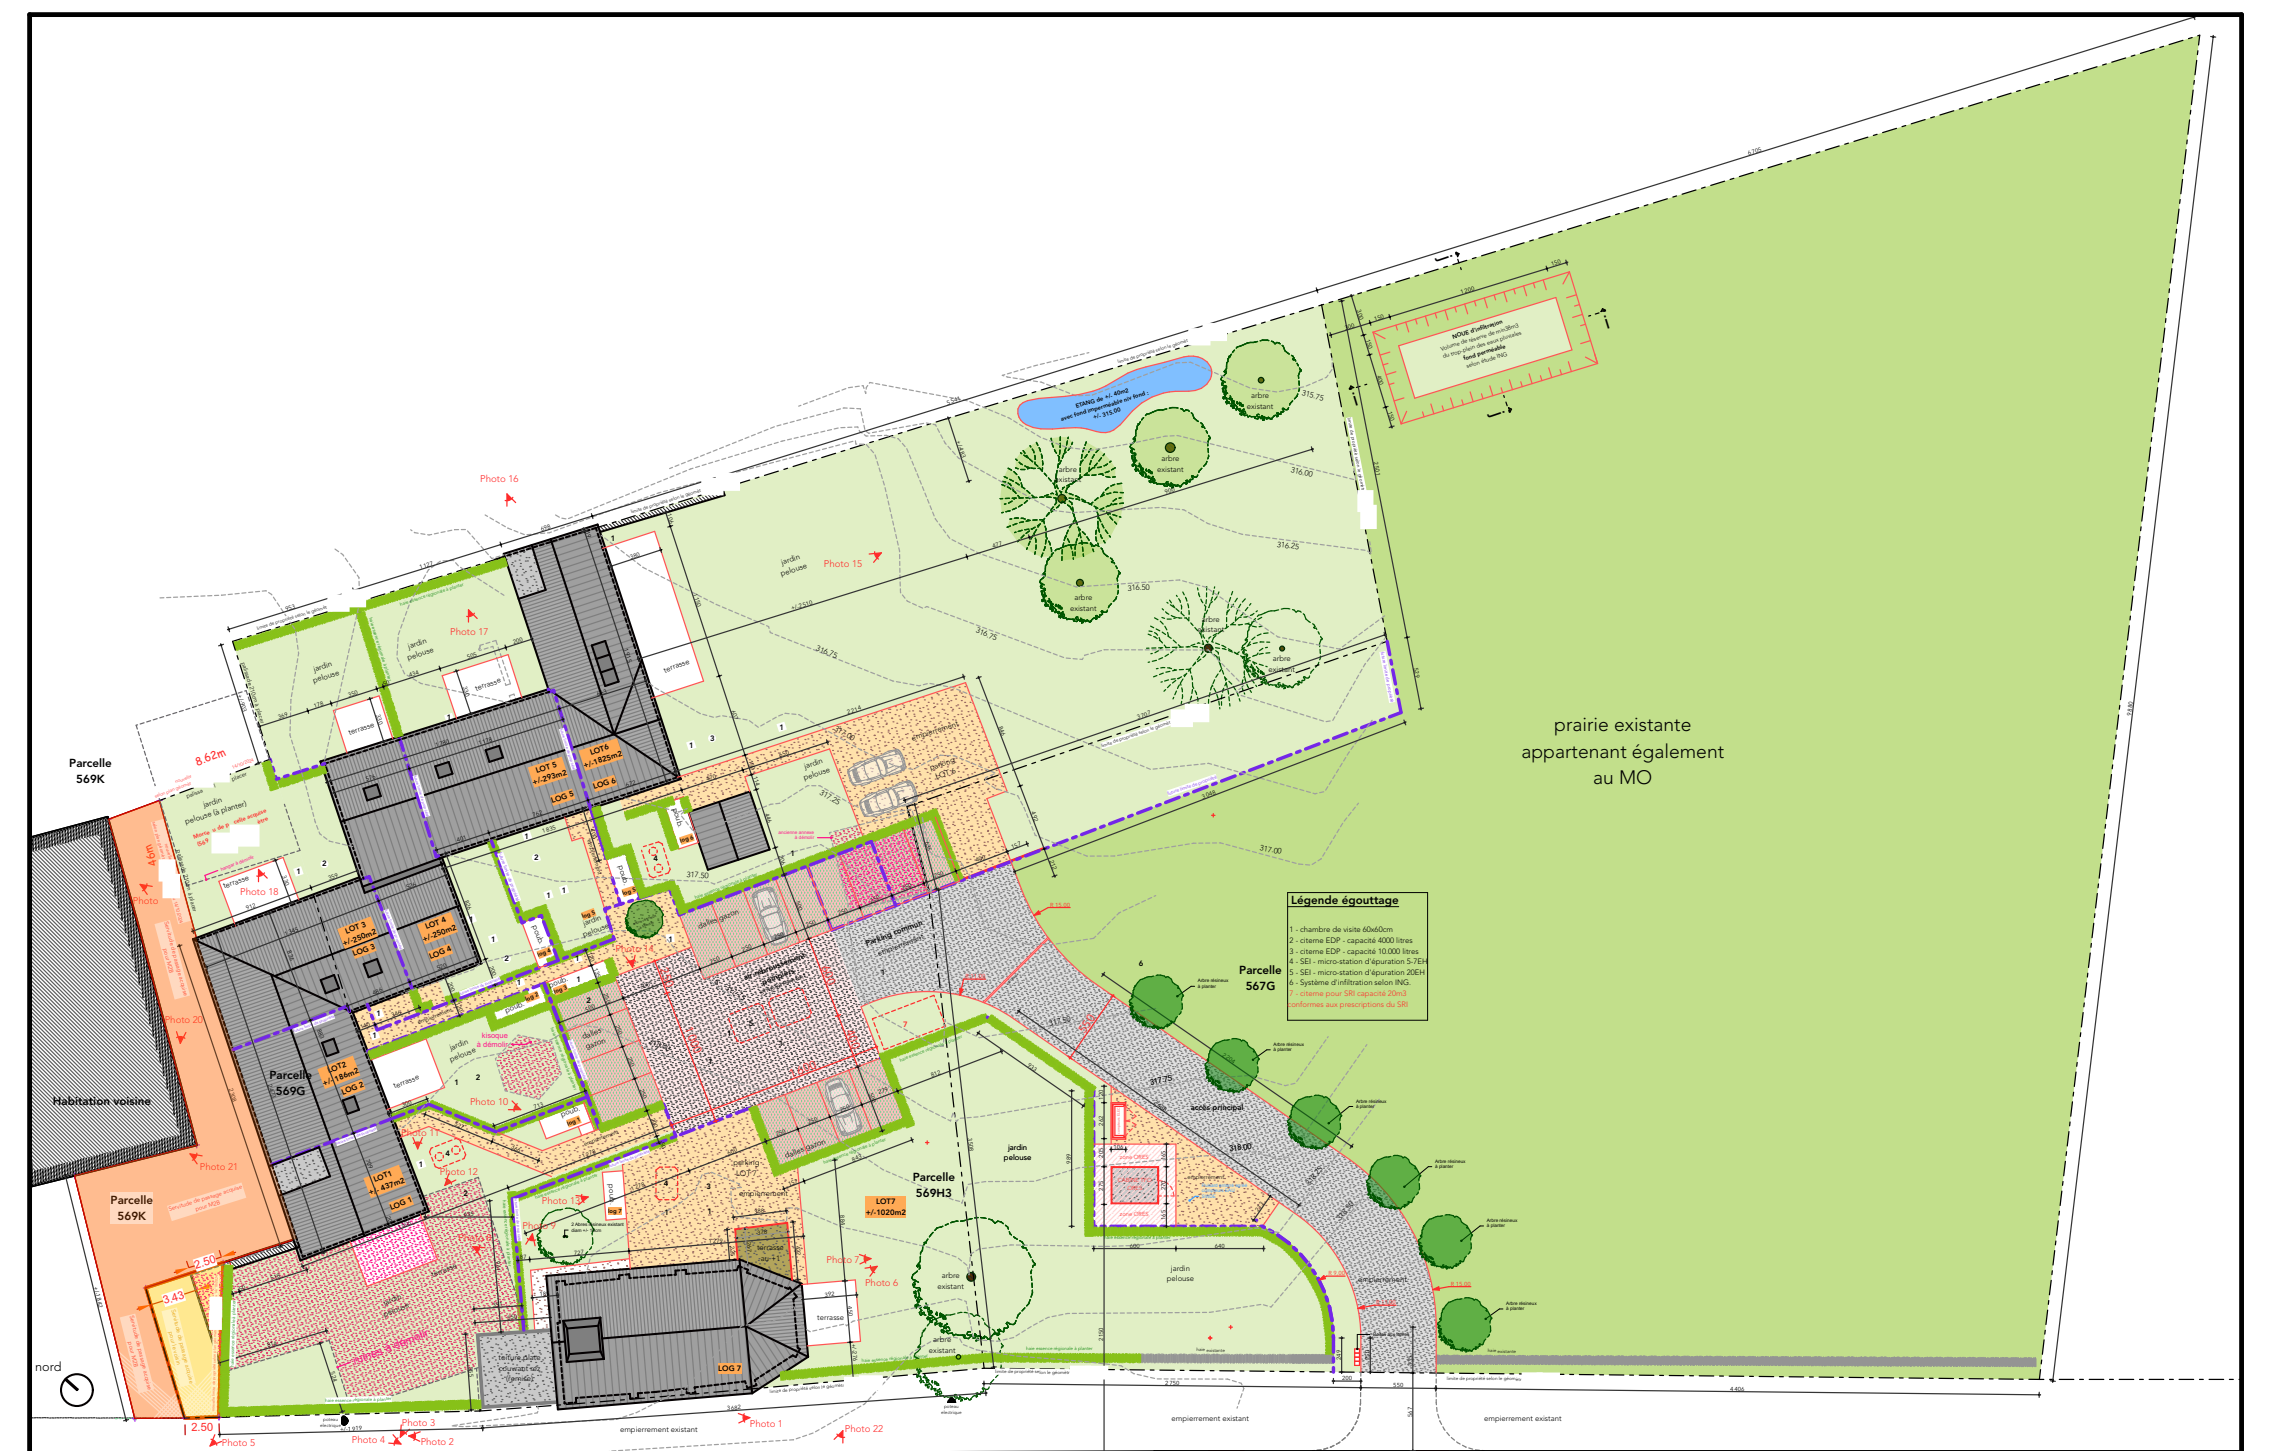

Vue en plan
situation projetée
éch. 1/500e

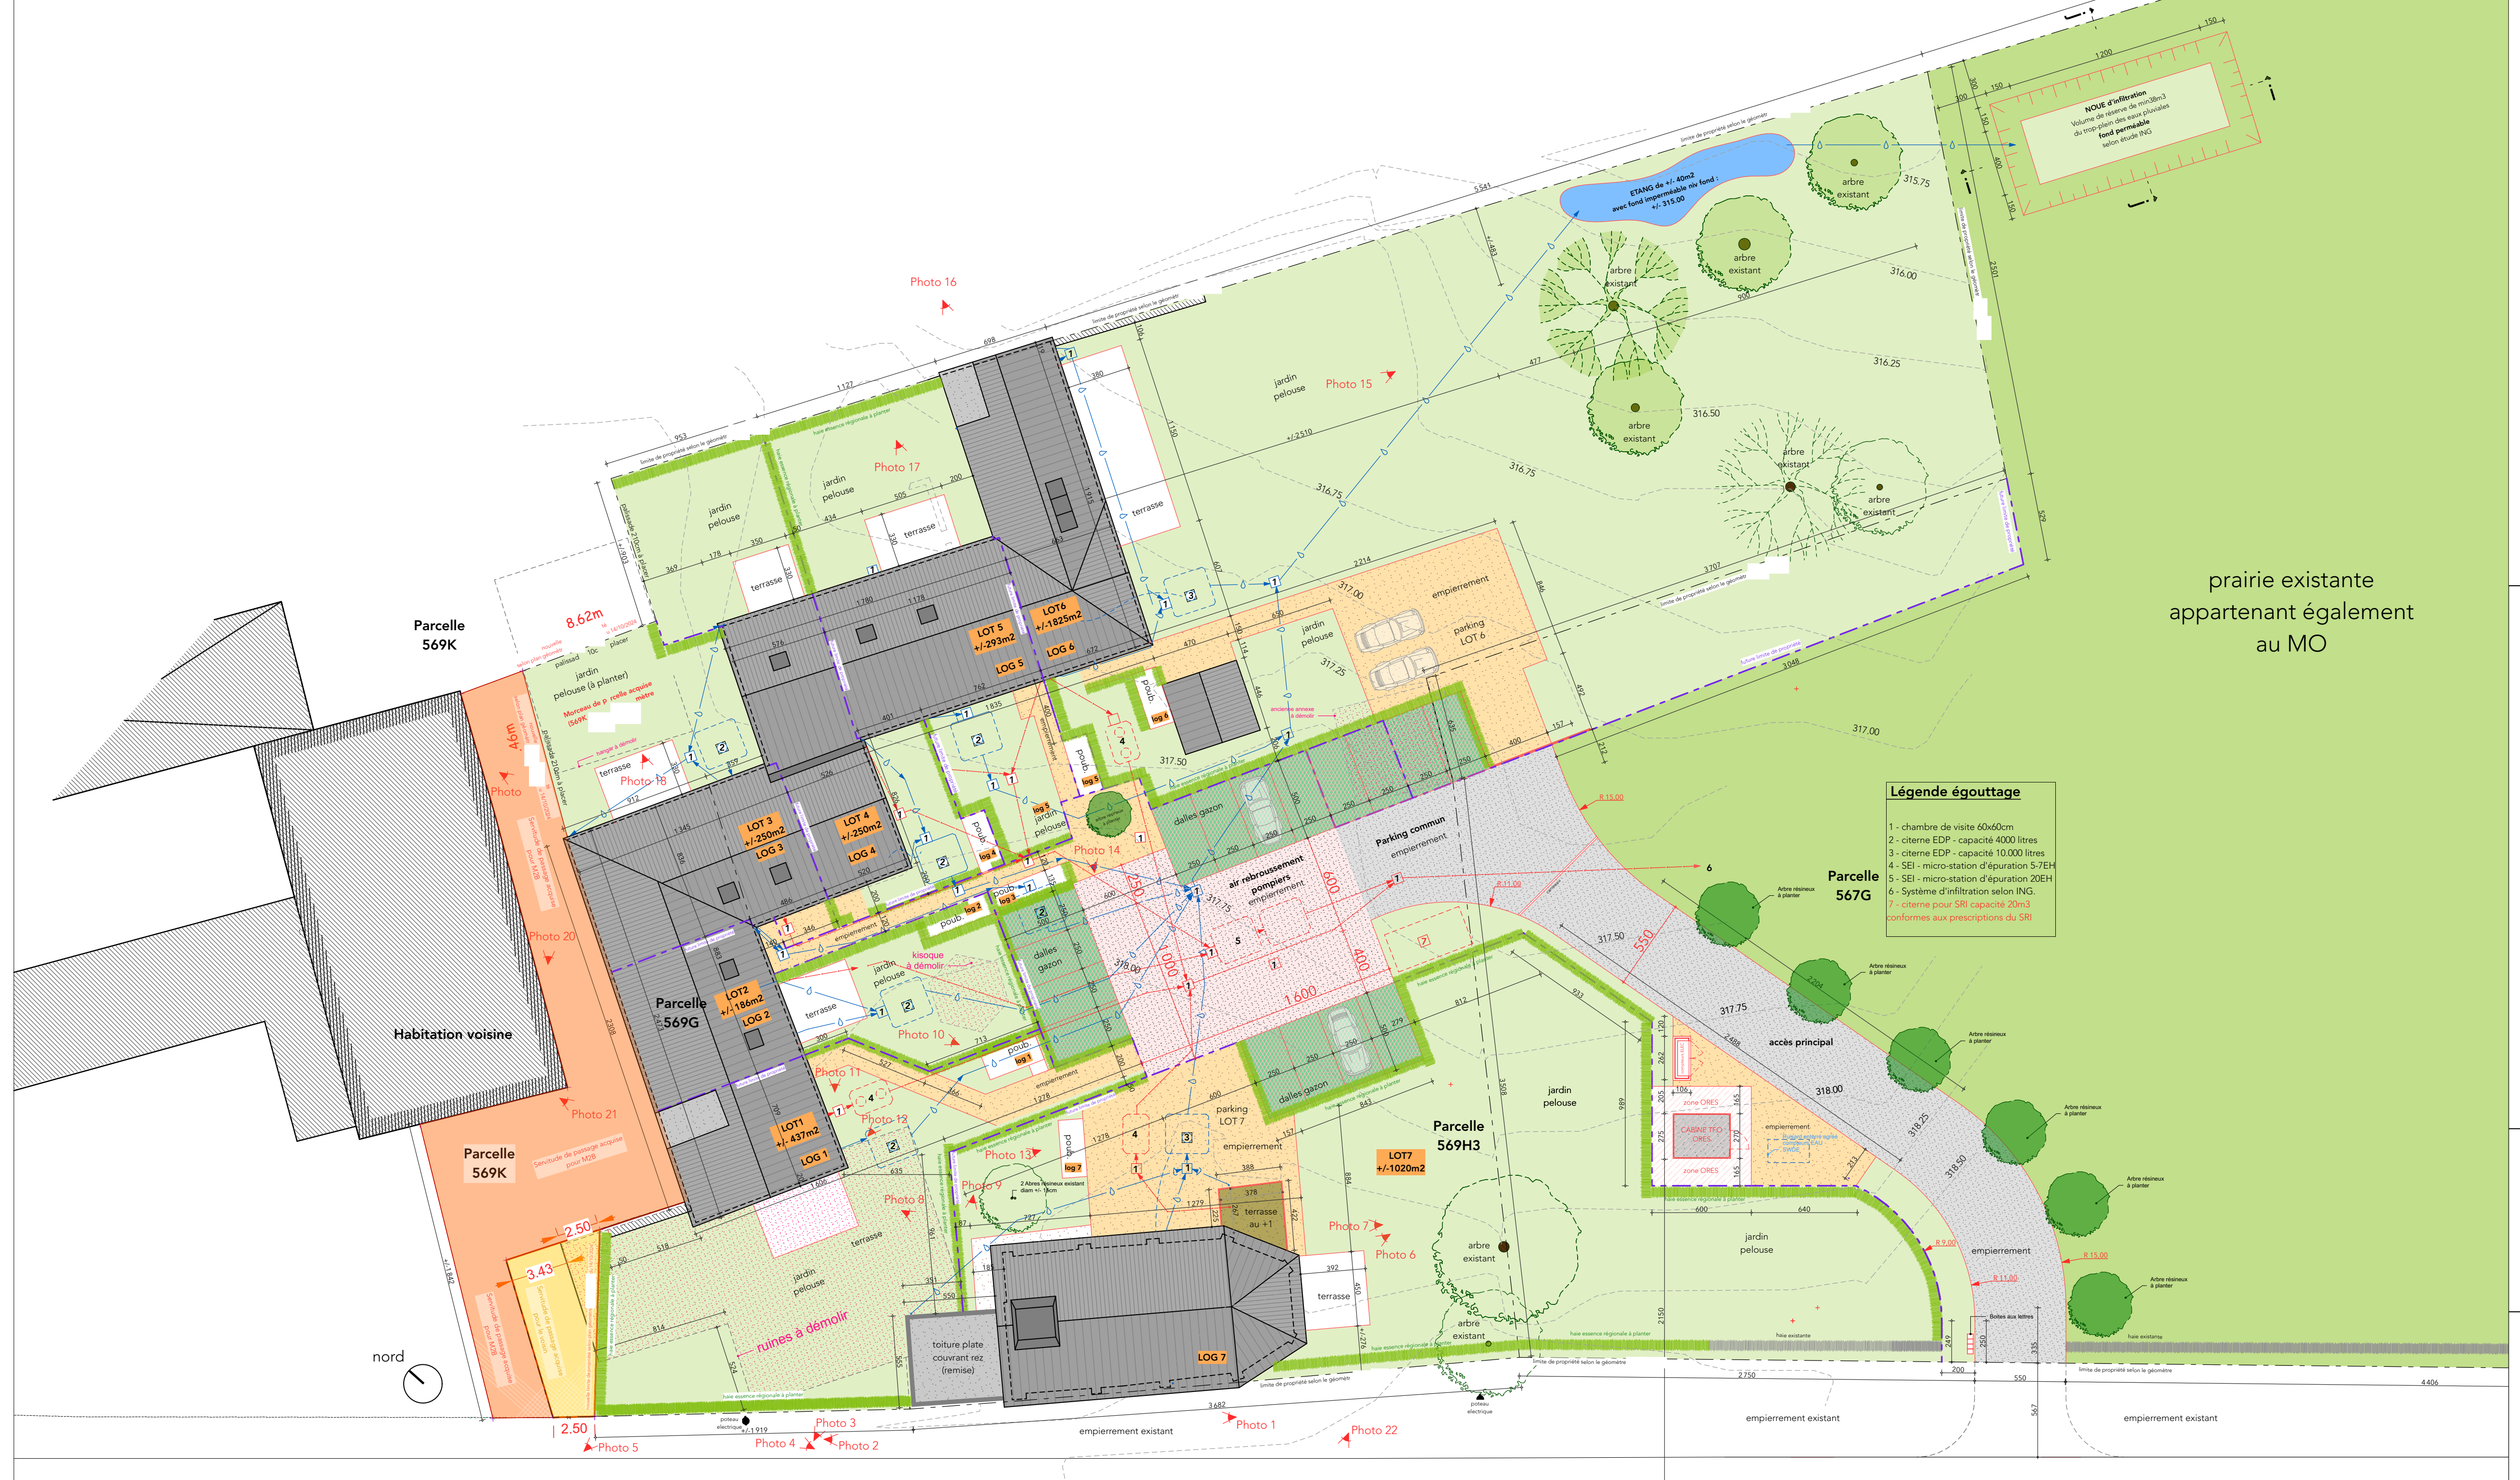
Parcelle 569K
Parcelle 569G
Parcelle 569H3
Parcelle 567G
Habitation voisine
prairie existante appartenant également au MO
accès principal
Arbre résineux à planter
future limite de propriété
3048
317.00
2204
LOG 7
toiture plate couvrant rez (remise)
ruines à démolir
haie essence régionale à planter
terrasse
arbre existant
poteau electrique
empierrement existant
limite de propriété selon le géomètre
2.50
Photo 1
Photo 2
Photo 3
Photo 4
Photo 5
Photo 22
nord
Servitude de passage acquise pour M2B
Axe de la N612
Rue du Mémorial Américain
voirie hydrocarbonnée équipée en eau-éléc-internet

Légende égouttage

1 - chambre de visite 60x60cm
2 - citerne EDP - capacité 4000 litres
3 - citerne EDP - capacité 10.000 litres
4 - SEI - micro-station d'épuration 5-7EH
5 - SEI - micro-station d'épuration 20EH
6 - Système d'infiltration selon ING.
7 - citerne pour SRI capacité 20m3
conformes aux prescriptions du SRI

Vue en plan - implantation
situation projetée
éch. 1/200e

Superficie des lots

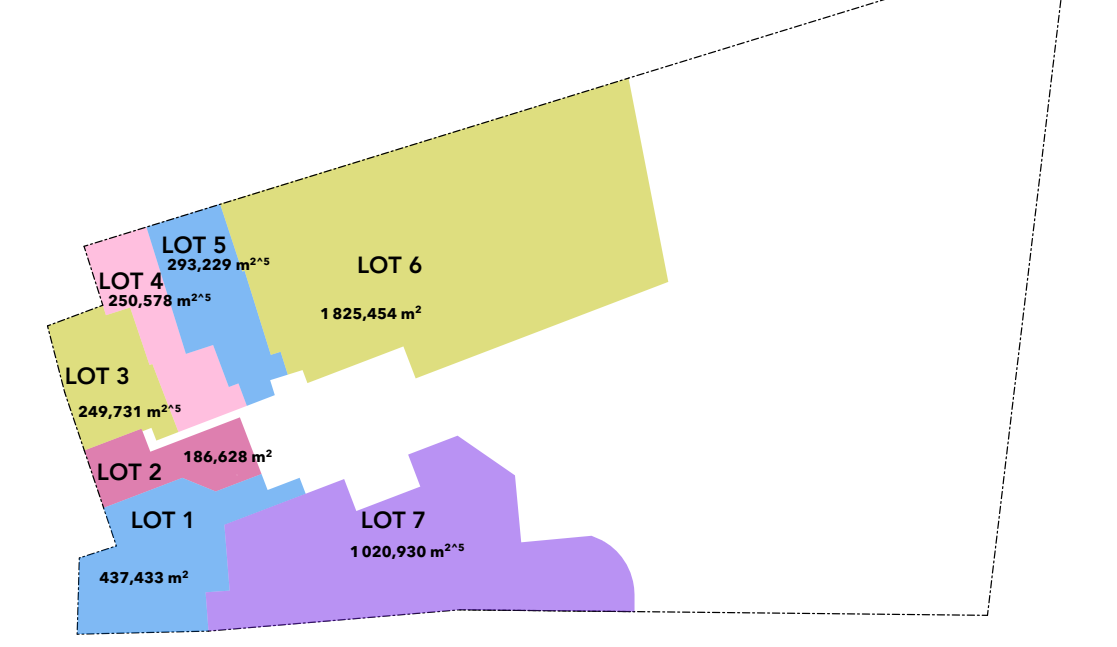

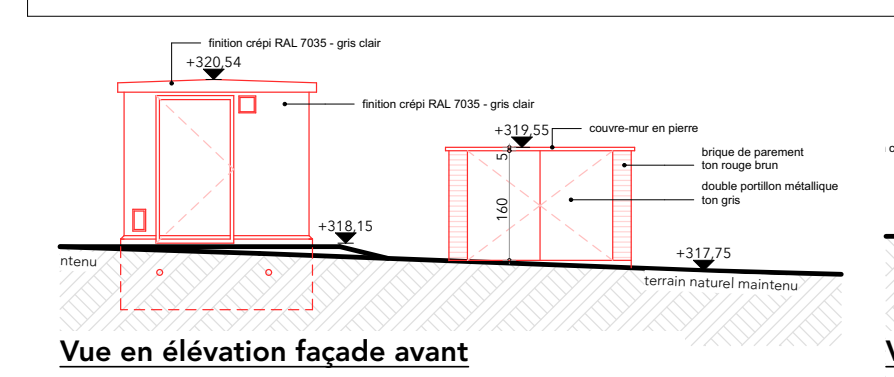
finition crépi RAL 7035 - gris clair
+320,54
finition crépi RAL 7035 - gris clair
+319,55
couvre-mur en pierre
brique de parement ton rouge brun
double portillon métallique ton gris
160
+318,15
+317,75
terrain naturel maintenu

Vue en élévation façade avant
- local ORES préfab + armoire compteur ELEC
situation projetée
éch. 1/100e

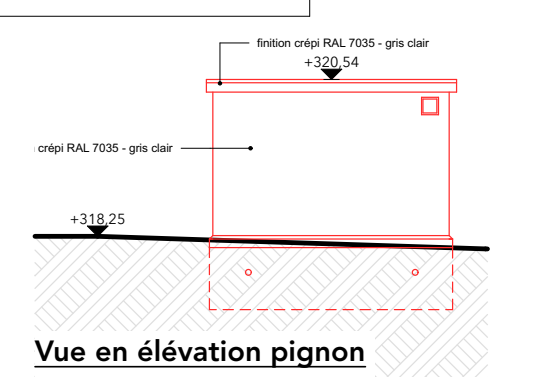
finition crépi RAL 7035 - gris clair
+320,54
crépi RAL 7035 - gris clair
+318,25

Vue en élévation pignon
- local ORES préfab
situation projetée
éch. 1/100e

Projet	**Transformation d'une chapelle à l'abandon et de l'ancien couvent de Gensterbloem en 7 logements**
Adresse	Rue du Mémorial Américain 231, à 4852 Plombières Cadastre : Plombières 4DIV / Section B / 569H3, 569G, 567G et une partie de la 569K
Administration	Urbanisme de Plombières

Maître de l'ouvrage

(représentée par

Auteur de projet

YA Architecture SRL

Evolution du dossier

Phase	Version	Date	Explicatif	Réalisé par
		19/06/2023	1ère réunion de Patrimoine (sans la présence de l'auteur de projet) sur site	
AP		12/02/2024	Présentation de l'AP3 au Patrimoine et au SPW, au SPW à Liège	
PU	A	14/03/2025	Tracé de la demande de permis d'urbanisme	YM
PU	**B**	**10/11/2025**	**Plans modificatifs selon exigences des pompiers (air de rebroussement,...)**	**YM**

Légende des matériaux utilisés dans les plans et coupes

▨	Maçonnerie existante	🟥	Bloc de béton	▨	Isolant	▨	Parement en brique
▨	Terrain	▨	Empierrement	🟥	Béton armé	🟥	Chape et finition sol

Contenu de la feuille	N° de Dossier	Maître de l'ouvrage
Implantation - façades - plans coupes	**2336**	**M2B**

Feuille n°	Version	Phase	Date	Echelle	Réalisé par
2/3	**B**	**PU**	**10/11/25**	**voir plans**	**YM**

YA Architecture SRL

Ce document est la propriété de YA Architecture SRL. Toute reproduction ou communication à des tiers en est interdite sans son autorisation préalable