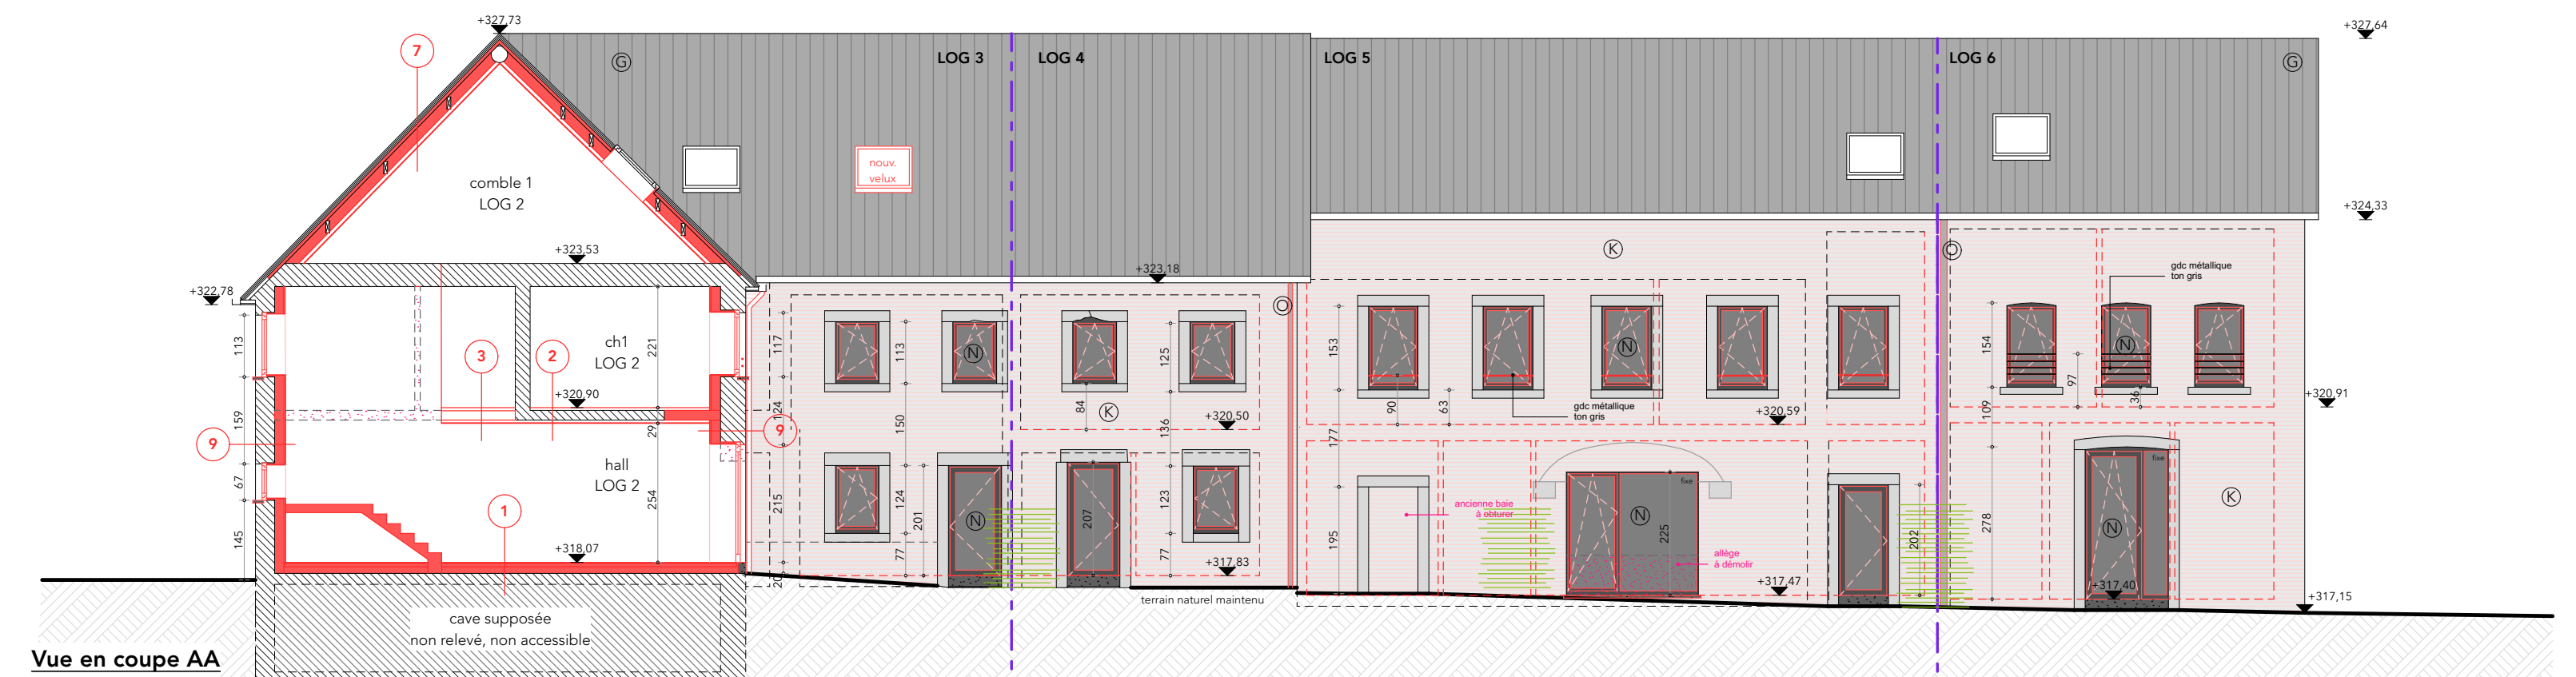

**Vue en coupe AA**
situation projetée
éch. 1/100e

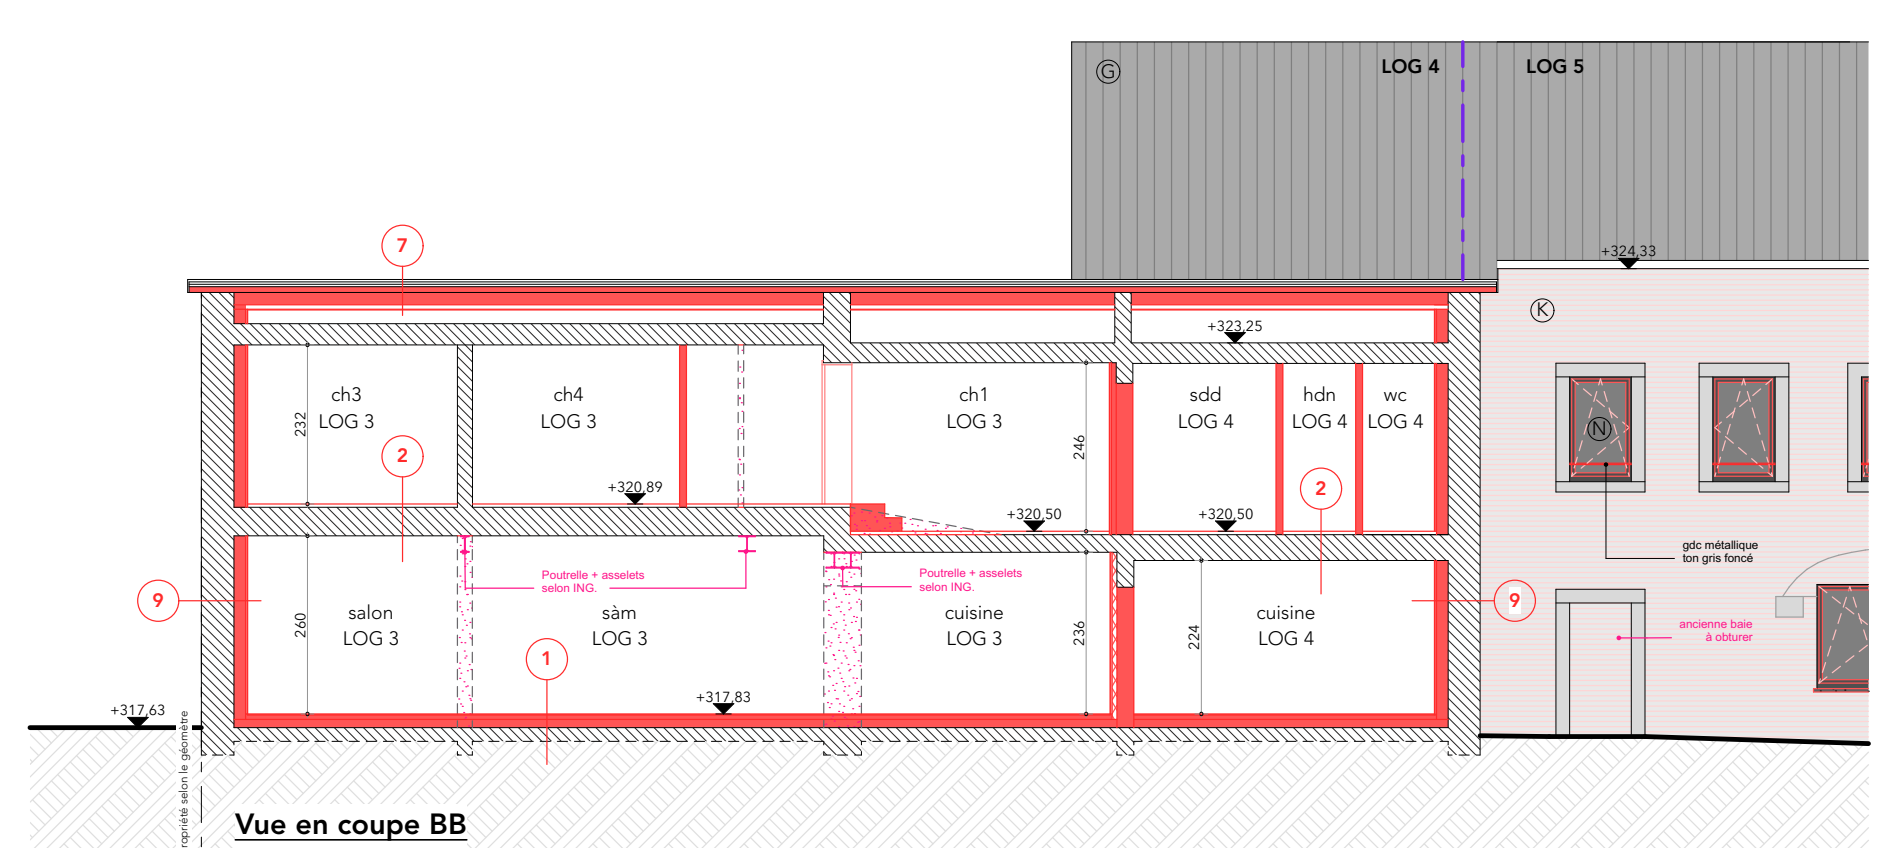

**Vue en coupe BB**
situation projetée
éch. 1/100e

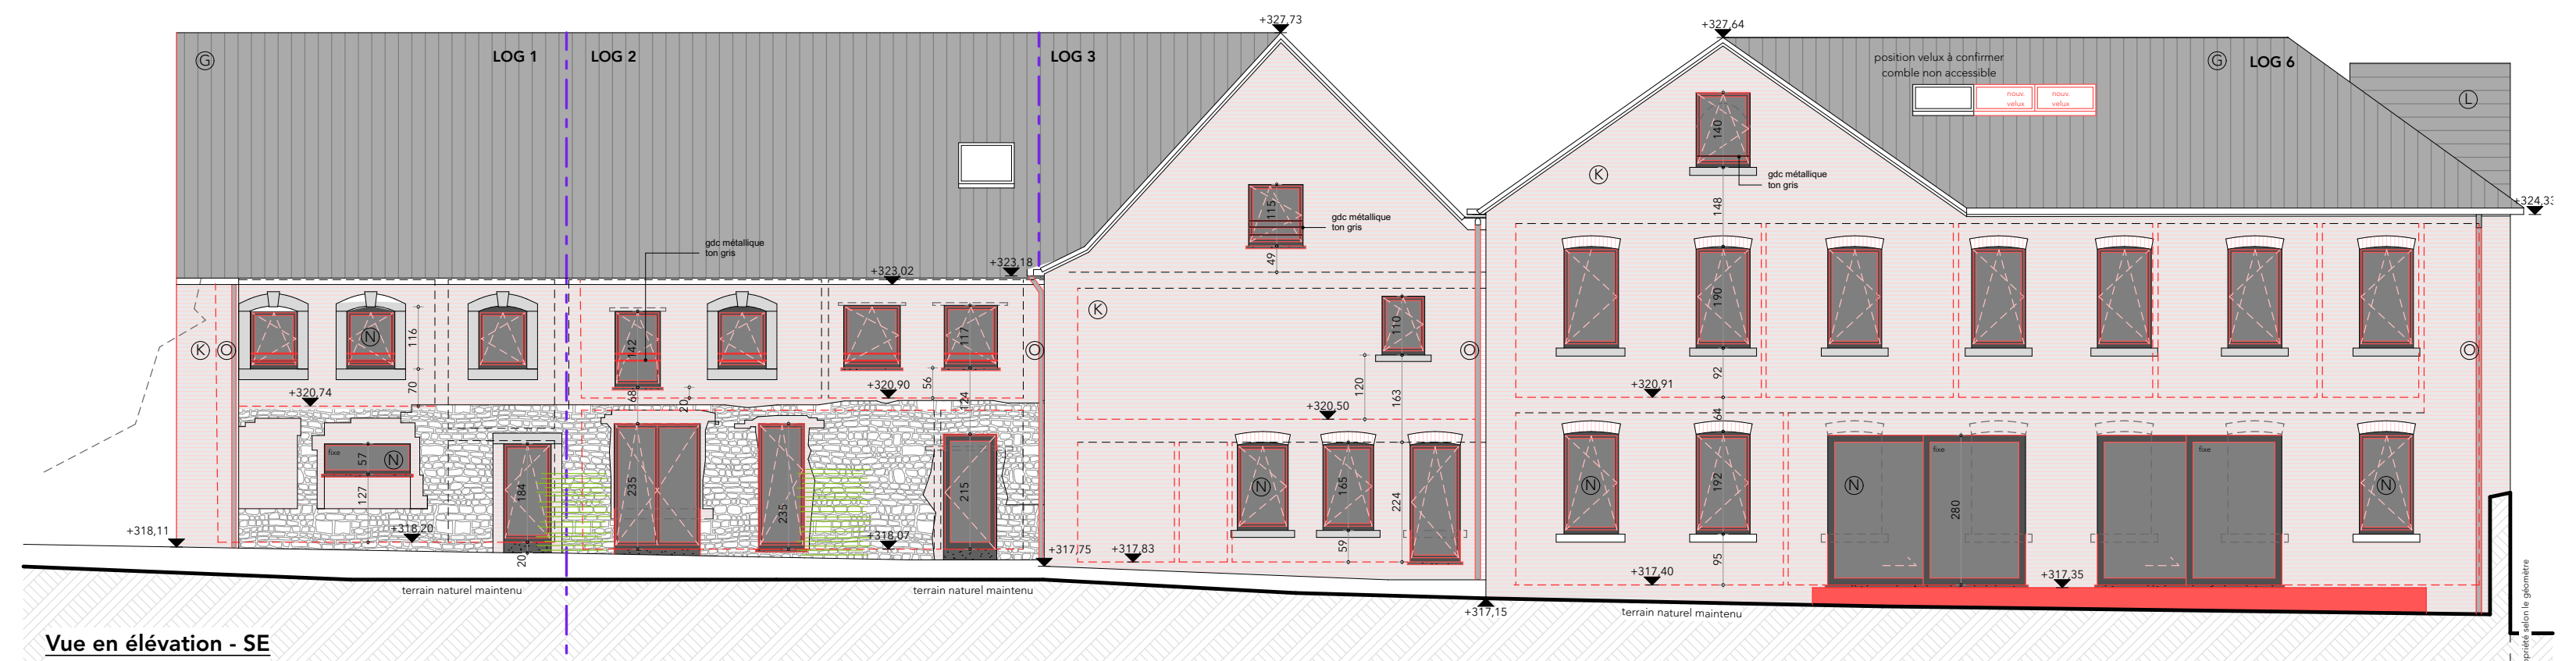

**Vue en élévation - SE**
situation projetée
éch. 1/100e

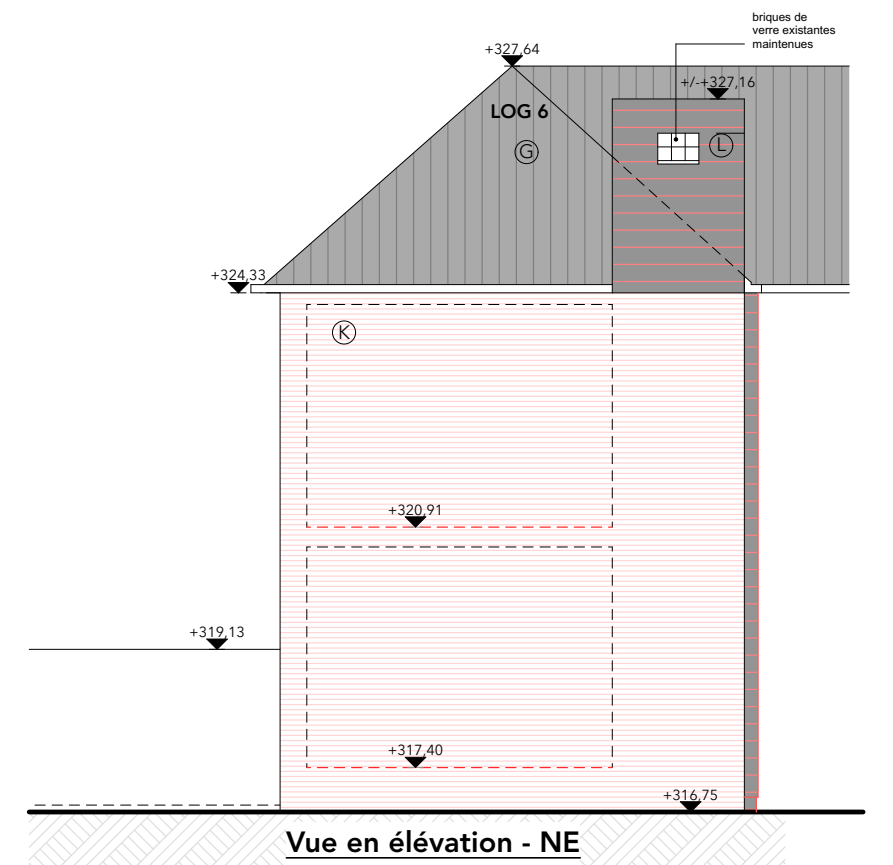

**Vue en élévation - NE**
situation projetée
éch. 1/100e

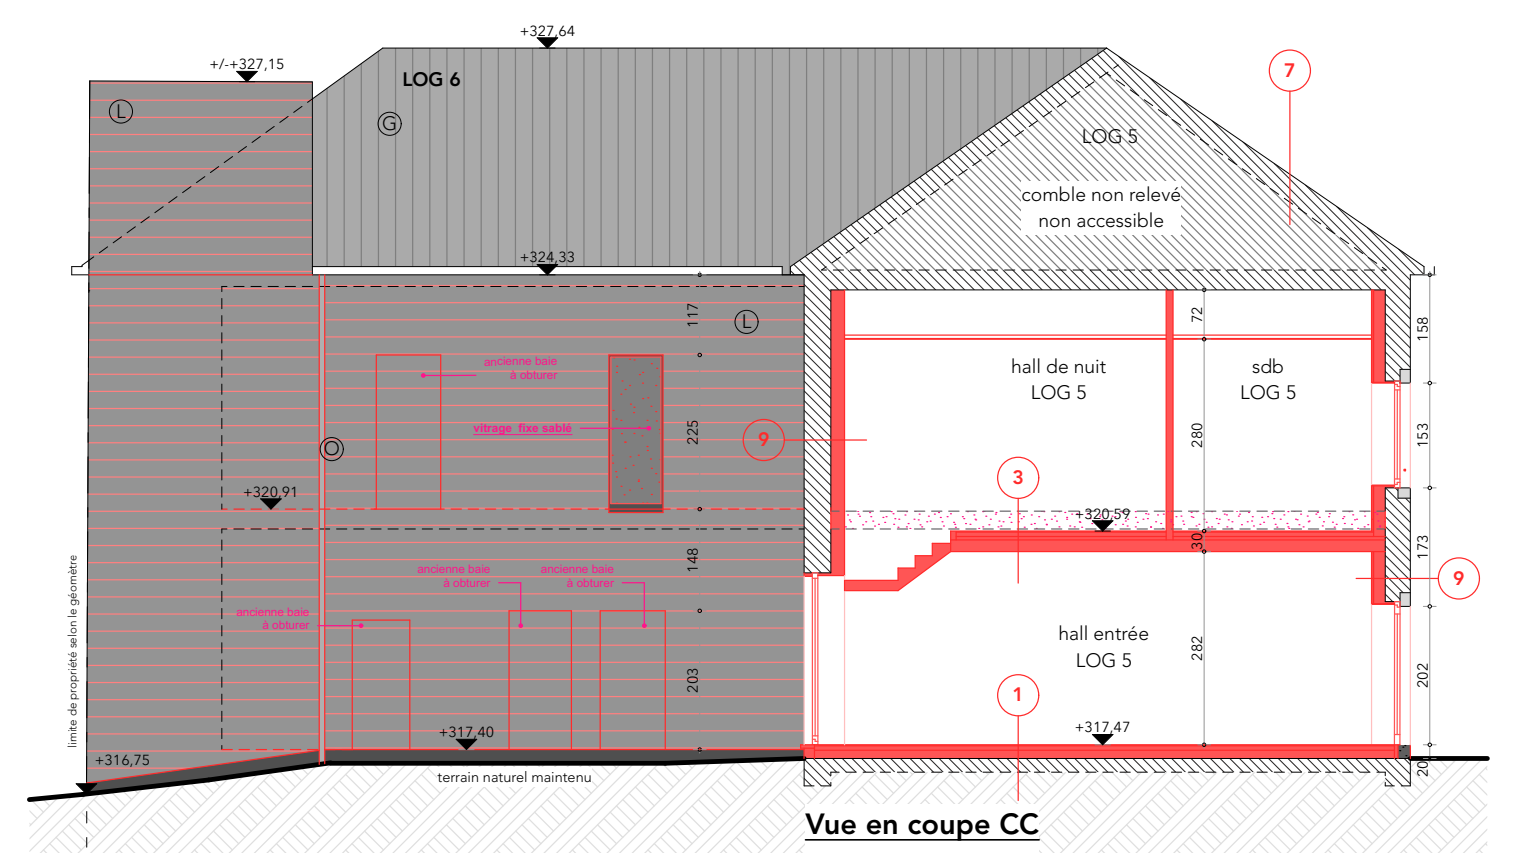

**Vue en coupe CC**
situation projetée
éch. 1/100e

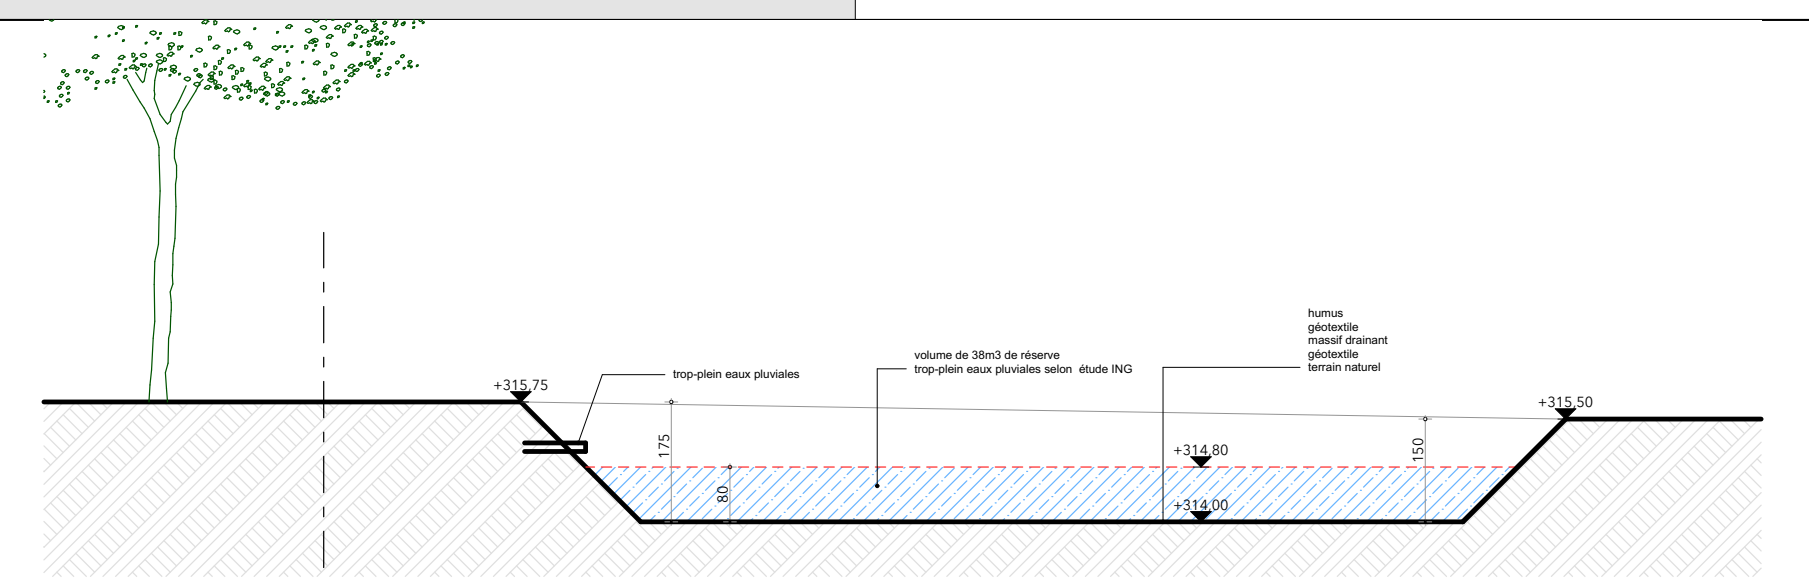
+315,75
trop-plein eaux pluviales
volume de 38m3 de réserve
trop-plein eaux pluviales selon étude ING
humus
géotextile
massif drainant
géotextile
terrain naturel
+315,50
+314,80
+314,00
175
80
150

**Vue en coupe jj**
situation projetée
éch. 1/100e

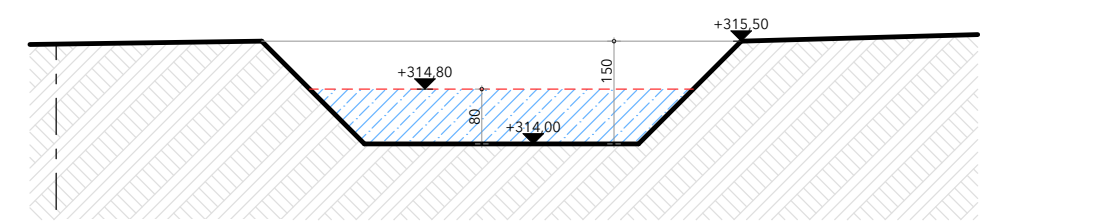

**Vue en coupe jj**
situation projetée
éch. 1/100e

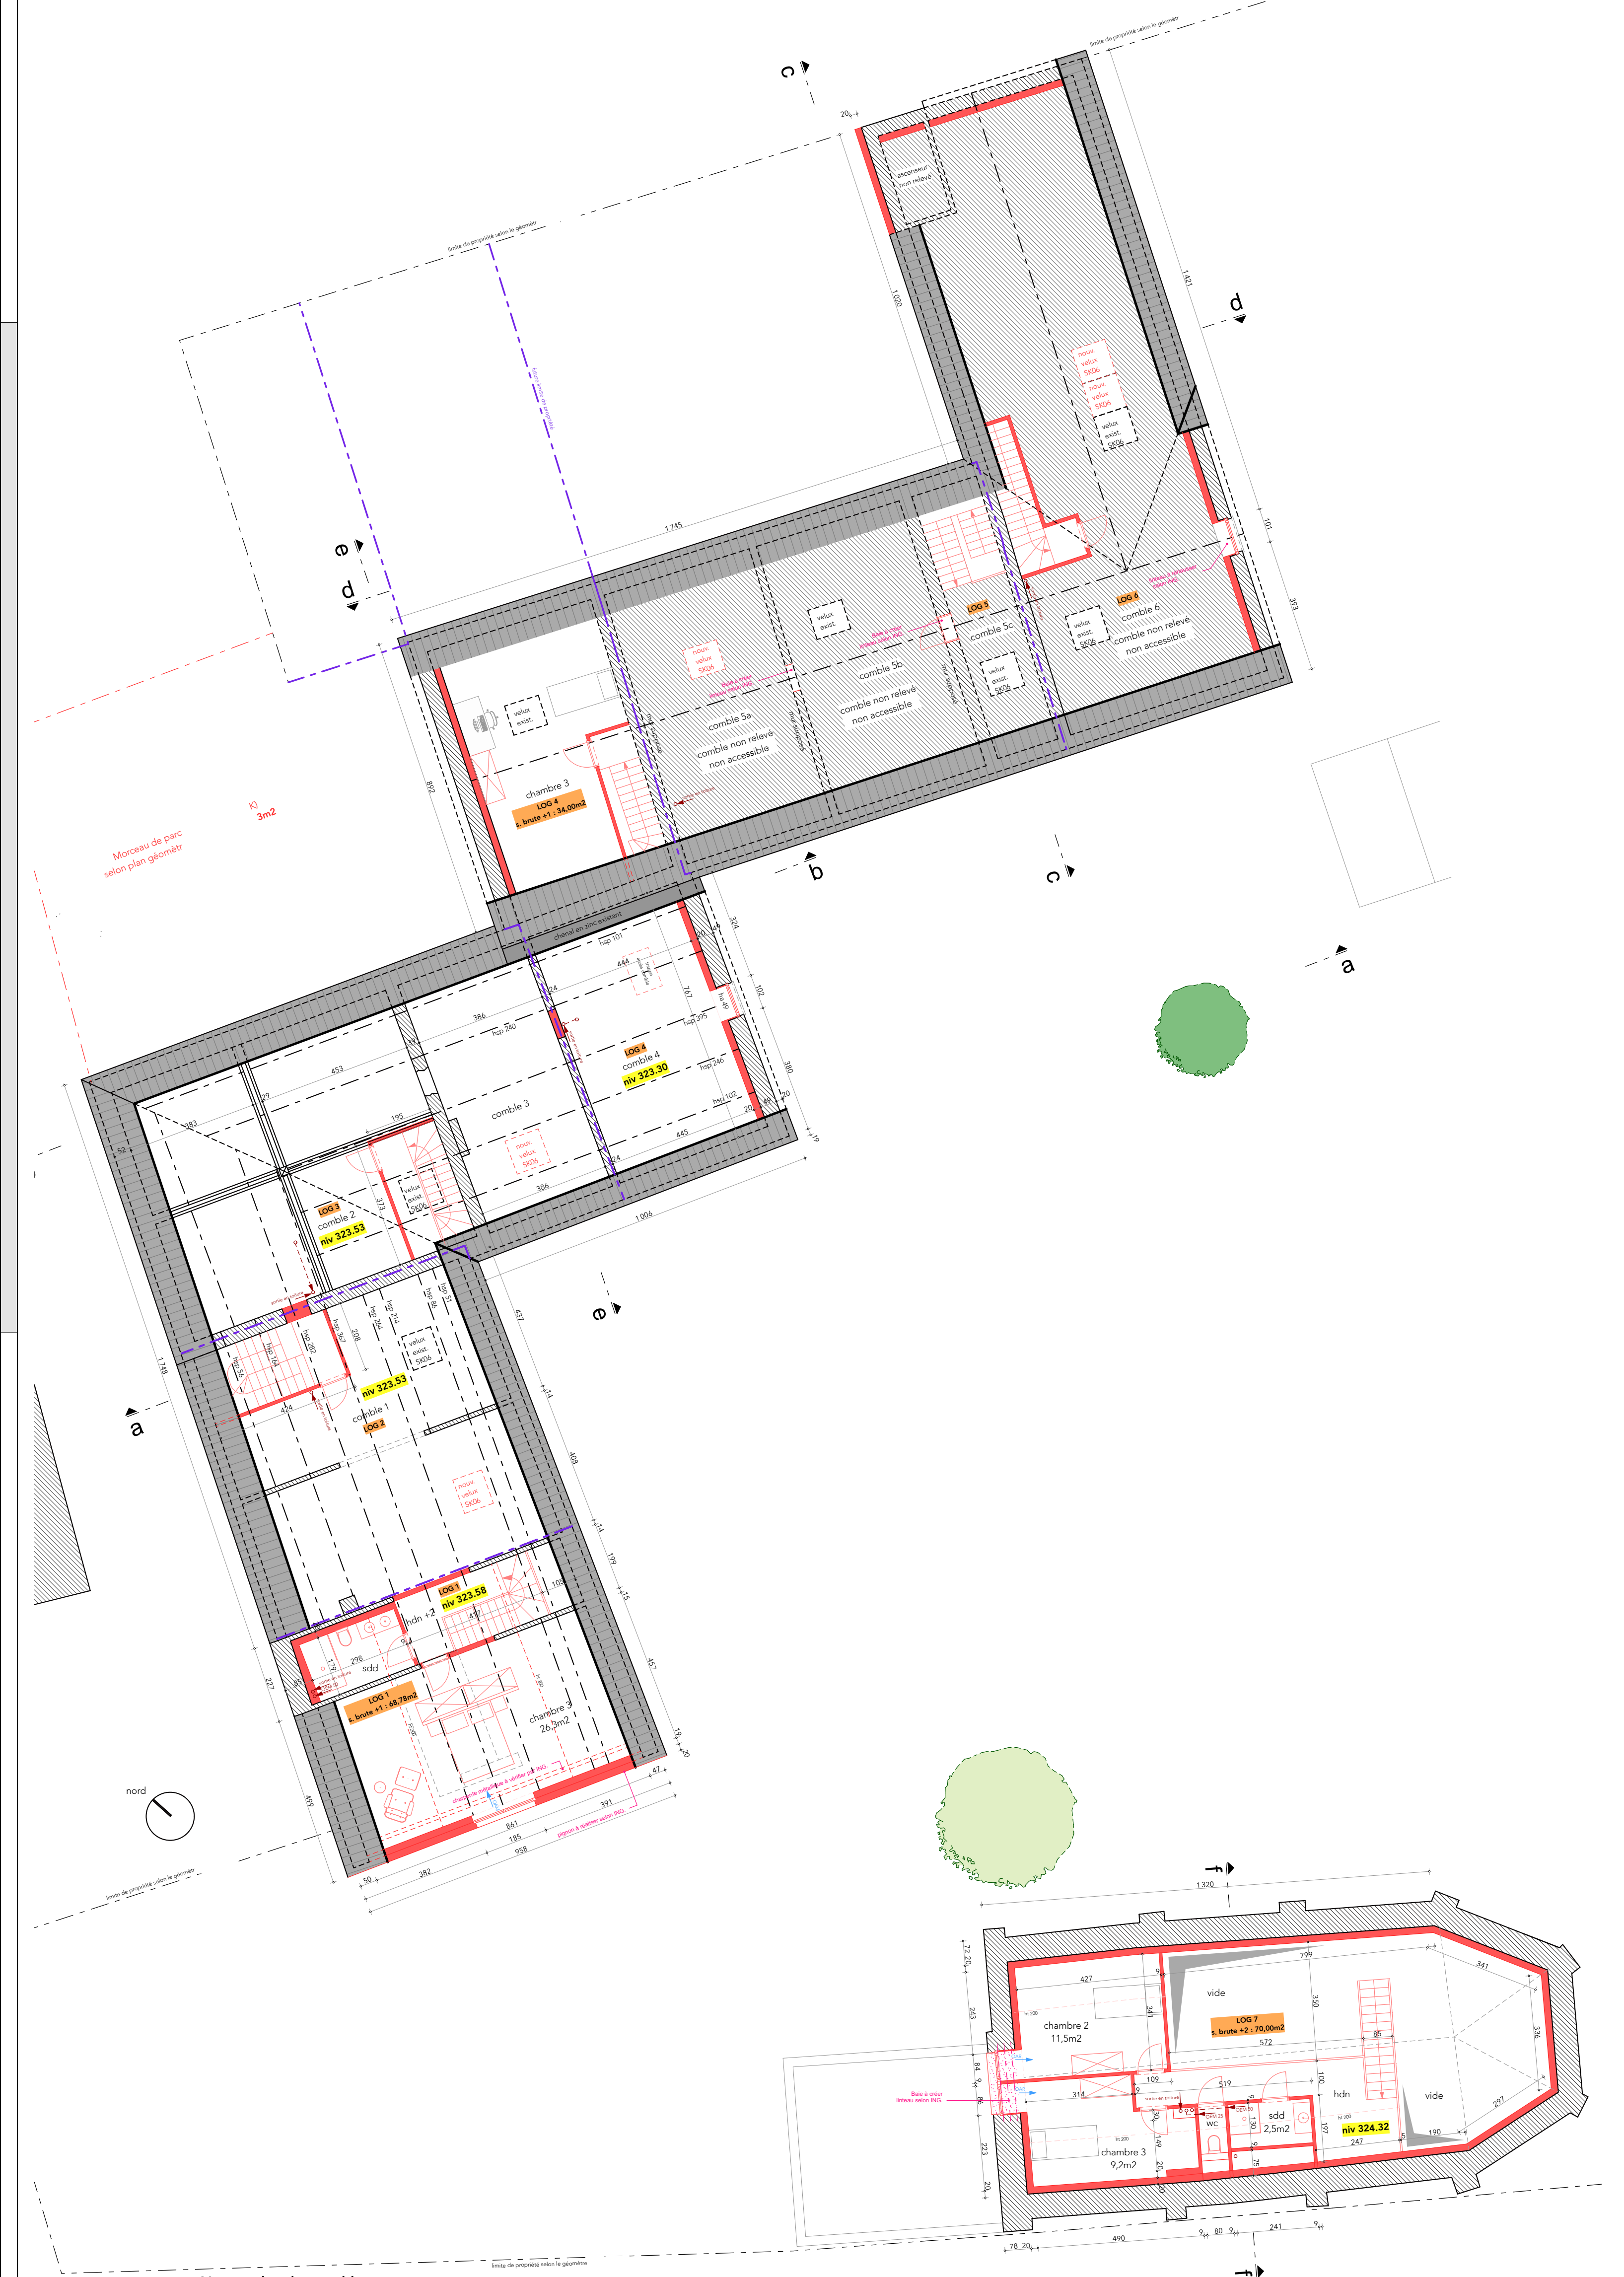

**Vue en plan des combles**
situation projetée
éch. 1/100e

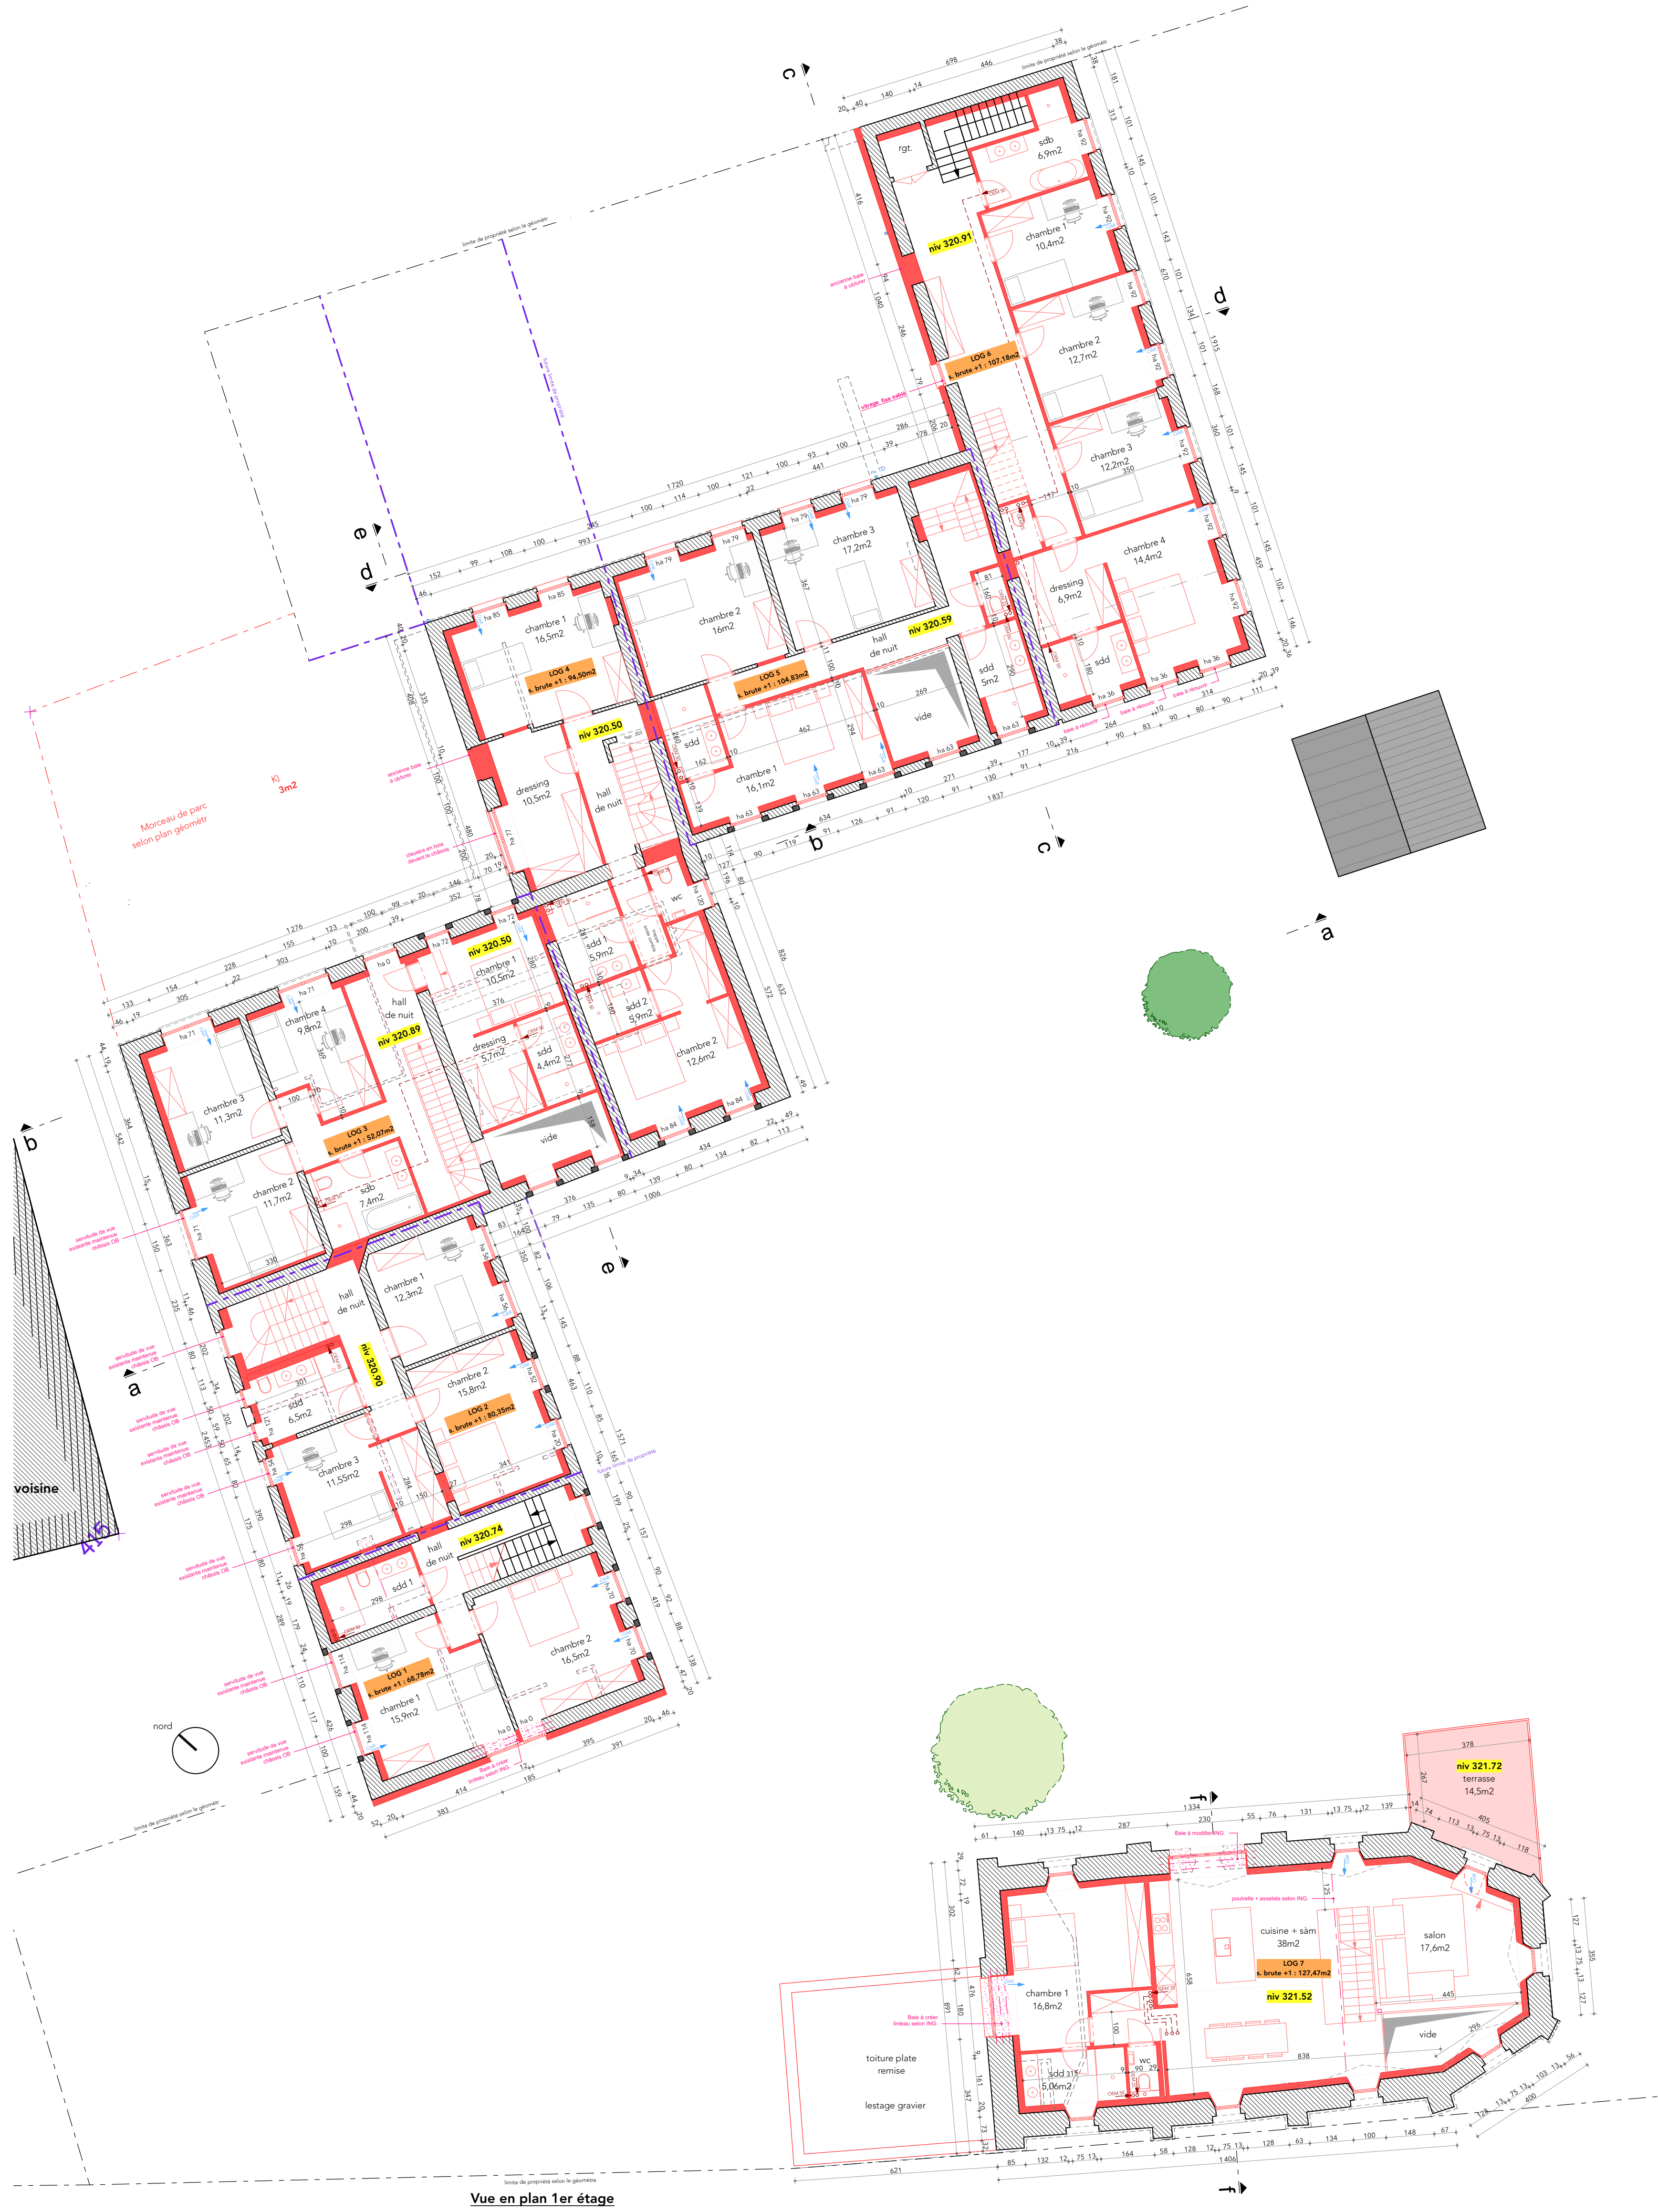

**Vue en plan 1er étage**
situation projetée
éch. 1/100e

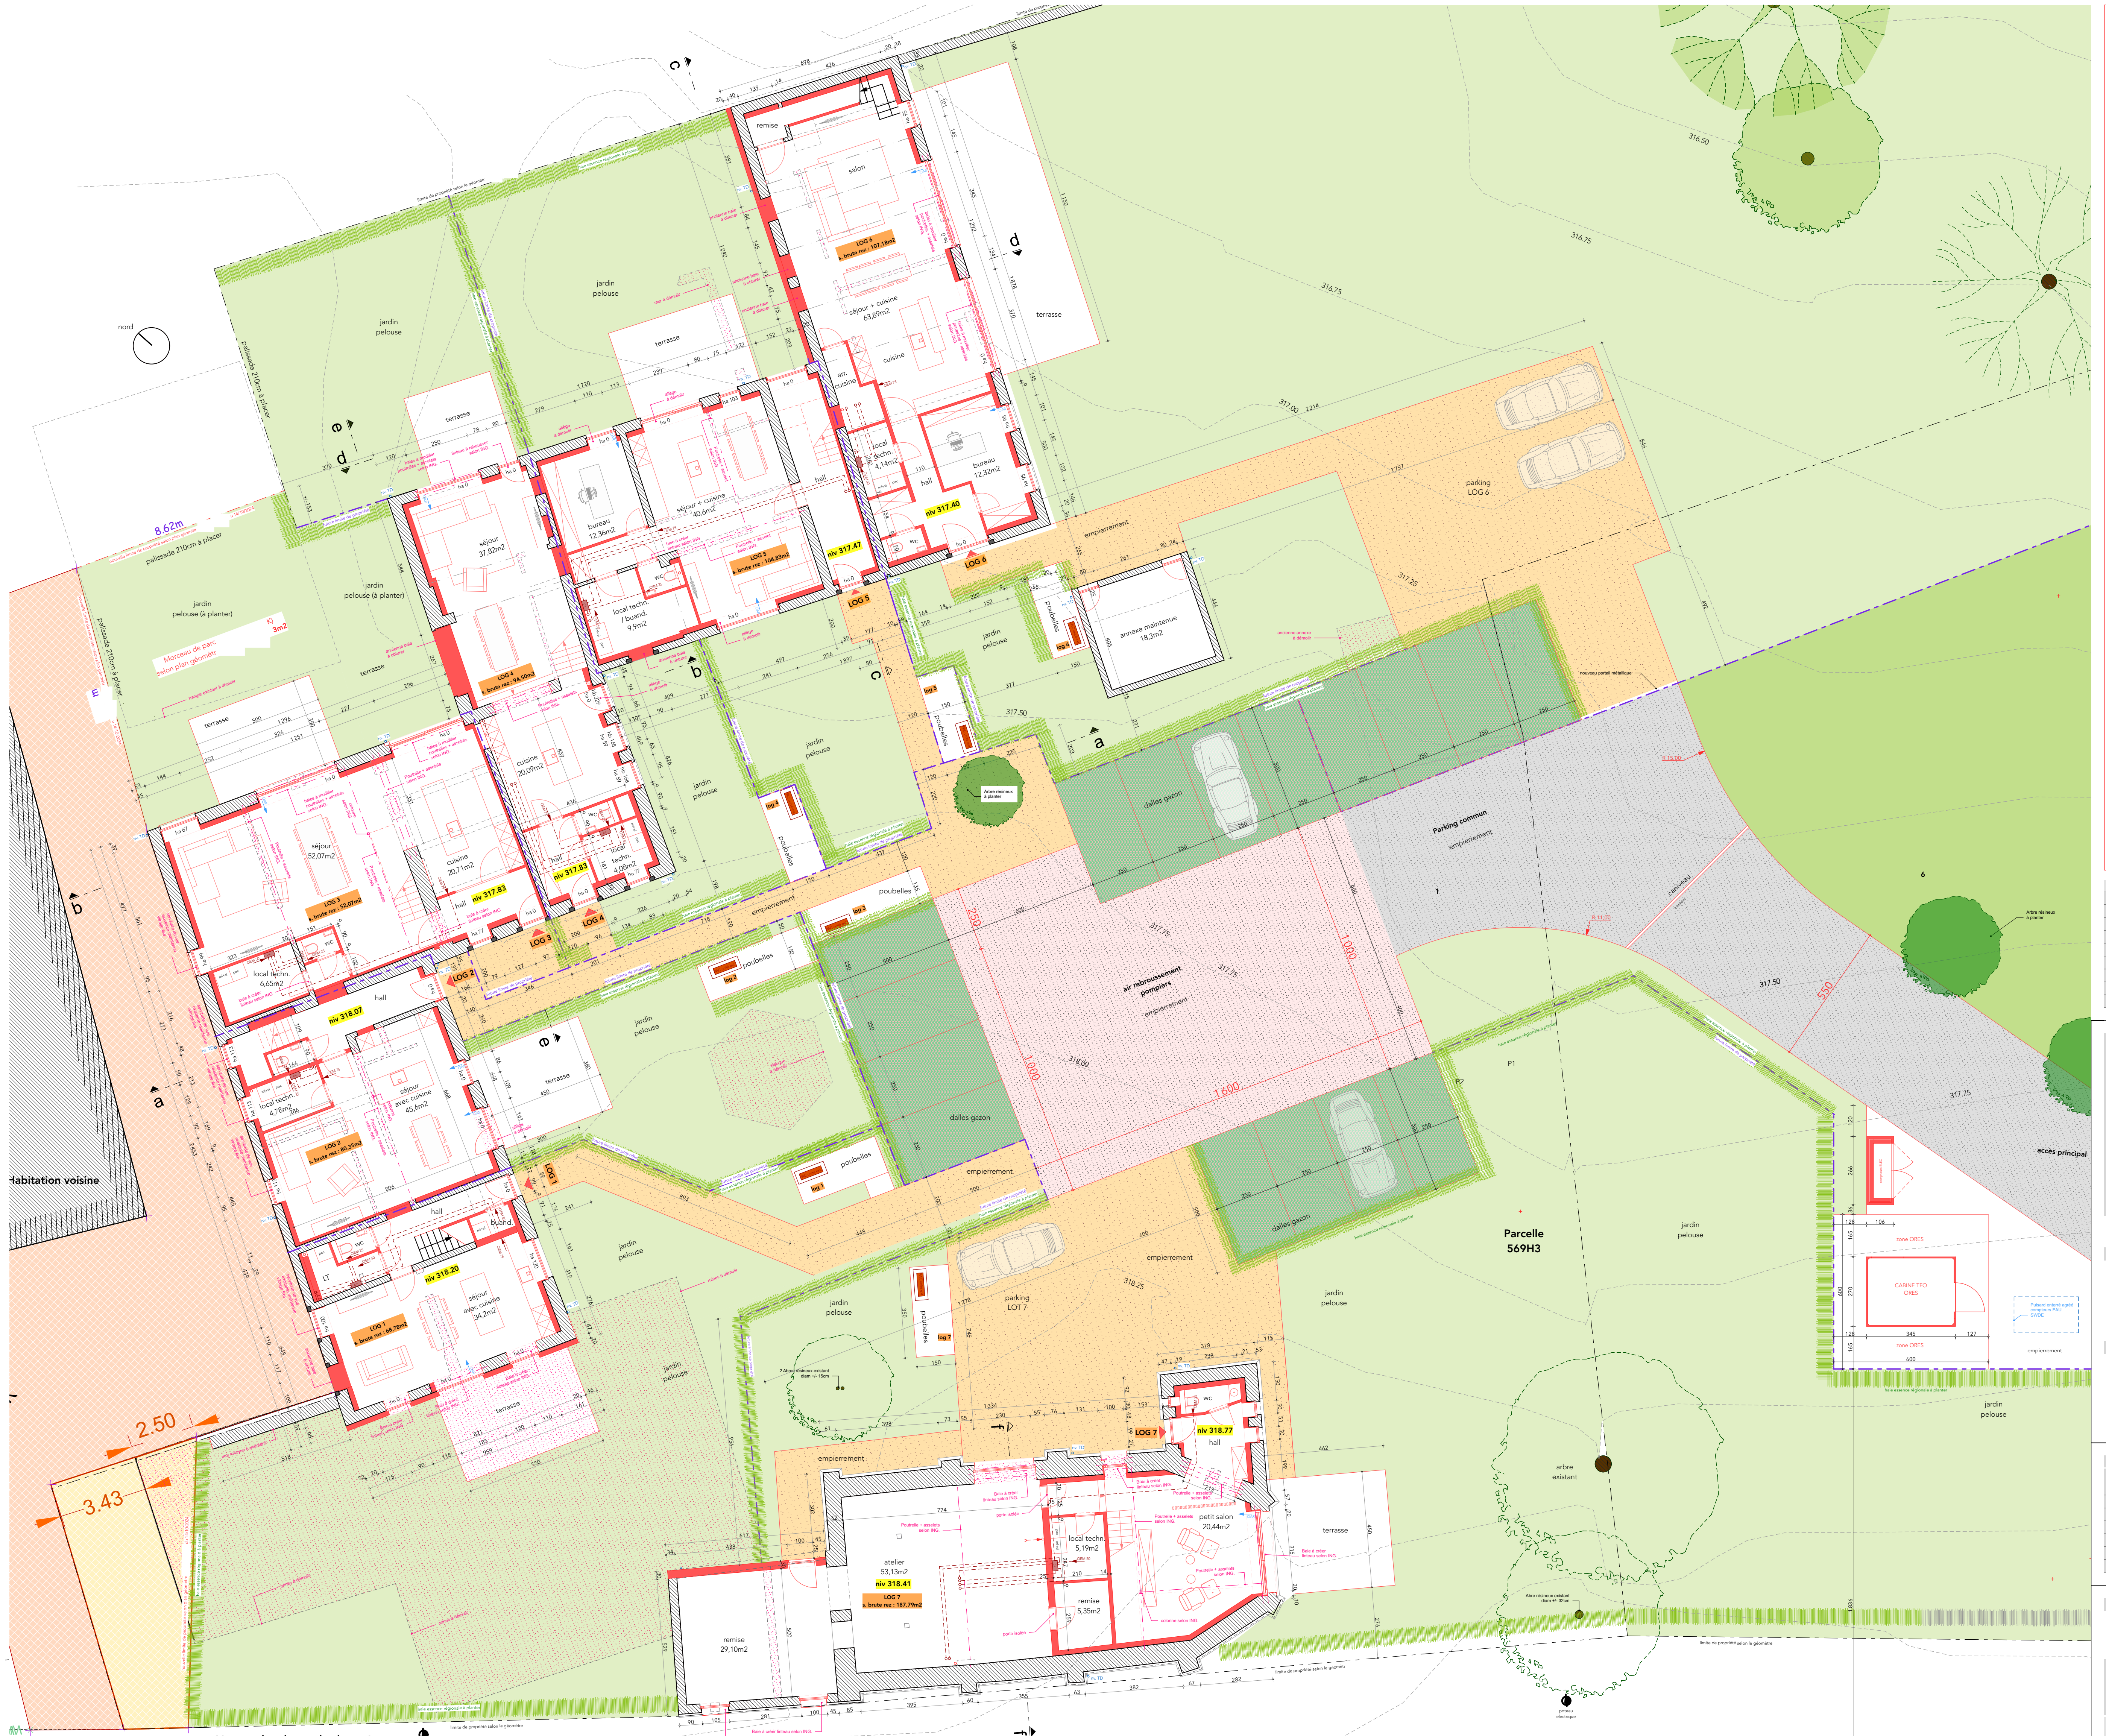
2.50
3.43
nouvelle limite de propriété selon
ruines à démolir
haie essence régionale à planter
limite de propriété selon le géomètre
poteau electrique
Arbre résineux à planter
accès principal
Puisard enterré agréé compteurs EAU SWDE
empierrement
Parcelle 569H3

**Vue en plan du rez-de-chaussée**
situation projetée
éch. 1/100e

**Composition des parois:**

① Dalle sur sol existante
carrelage + chape 8cm
chape PU projeté 12cm
dalle de sol existante

② Plancher existant
parquet
panneau d'égalisation
plancher existant (béton OU gitage en bois)
lattage technique éventuel
plaque de plâtre

③ Nouveau plancher en béton
parquet + chape 8cm
poutrains + claveaux selon ing. + chape de compression
plafonnage

④ Nouveau plancher en béton isolé
parquet + chape 8cm
chape PU projeté10cm
poutrains + claveaux selon ing. + chape de compression
plafonnage

⑤ Nouvelle dalle sur sol isolée (chapelle)
carrelage + chape 8cm
chape PU projeté12cm
dalle BA selon ing.
sable stabilisé
empierrement

⑥ Nouvelle dalle sur sol non isolée (chapelle)
chape lissée 8cm
dalle BA selon ing.
sable stabilisé
empierrement

⑦ Toiture existante
tuiles en terre cuite
lattage + c-l + sous-toiture
chevrons 6 (ou 8cm selon versant) + nouvelle isolation en laine minérale 6 (ou 8cm)
pannes + nouvelle isolation en laine minérale 18cm
pare-vapeur
lattage + plaque de plâtre

⑧ Nouvelle couverture de toiture (chapelle)
ardoise en fibro-ciment
lattage + c-l + sous-toiture
PU 12cm (sarking)
pare-vapeur
chevrons existants (supposés)
charpente existante
faux-plafond existant

⑨ Murs existants
peinture à la chaux ton blanc cassé
mur existant en briques de terre cuite (ép variable entre 39 et 49cm)
PU projeté sur les murs ép. 15cm
lattage technique
panneau en OSB
plaque de plâtre

⑩ Murs existants (chapelle)
mur existant en moellons (ép. +/- 70cm)
PU projeté sur les murs ép. 15cm
lattage technique
panneau en OSB
plaque de plâtre

⑪ Murs existants isolés et ardoisés
parement en ardoises de fibro-ciment
lattage +c-l + pare-pluie
PU 12cm
mur existant en briques de terre cuite (ép. variable entre 39 et 49cm)
plafonnage

⑫ Nouveau pignon (logement 1)
parement en bardage bois ajourée
lattage +c-l + pare-pluie
PU 12cm
bloc béton 14cm
plafonnage

Légende des matériaux - **PROJETÉS**

| | | | |
|---|---|---|---|
| Ⓚ | Parement principal | Maçonnerie en briques de terre cuite | peint à la chaux ton blanc cassé |
| Ⓛ | Bardage | Ardoises fibro-ciment | ton gris foncé |
| Ⓜ | Bardage | Bois | ton naturel |
| Ⓝ | Menuiseries extérieures | Aluminium ou PVC | ton gris |
| Ⓞ | Tuyaux de descente | Zinc | naturel (gris clair) |
| Ⓟ | Couverture | Ardoises fibro-ciment | ton gris foncé |
| Ⓠ | Seuils | Aluminium | ton gris |
| Ⓡ | Seuils | Pierre | ton naturel (gris) |
| Ⓢ | Parement secondaire | Maçonnerie en briques de terre cuite | ton rouge-brun (sablage - rejointoyage) |

| | |
|---|---|
| Projet | **Transformation d'une chapelle à l'abandon et de l'ancien couvent de Gensterbloem en 7 logements** |
| Adresse | Rue du Mémorial Américain 231, à 4852 Plombières<br>Cadastre : Plombières 4DIV / Section B / 569H3, 569G, 567G et une partie de la 569K |
| Administration | Urbanisme de Plombières |

Maître de l'ouvrage

(représentée par

Auteur de projet

**YA Architecture SRL**

Evolution du dossier

| Phase | Version | Date | Explicatif | Réalisé par |
|---|---|---|---|---|
| | | 19/06/2023 | 1ère réunion de Patrimoine (sans la présence de l'auteur de projet) sur site | |
| AP | | 12/02/2024 | Présentation de l'AP3 au Patrimoine et au SPW, au SPW à Liège | |
| PU | A | 14/03/2025 | Tracé de la demande de permis d'urbanisme | YM |
| **PU** | **B** | **10/11/2025** | **Plans modificatifs selon exigences des pompiers (air de rebroussement,...)** | **YM** |

Légende des matériaux utilisés dans les plans et coupes

| | | | | | | | |
|---|---|---|---|---|---|---|---|
| ▨ | Maçonnerie existante | 🟥 | Bloc de béton | ▨ | Isolant | ▨ | Parement en brique |
| ▨ | Terrain | ▨ | Empierrement | 🟥 | Béton armé | 🟥 | Chape et finition sol |

| Contenu de la feuille | N° de Dossier | Maître de l'ouvrage | | |
|---|---|---|---|---|
| **Façades- Plans - Coupes** | **2336** | **M2B** | | |

| Feuille n° | Version | Phase | Date | Echelle | Réalisé par |
|---|---|---|---|---|---|
| **3/3** | **B** | **PU** | **14/11/25** | **voir plans** | **YM** |

YA Architecture SRL

Ce document est la propriété de YA Architecture SRL. Toute reproduction ou communication à des tiers en est interdite sans son autorisation préalable